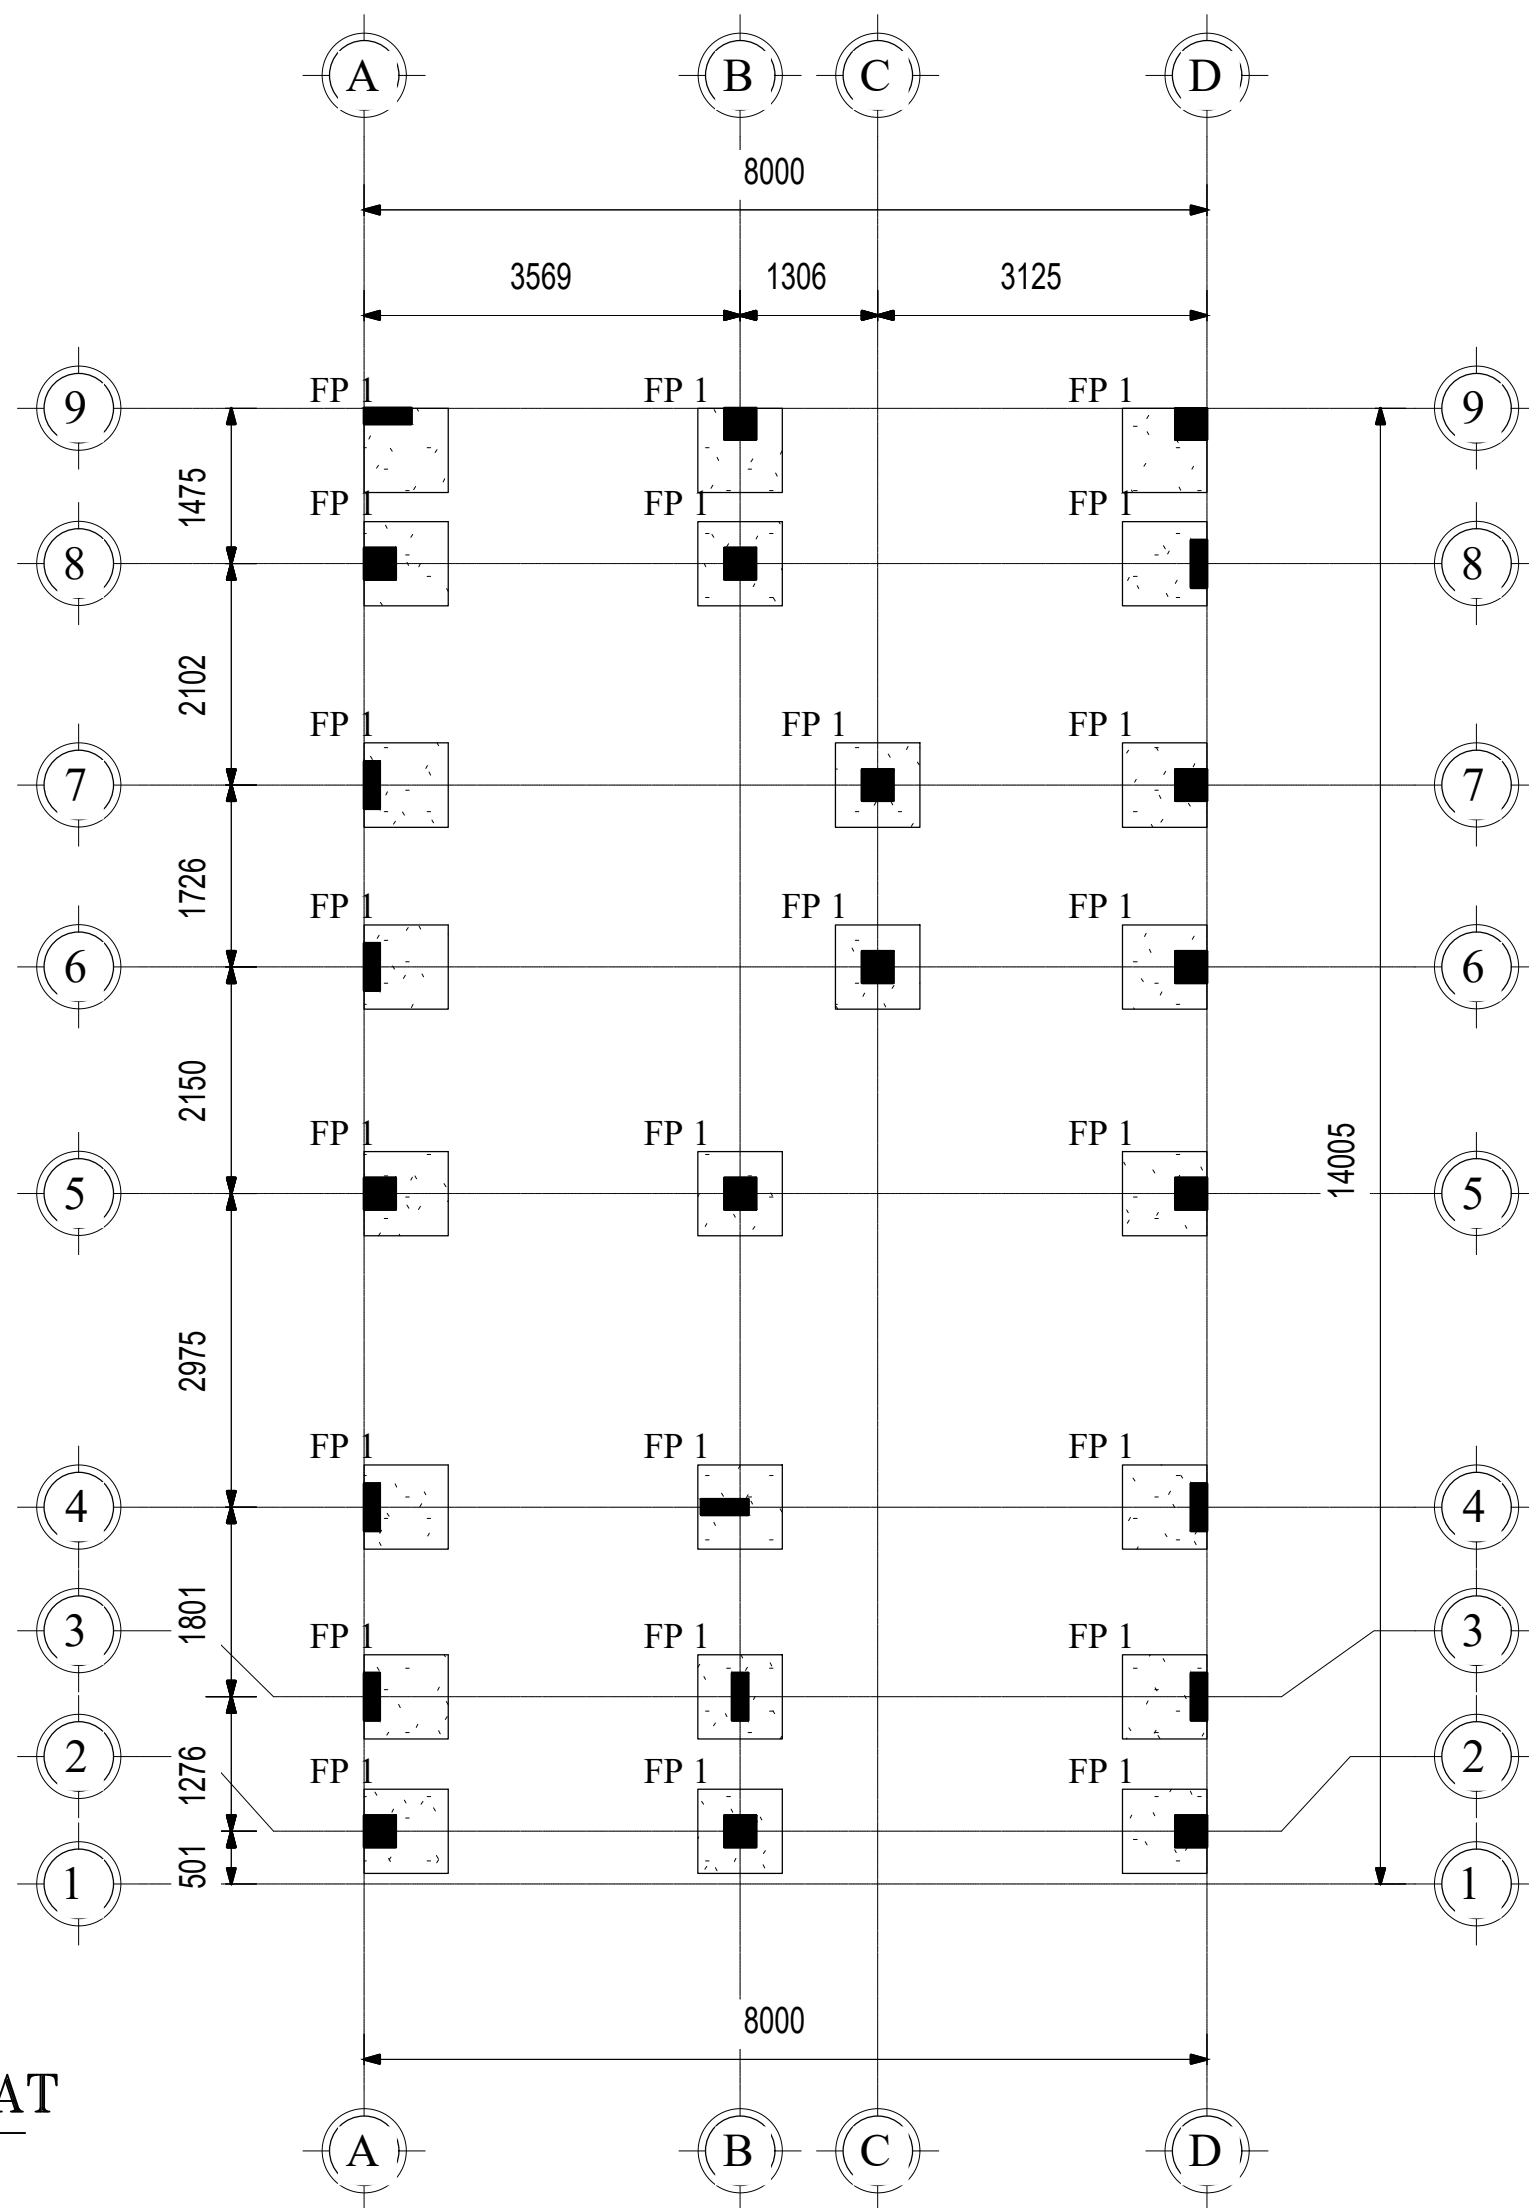
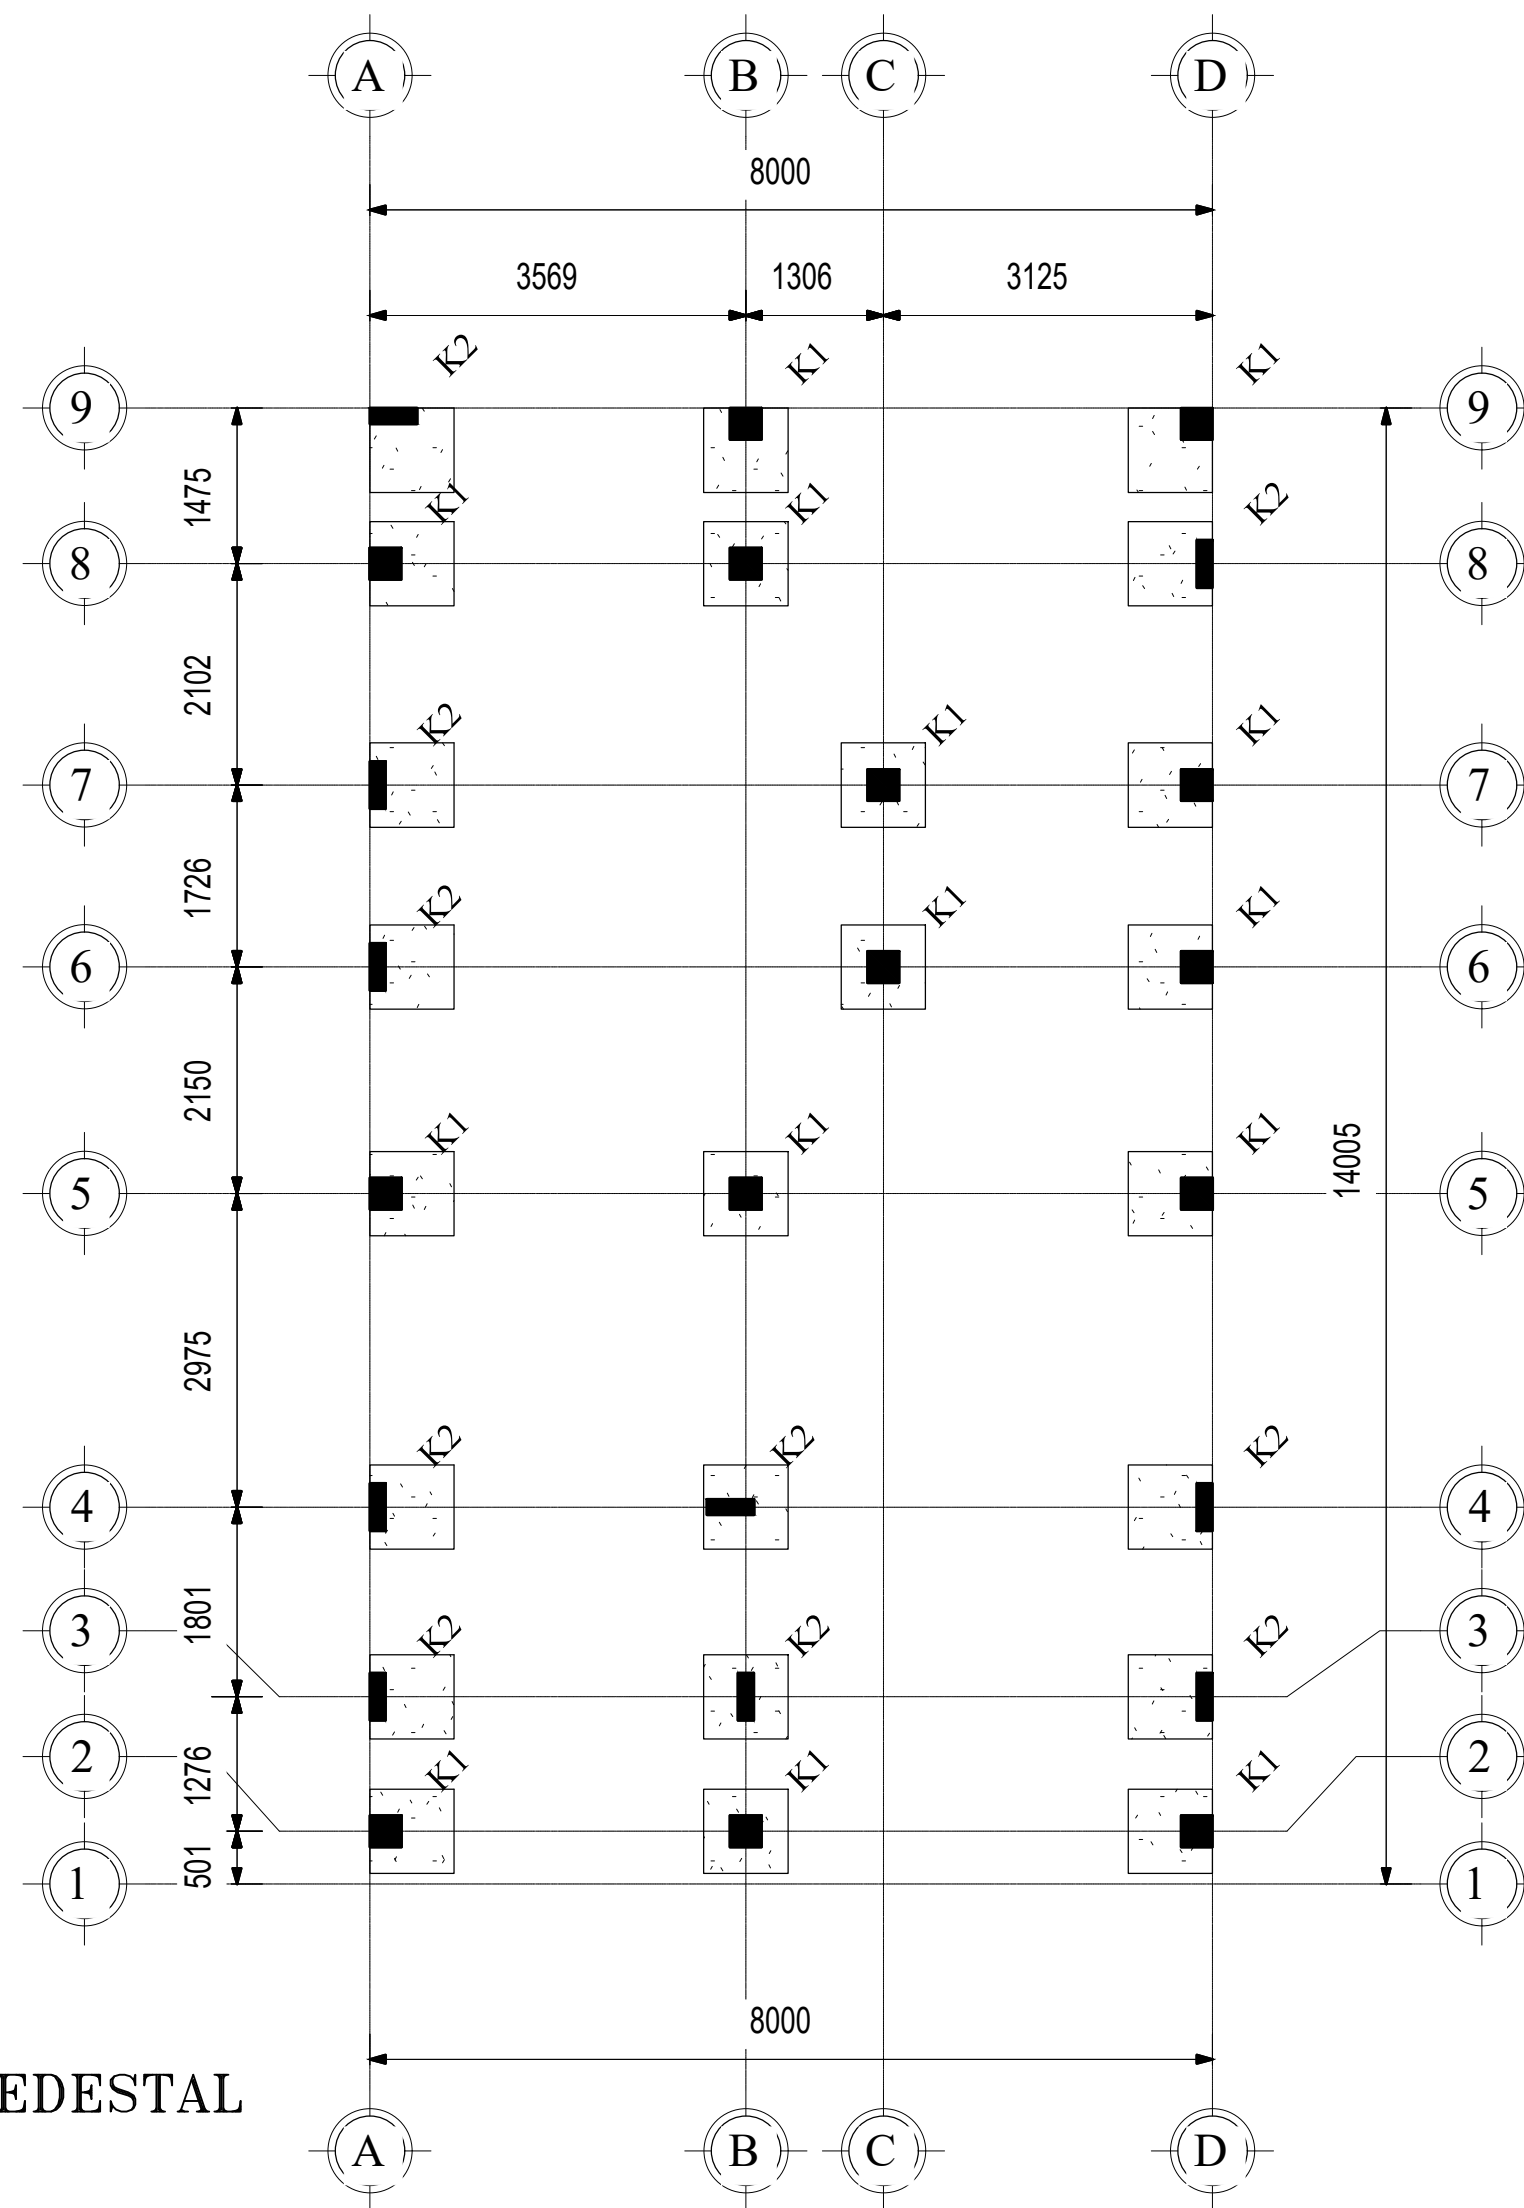
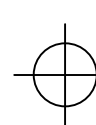
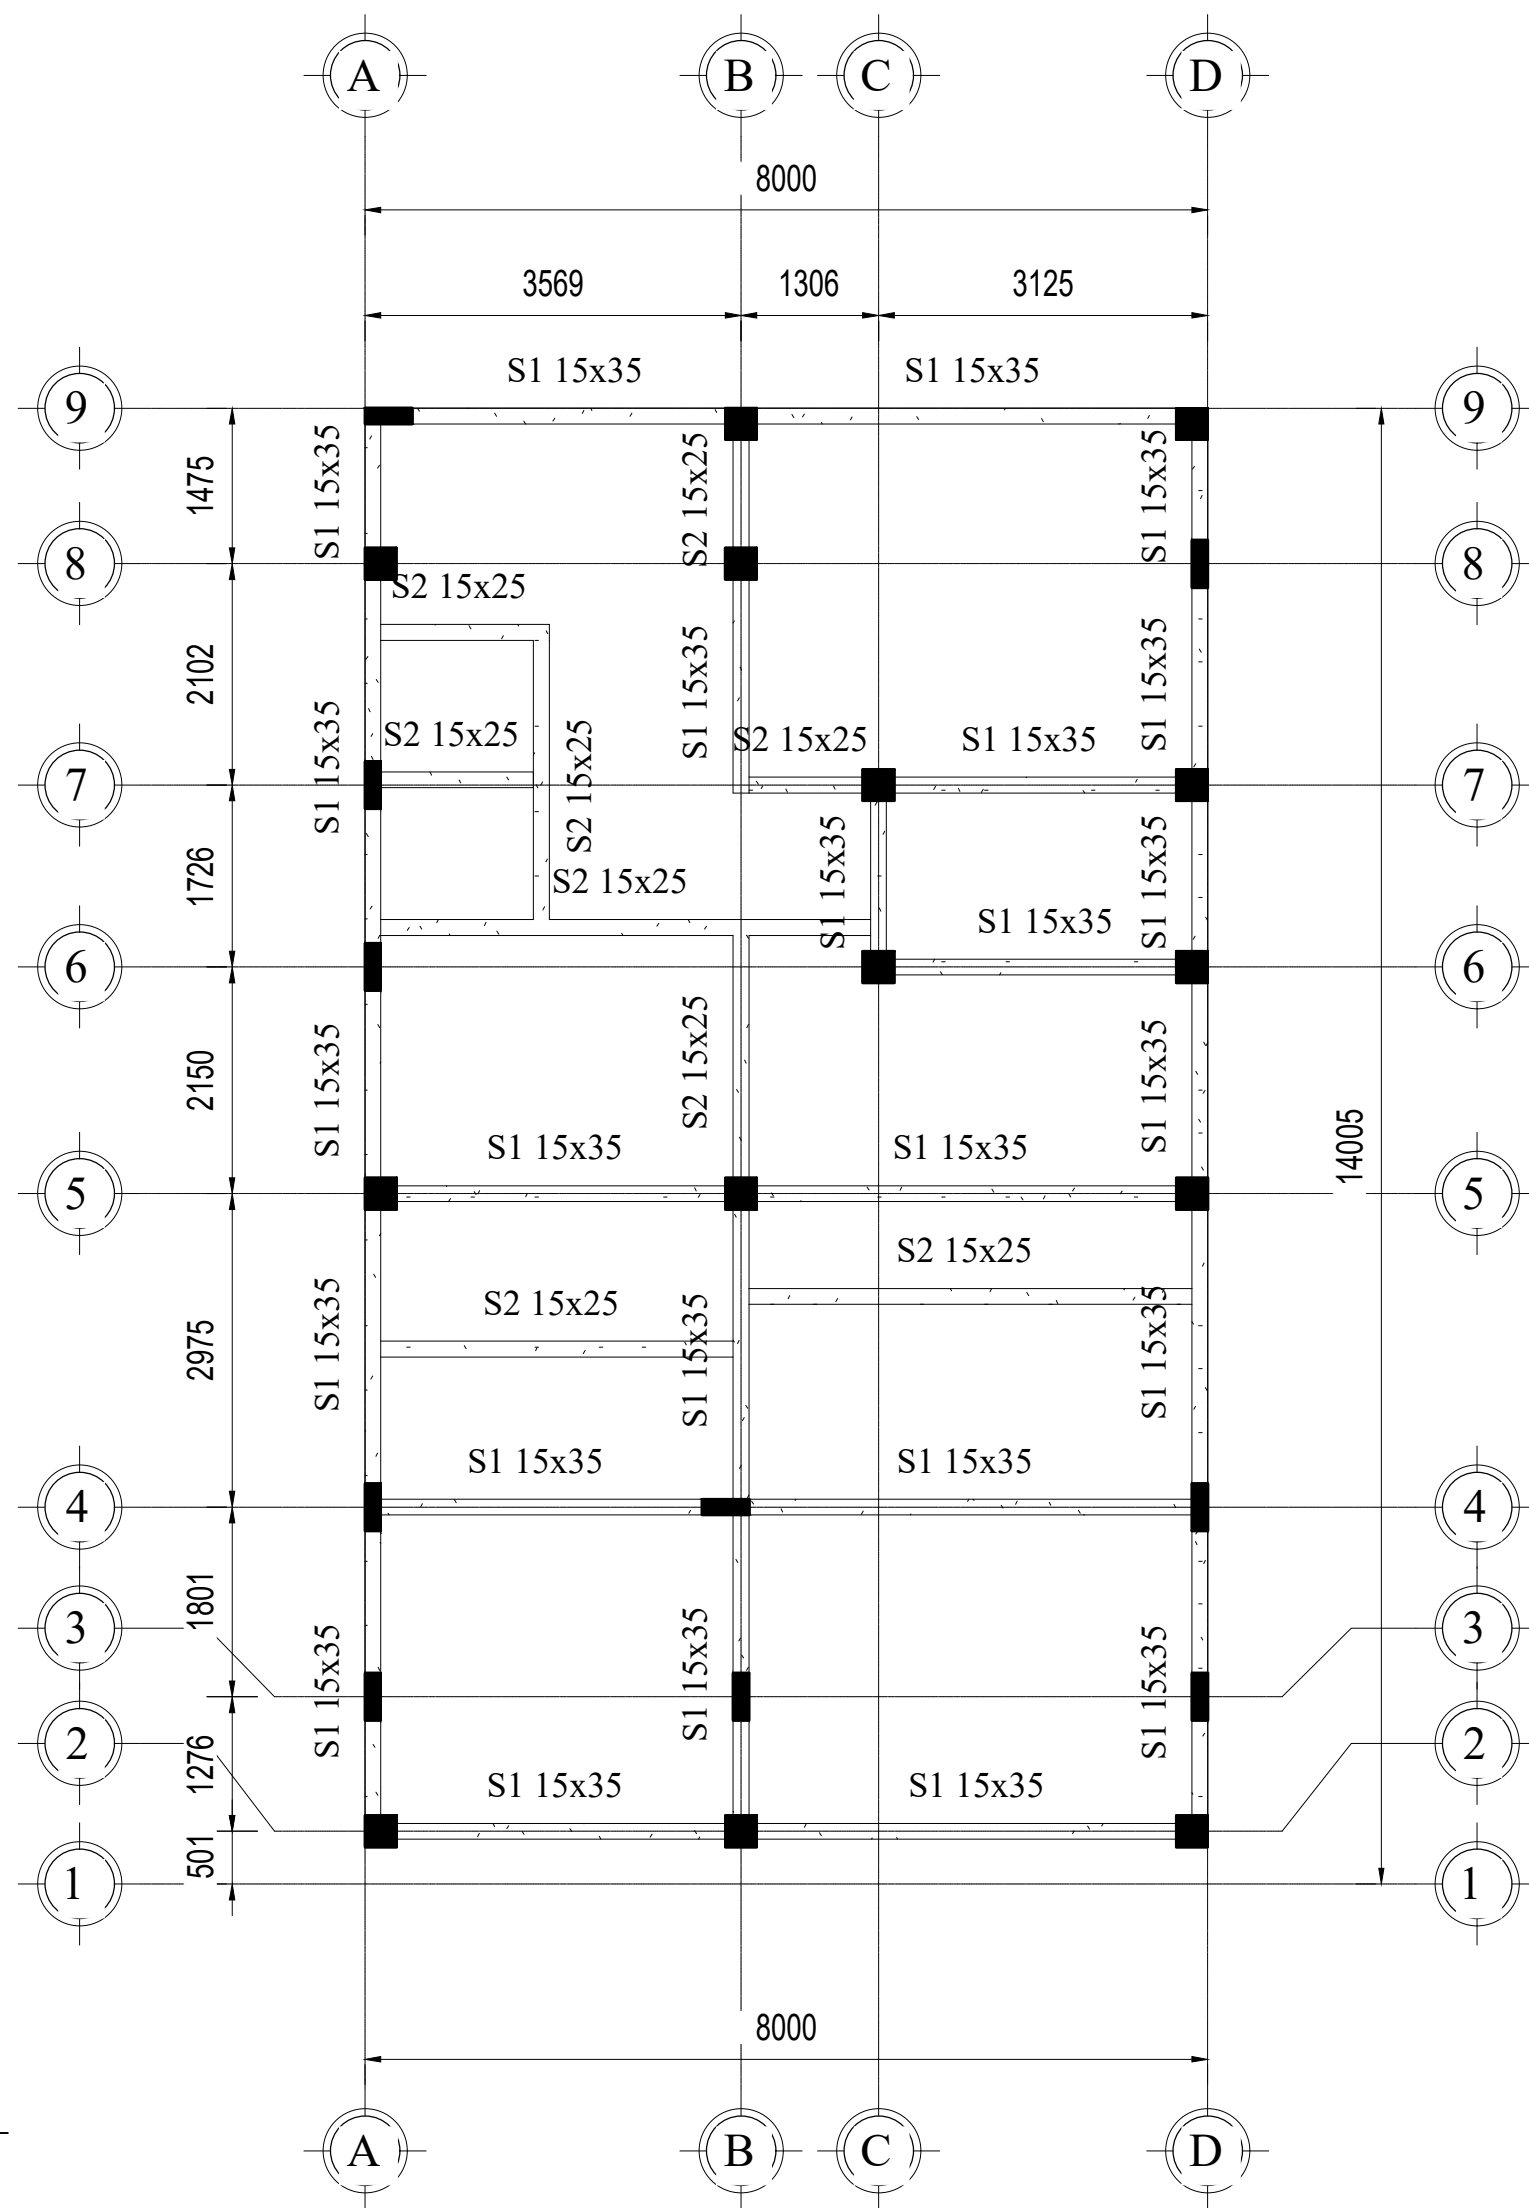




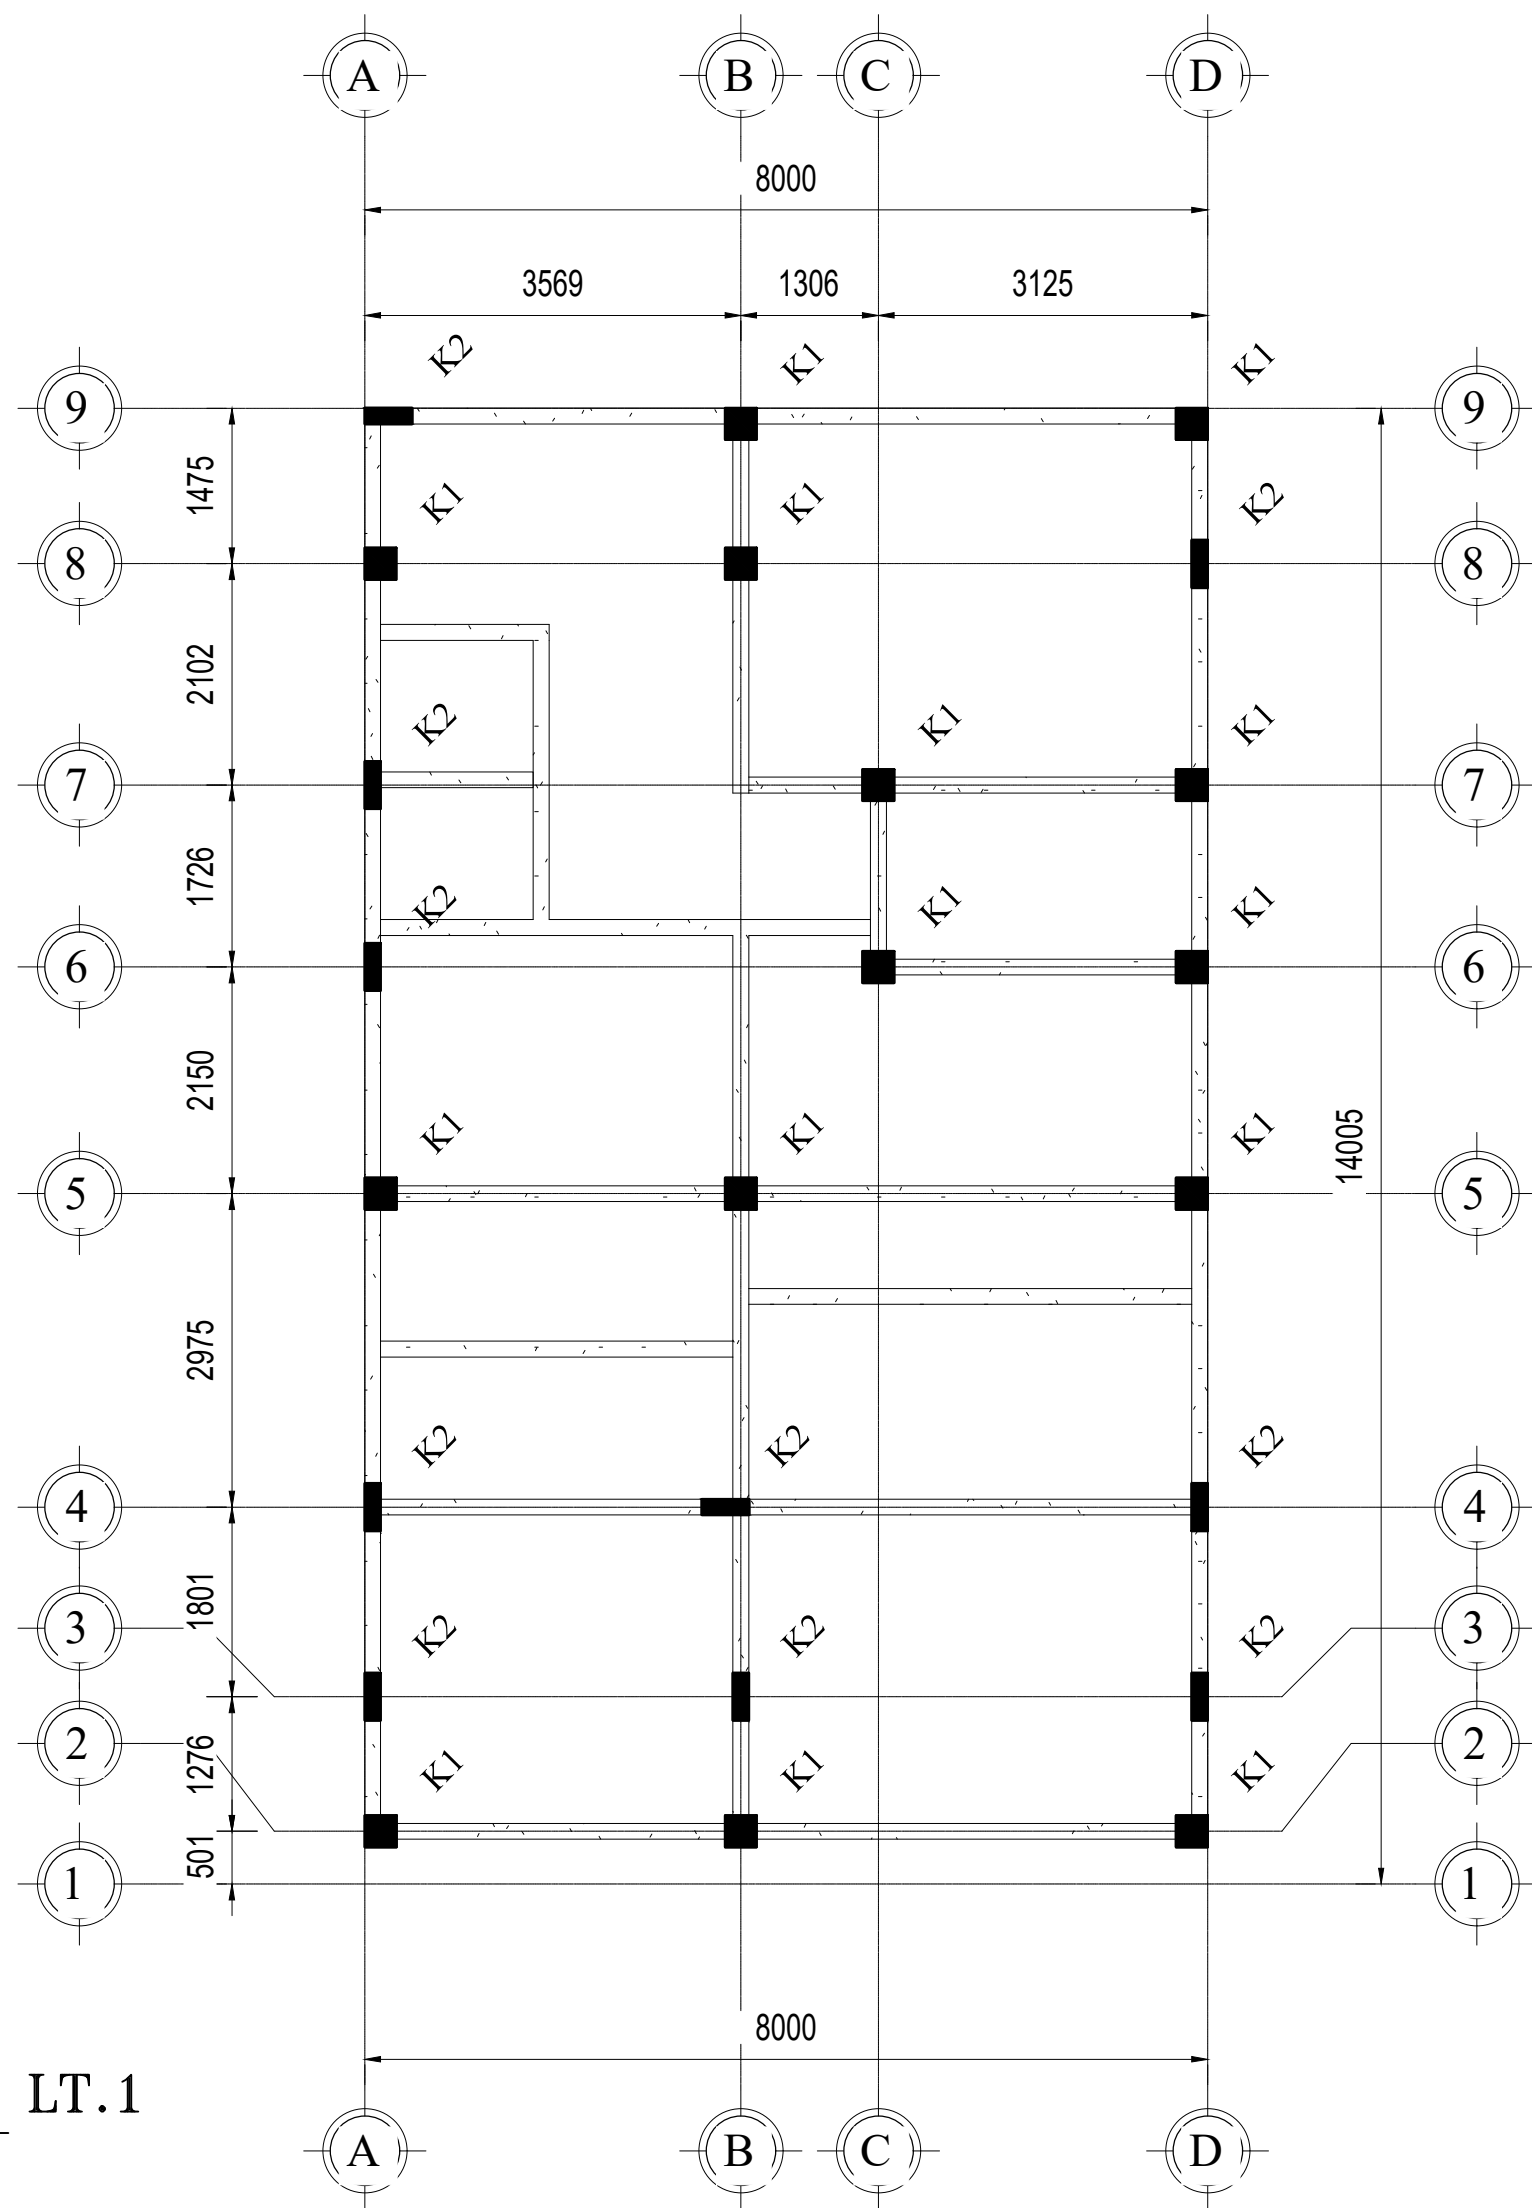
 **DENAH FOOTPLAT**
SKALA 1 : 100

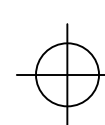


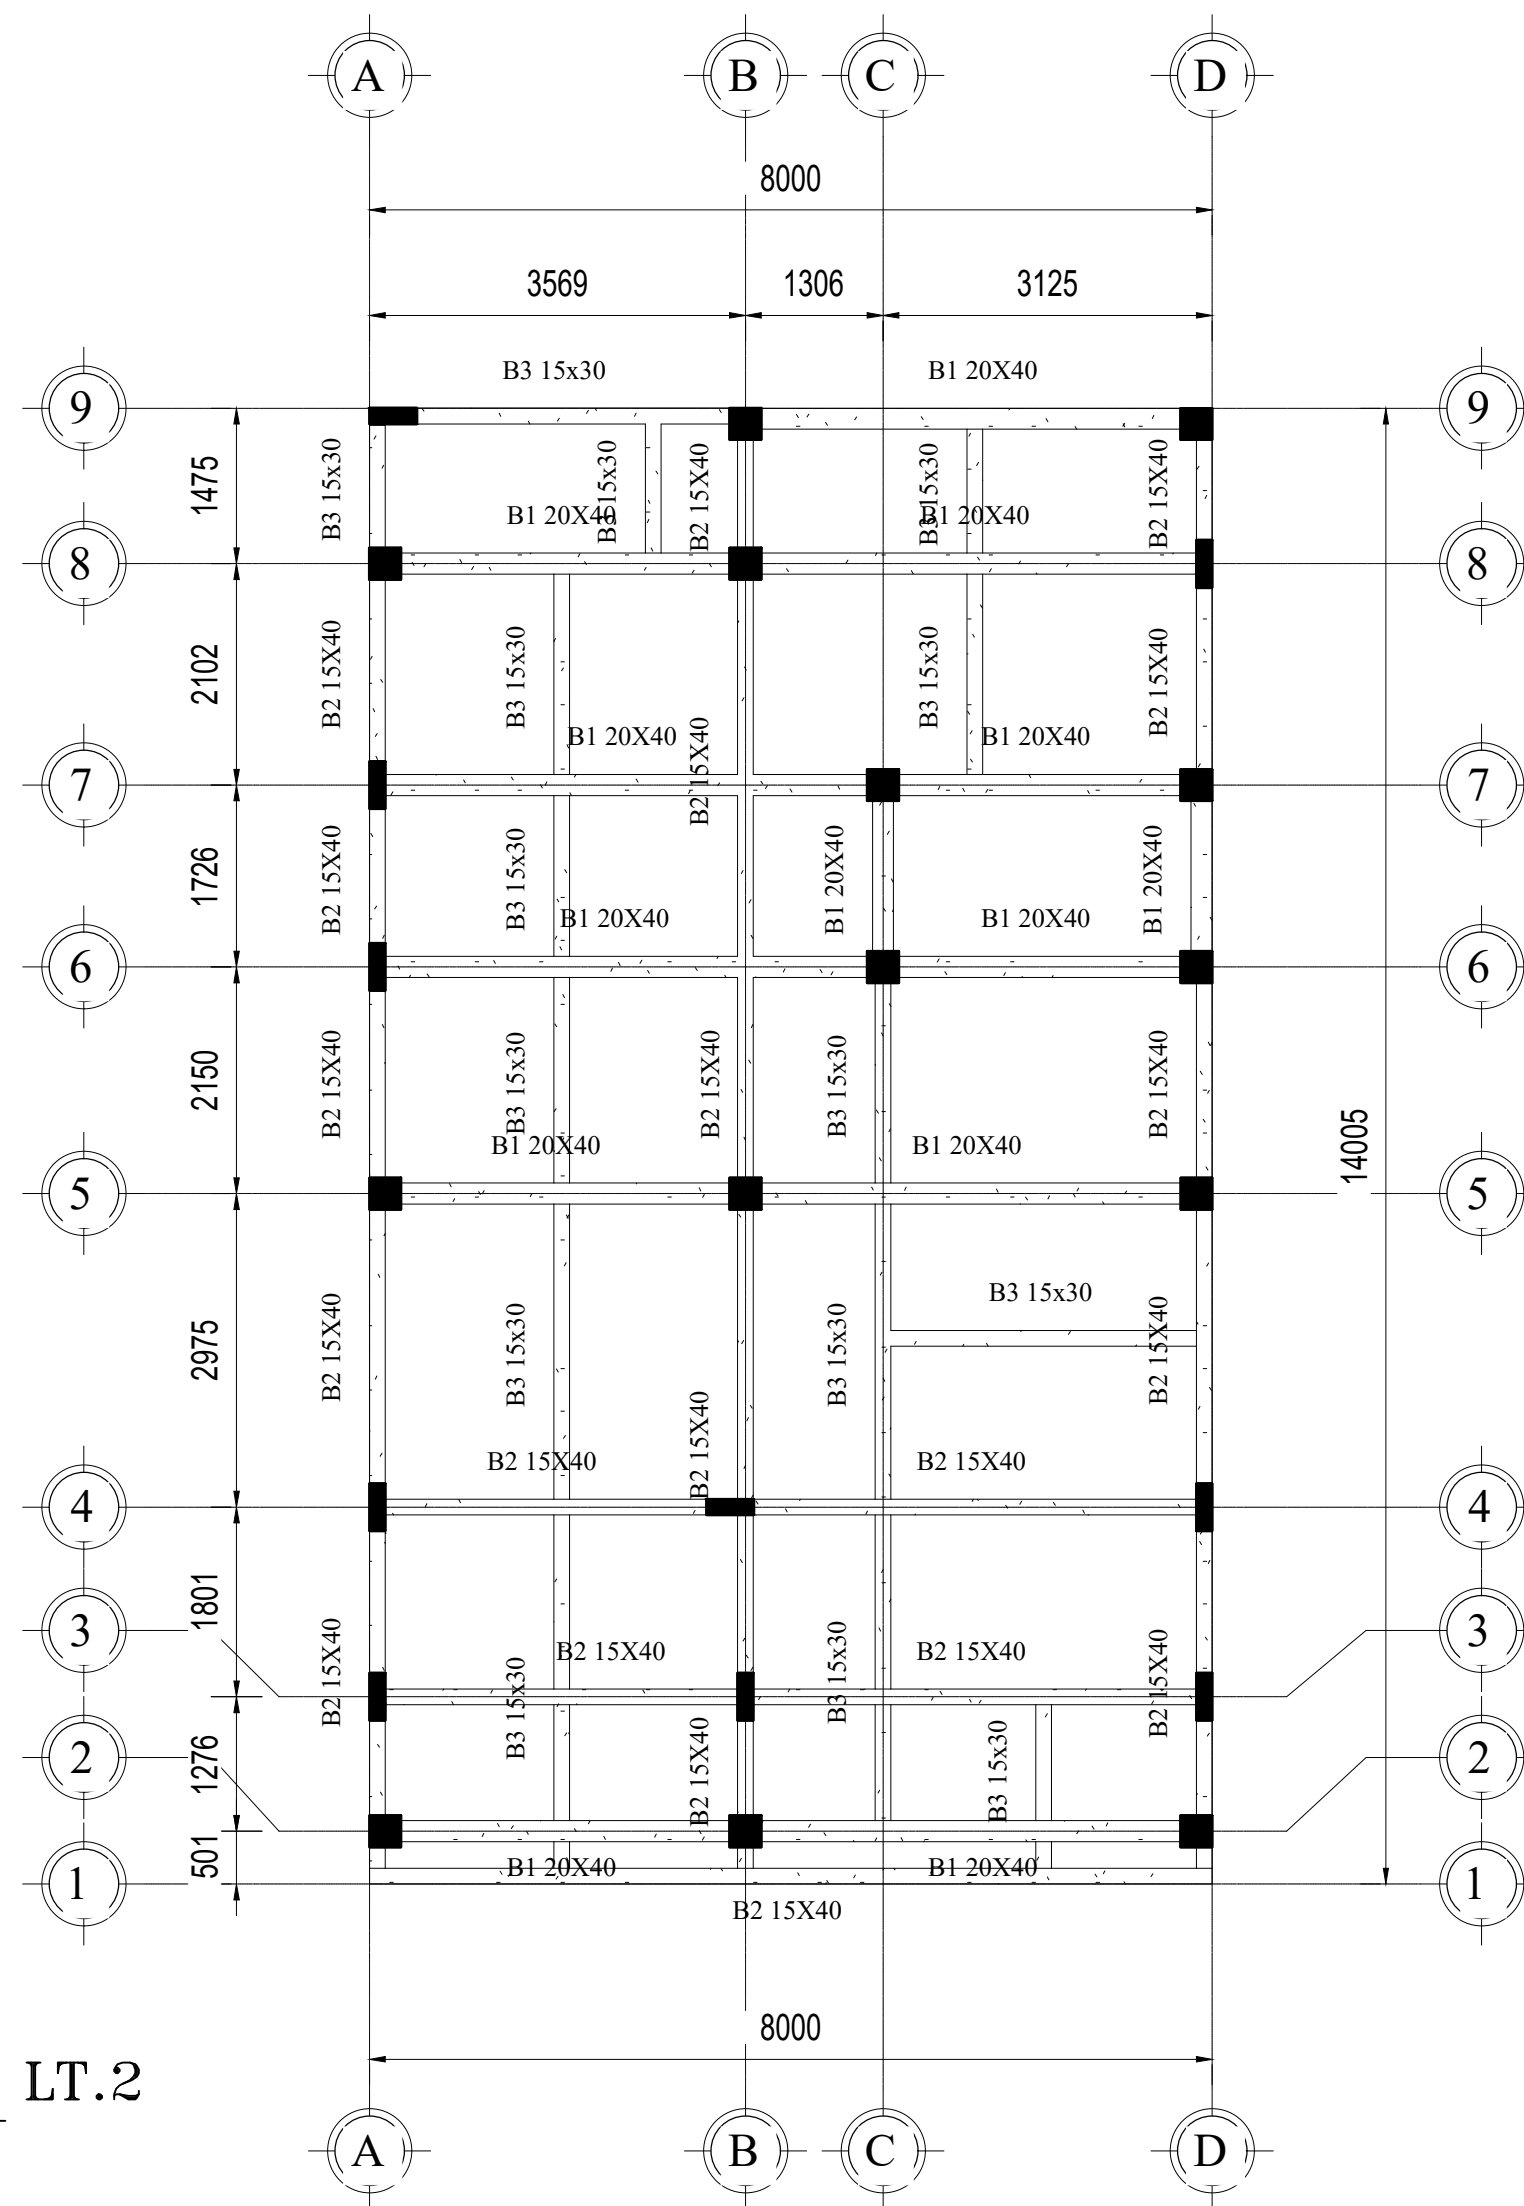
 **DENAH KOLOM PEDESTAL**
SKALA 1 : 100



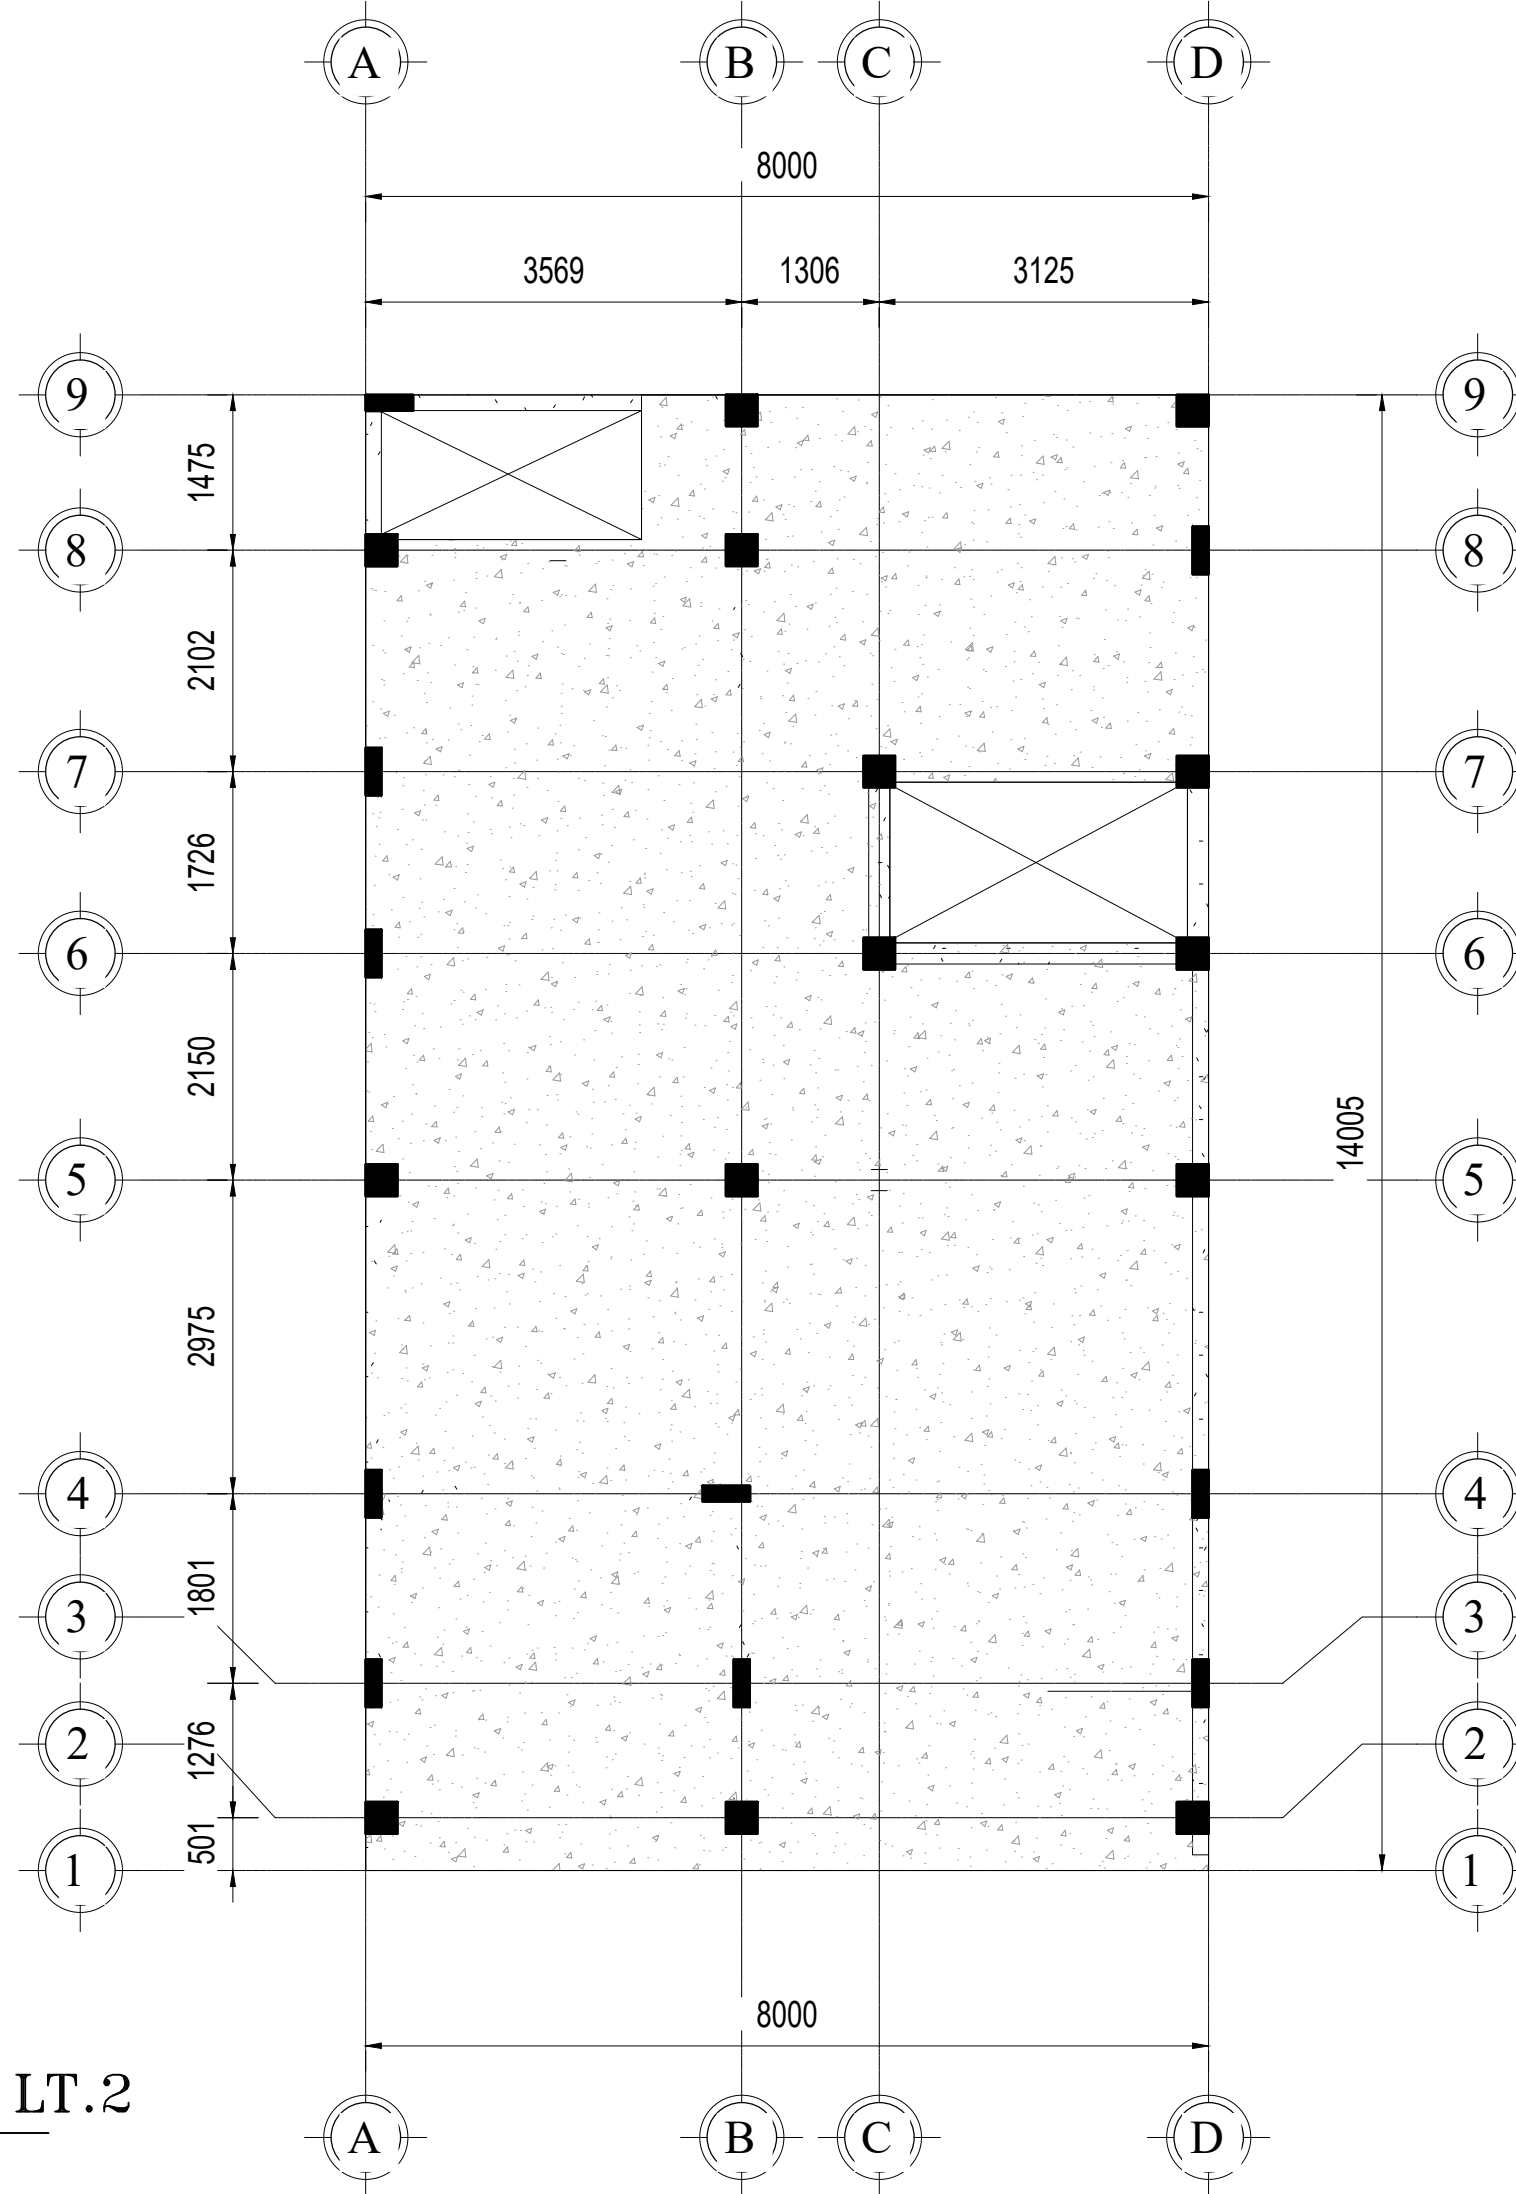
 **DENAH SLOOF**
SKALA 1 : 100

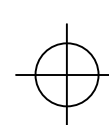


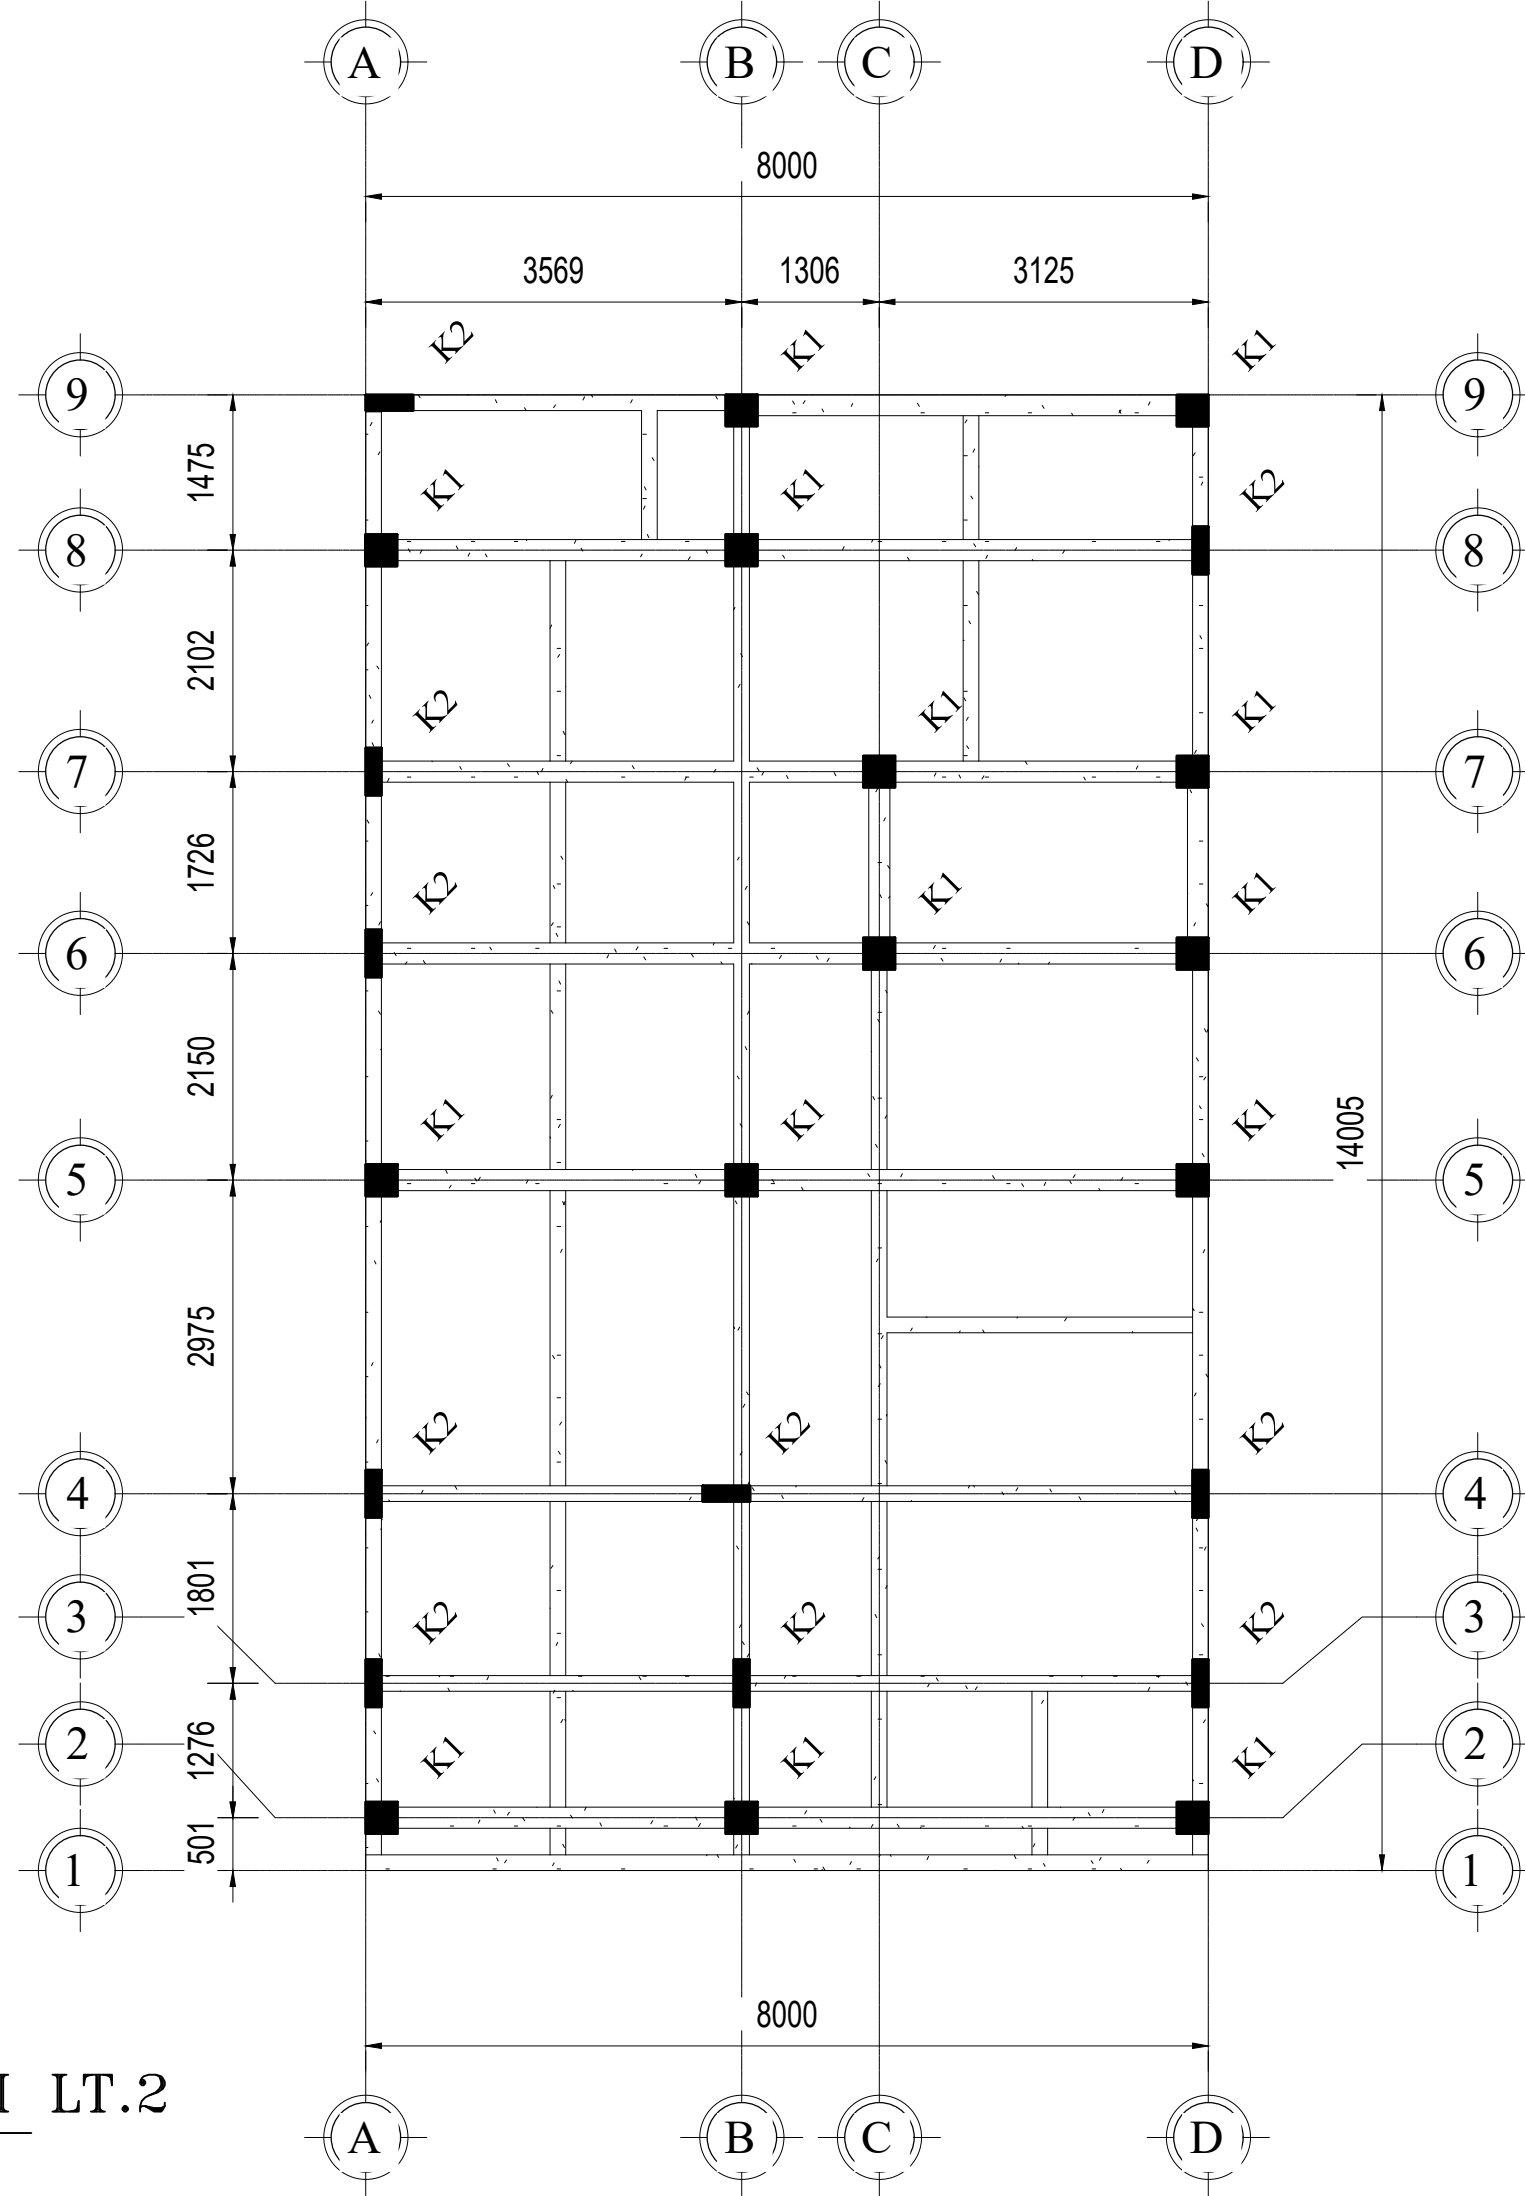
 **DENAH KOLOM LT.1**
SKALA 1 : 100

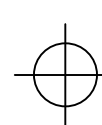


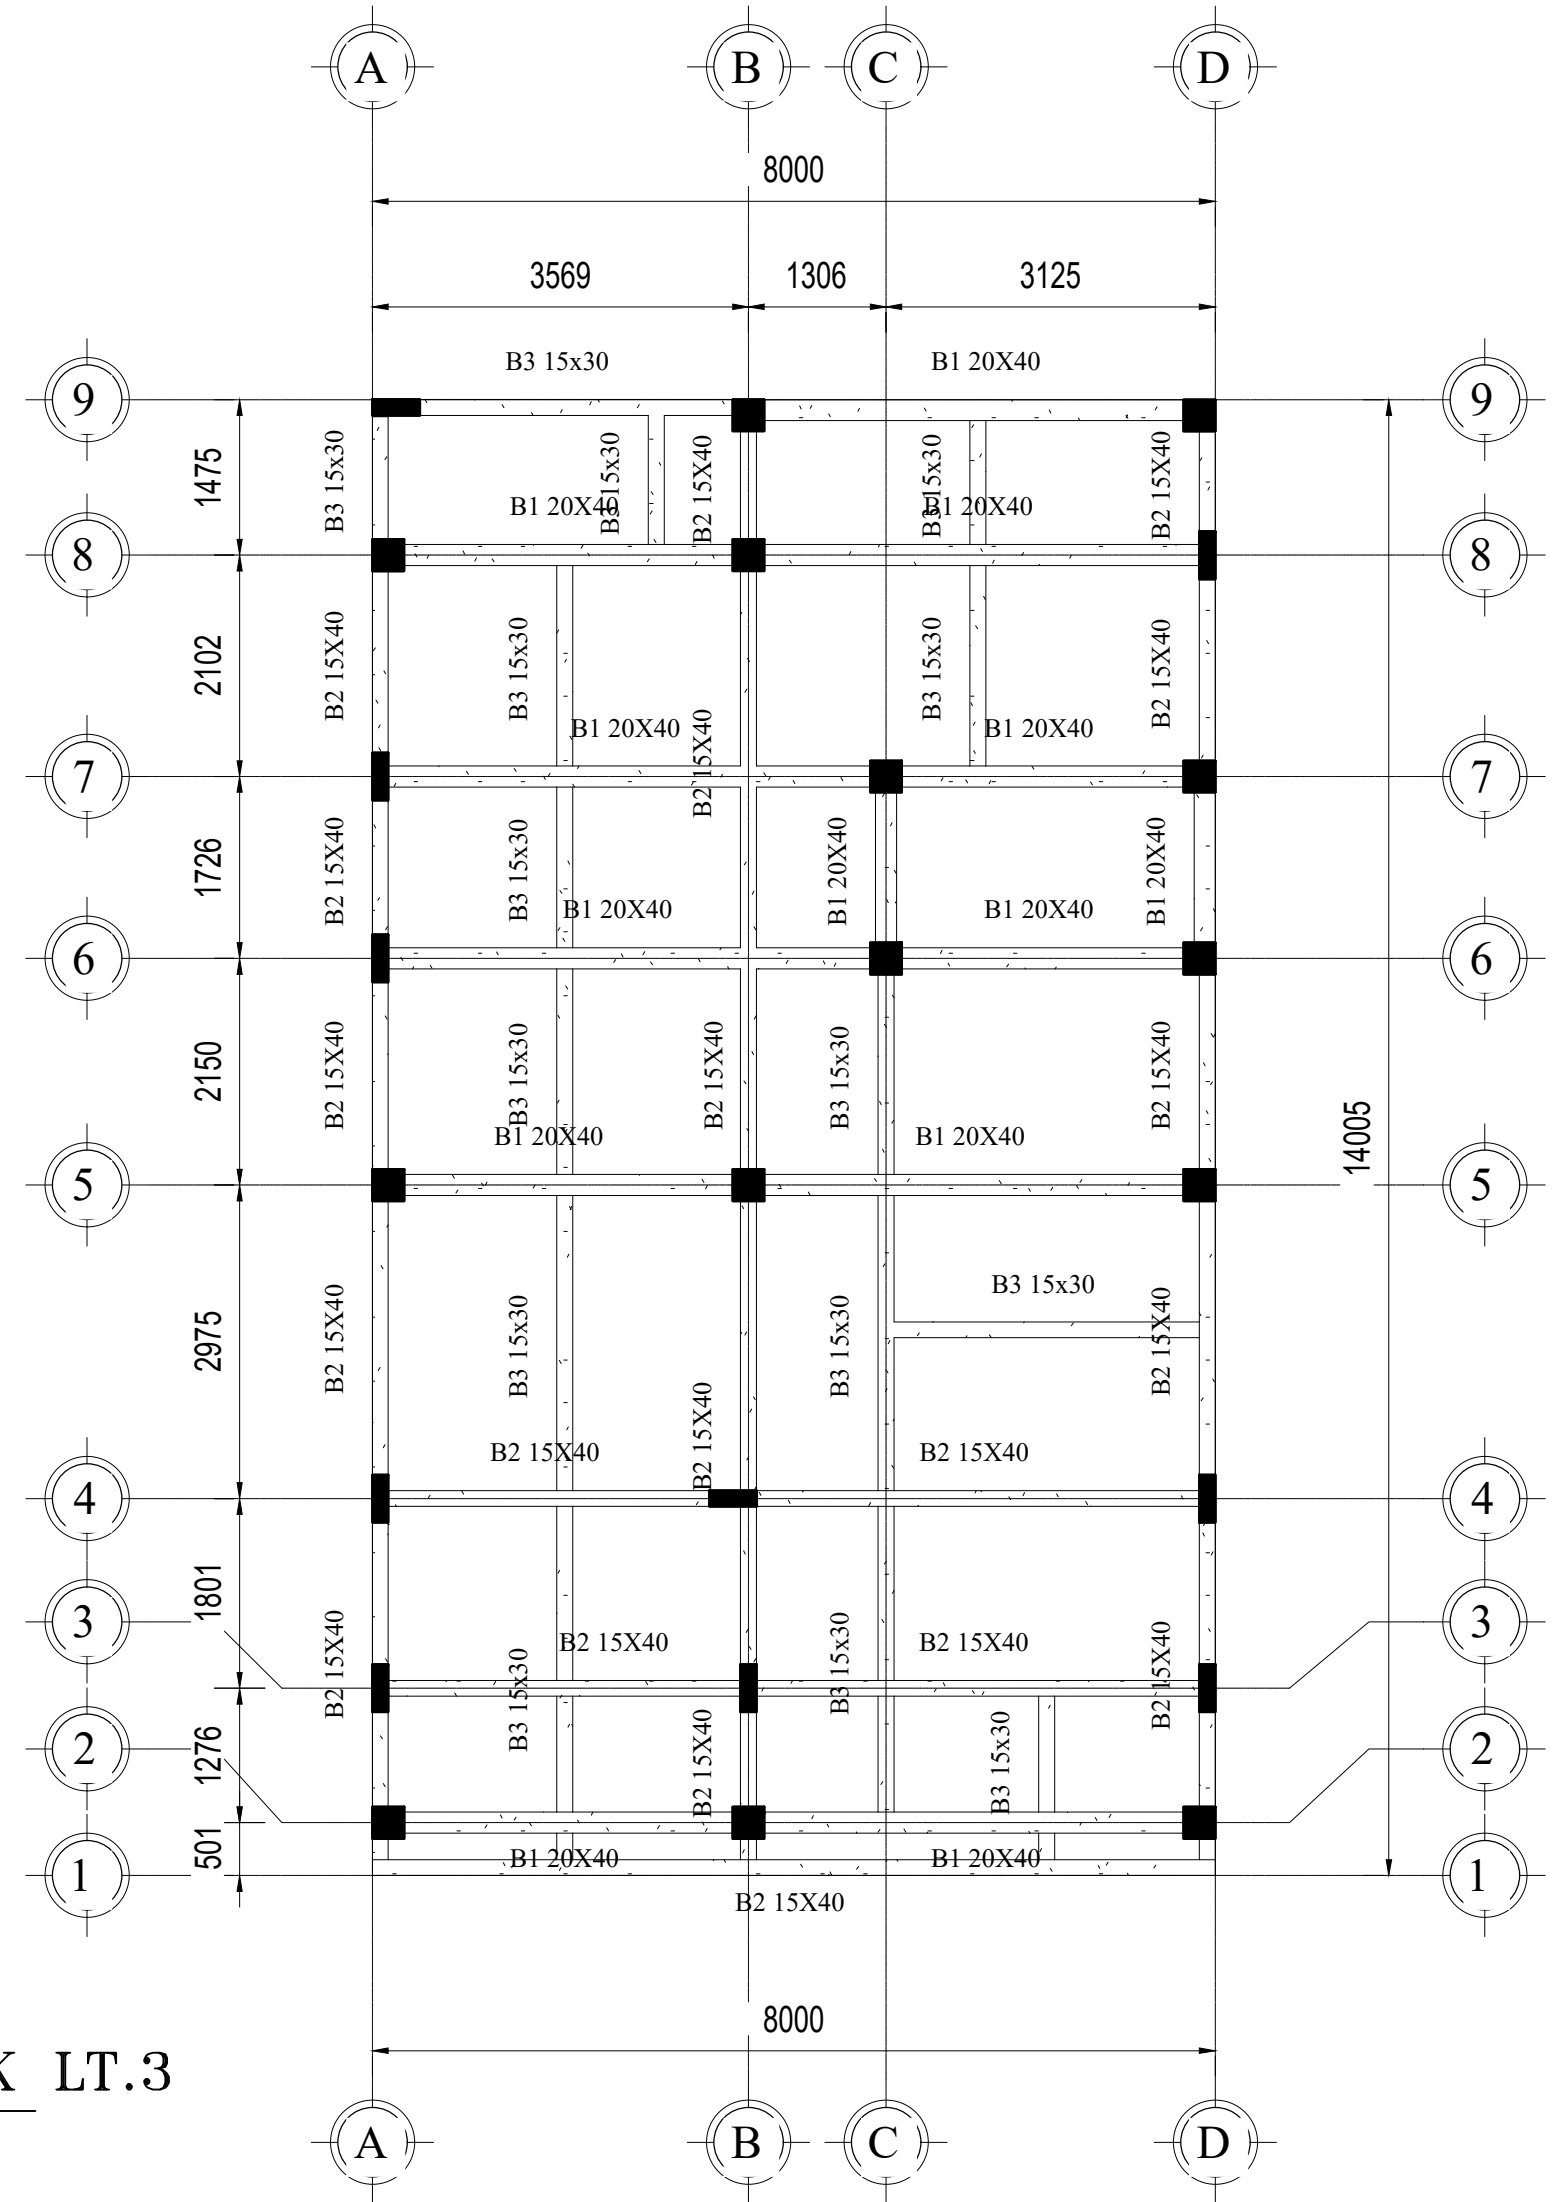
 **DENAH BALOK LT.2**
SKALA 1 : 100

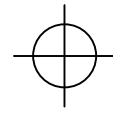


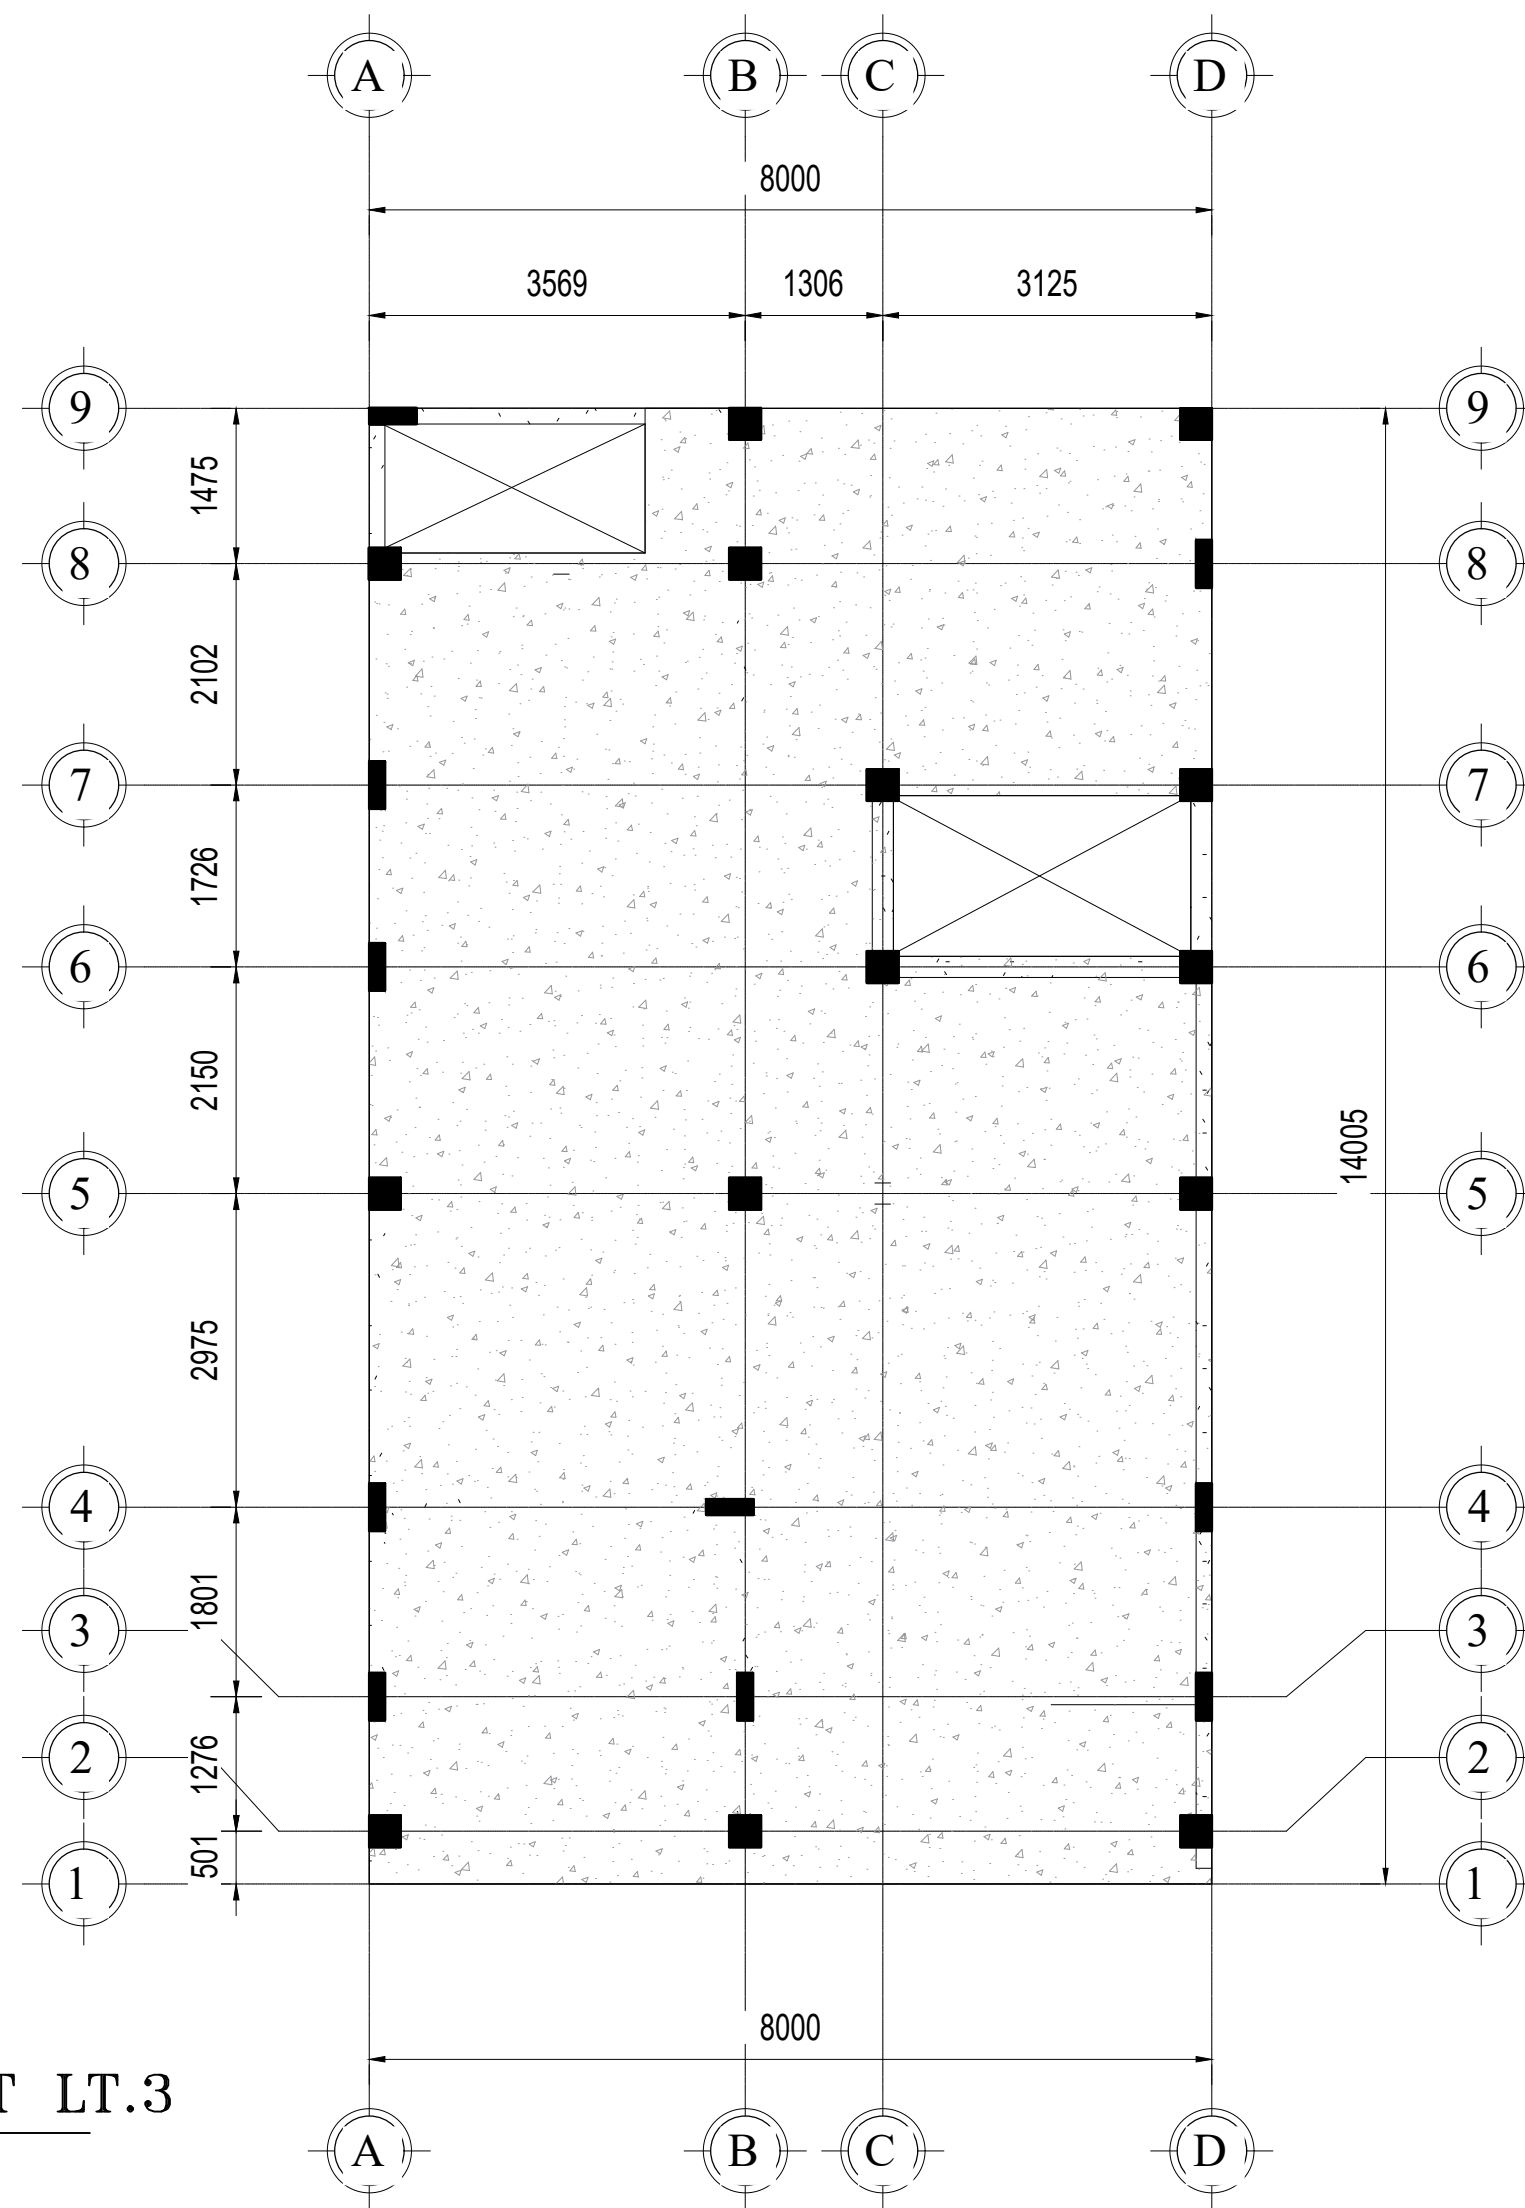
 DENAH PLAT LT.2
SKALA 1 : 100

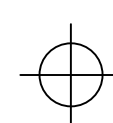


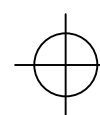
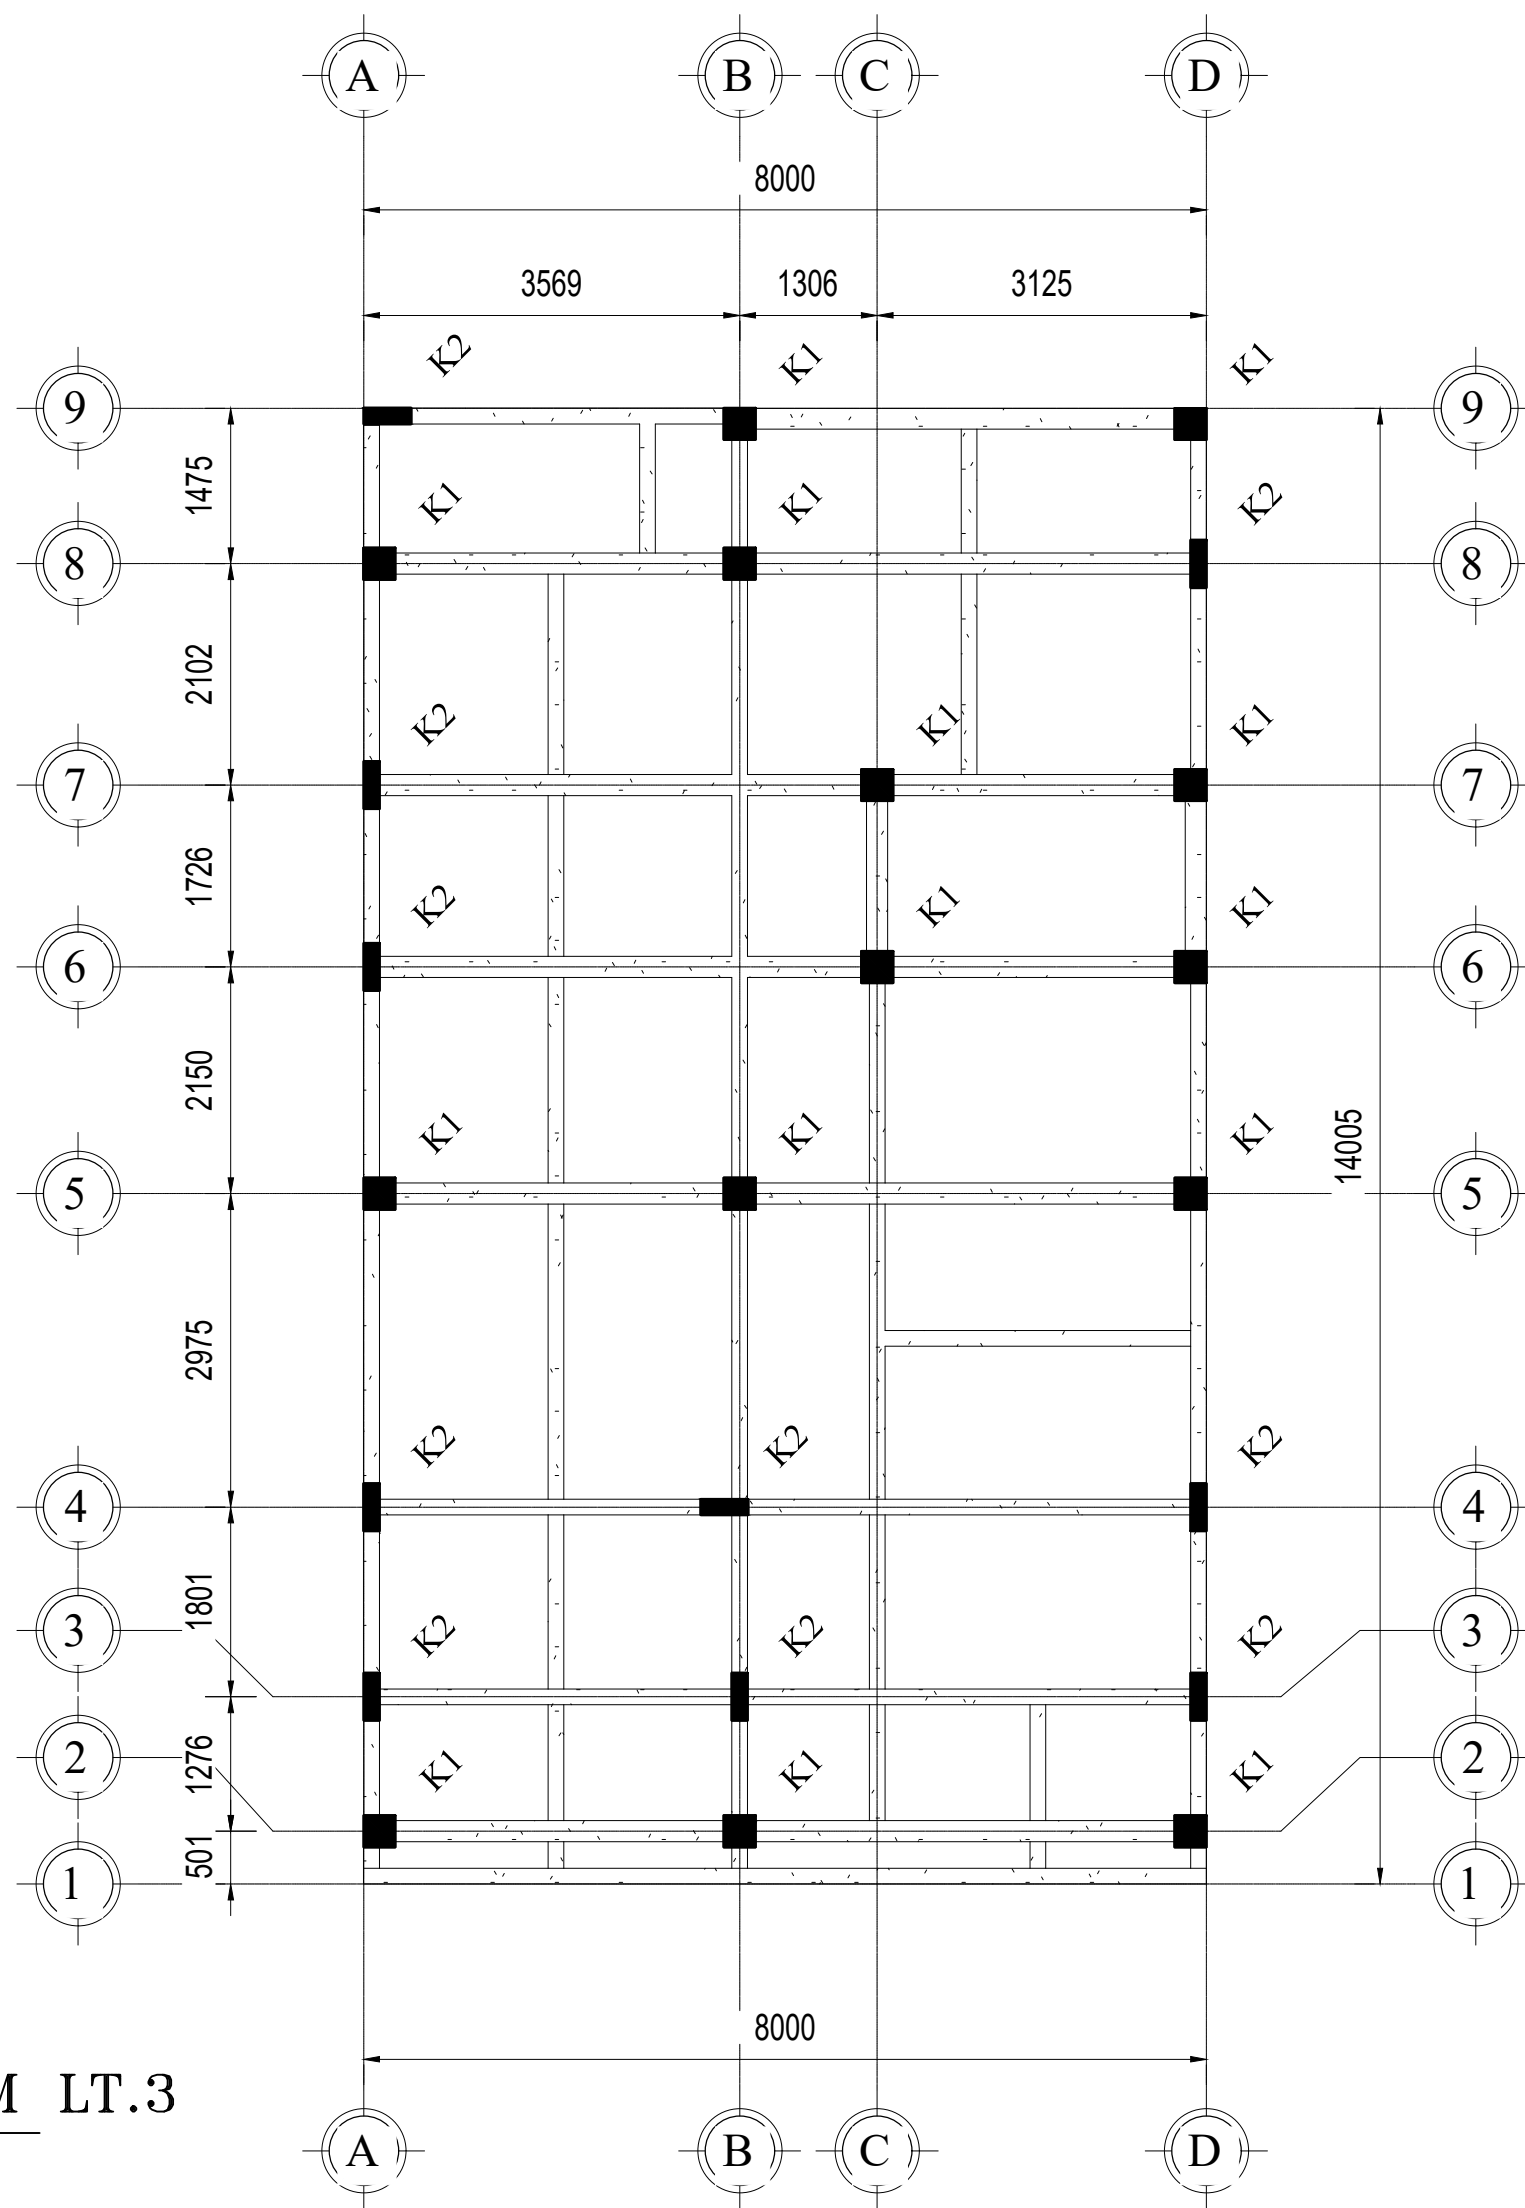
 **DENAH KOLOM LT.2**
SKALA 1 : 100



 **DENAH BALOK LT.3**
SKALA 1 : 100

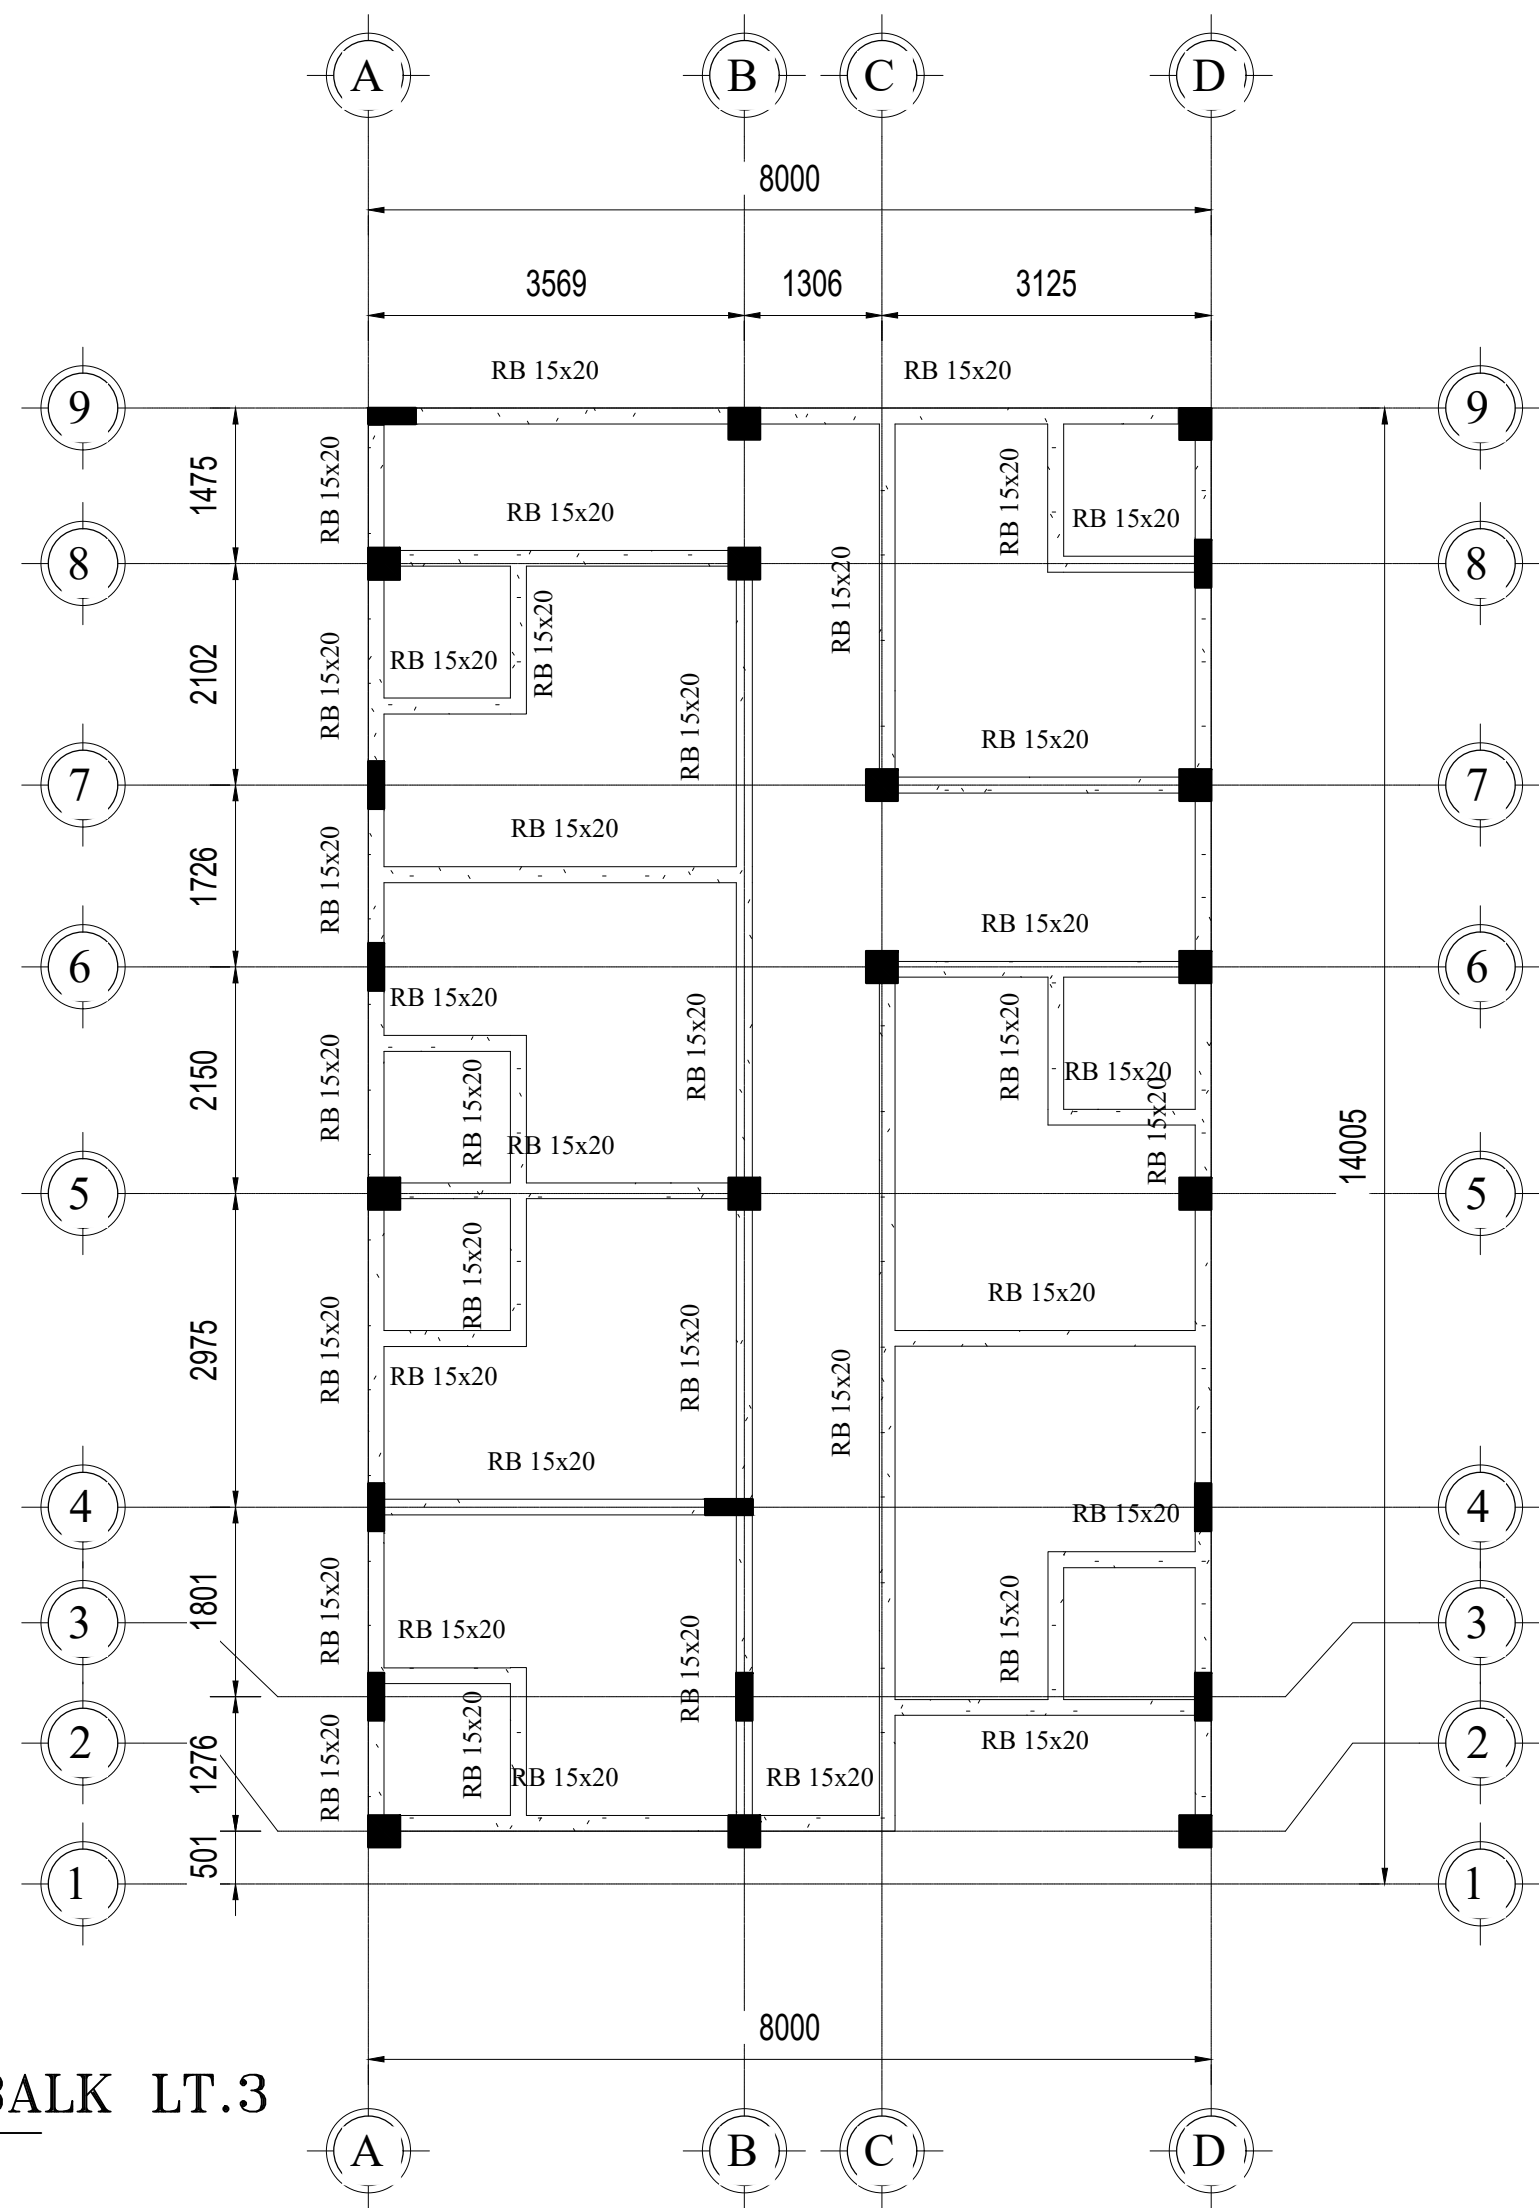


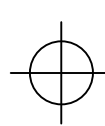
 **DENAH PLAT LT.3**
SKALA 1 : 100

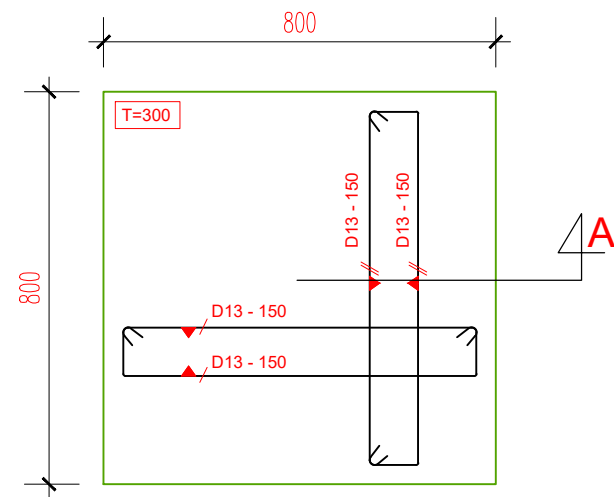


DENAH KOLOM LT.3

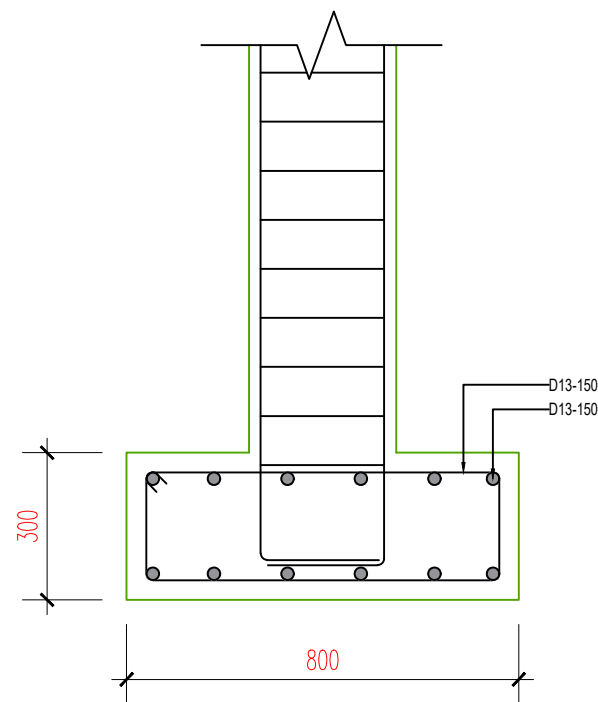
SKALA 1 : 100



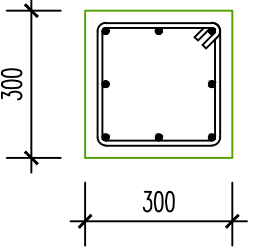
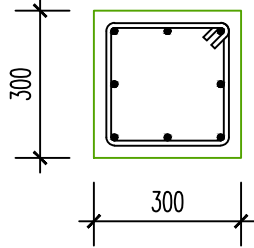
 **DENAH RINGBALK LT.3**
SKALA 1 : 100

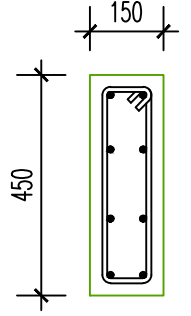
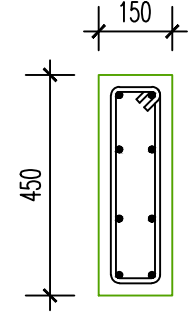


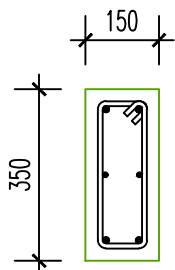
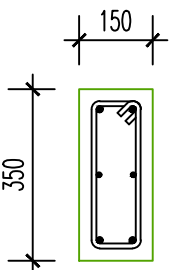
FOOTPLAT FP1

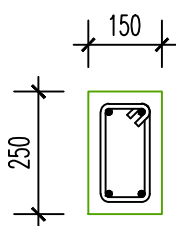
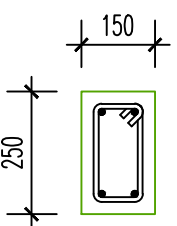


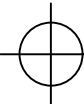
POTONGAN A

TYPE	KOLOM 30X30 - TIPE K1	
POTONGAN		
DIMENSI	30 x 30	30 x 30
TUL. UTAMA	8 D13	8 D13
TUL. SENGKANG	D10 - 100	D10 - 150
POSISI	TUMPUAN	LAPANGAN

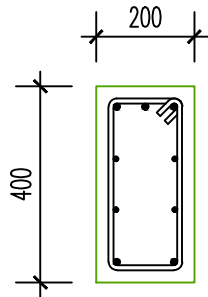
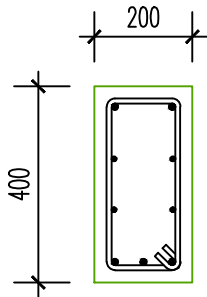
TYPE	KOLOM 15X45 - TIPE K2	
POTONGAN		
DIMENSI	15 x 45	15 x 45
TUL. UTAMA	8 D13	8 D13
TUL. SENGKANG	D10 - 100	D10 - 150
POSISI	TUMPUAN	LAPANGAN

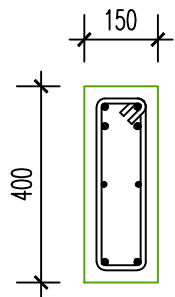
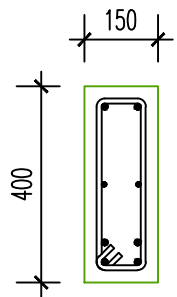
TYPE	SLOOF 15X35 - TIPE S1	
POSISI	TUMPUAN $\frac{1}{4}$ L	LAPANGAN $\frac{1}{2}$ L
POTONGAN		
TUL. ATAS	2 D 13	2 D 13
TUL. BAWAH	2 D 13	2 D 13
SENGKANG	D10 -150	D10 -200
SIDE, TORSI	2 D 10	2 D 10

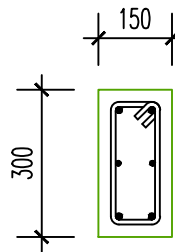
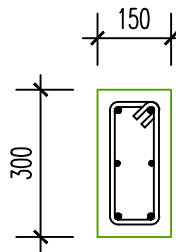
TYPE	SLOOF 15X25 - TIPE S2	
POSISI	TUMPUAN $\frac{1}{4}$ L	LAPANGAN $\frac{1}{2}$ L
POTONGAN		
TUL. ATAS	2 D 13	2 D 13
TUL. BAWAH	2 D 13	2 D 13
SENGKANG	D10 -150	D10 -200
SIDE, TORSI	-	-

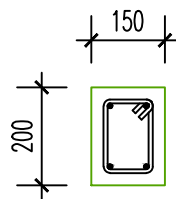
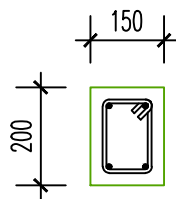


DETAIL STRUKTUR SLOOF

TYPE	BALOK 20X40 - TIPE B1	
POSISI	TUMPUAN $\frac{1}{4}$ L	LAPANGAN $\frac{1}{2}$ L
POTONGAN		
TUL. ATAS	3 D 13	2 D 13
TUL. BAWAH	2 D 13	3 D 13
SENGKANG	D10 -100	D10 -150
SIDE, TORSI	4 D 10	4 D 10

TYPE	BALOK 15X40 - TIPE B2	
POSISI	TUMPUAN $\frac{1}{4}$ L	LAPANGAN $\frac{1}{2}$ L
POTONGAN		
TUL. ATAS	4 D 13	2 D 13
TUL. BAWAH	2 D 13	4D 13
SENGKANG	D10 -100	D10 -150
SIDE, TORSI	2 D 10	2 D 10

TYPE	BALOK 15X30 - TIPE B3	
POSISI	TUMPUAN $\frac{1}{4}$ L	LAPANGAN $\frac{1}{2}$ L
POTONGAN		
TUL. ATAS	2 D 13	2 D 13
TUL. BAWAH	2 D 13	2 D 13
SENGKANG	D10 -100	D10 -150
SIDE, TORSI	2 D 10	2 D 10

TYPE	RINGBALK 15X20 - TIPE RB	
POSISI	TUMPUAN $\frac{1}{4}$ L	LAPANGAN $\frac{1}{2}$ L
POTONGAN		
TUL. ATAS	2 D 10	2 D 10
TUL. BAWAH	2 D 10	2 D 10
SENGKANG	Ø8 -150	Ø8 -150
SIDE, TORSI	-	-