

GAMBAR RENCANA

PERENCANAAN HUNIAN RUMAH TYPE 40

BAPAK MULYONO, SLEMAN, YOGYAKARTA




DAFTAR GAMBAR

PERENCANAAN HUNIAN RUMAH TYPE 40

NO	JUDUL GAMBAR	SKALA
01	DENAH SITUASI	1 : 150
02	DENAH RENCANA	1 : 100
03	DENAH ATAP	1 : 100
04	POTONGAN A-A	1 : 100
05	POTONGAN B-B	1 : 100
06	POTONGAN C-C	1 : 100
07	TAMPAK DEPAN	1 : 100
08	TAMPAK SAMPING KANAN	1 : 100
09	TAMPAK SAMPING KIRI	1 : 100
10	TAMPAK BELAKANG	1 : 100
11	DENAH PONDASI	1 : 100
12	DETAIL PONDASI A-A	1 : 20
13	DETAIL PONDASI B-B	1 : 20
14	DENAH SLOOF	1 : 100
15	DETAIL SLOOF	1 : 20
16	DENAH KOLOM	1 : 100
17	DENAH BALOK LATEI	1 : 100
18	DENAH RING BALOK	1 : 100
19	DETAIL KOLOM & BALOK	1 : 20
20	DENAH PINTU DAN JENDELA	1 : 100

NO	JUDUL GAMBAR	SKALA
21	DETAIL PJ	1 : 25
22	DETAIL P1	1 : 25
23	DETAIL P2	1 : 25
24	DETAIL P3	1 : 25
25	DETAIL J1	1 : 25
26	DETAIL J2	1 : 25
27	DETAIL BV	1 : 25
28	DENAH FINISHING LANTAI	1 : 100
29	DENAH PLAFOND	1 : 100
30	DENAH INSTALASI LISTRIK	1 : 100
31	DENAH INSTALASI AIR BERSIH	1 : 100
32	DENAH INSTALASI AIR KOTOR	1 : 100
33	DENAH INSTALASI AIR HUJAN	1 : 100
34	DETAIL SEPTICTANK	1 : 50
35	DETAIL SUMUR PERESAPAN	1 : 20
36	DETAIL BAK KONTROL	1 : 20
37	DETAIL ROOF DRAIN	1 : 20

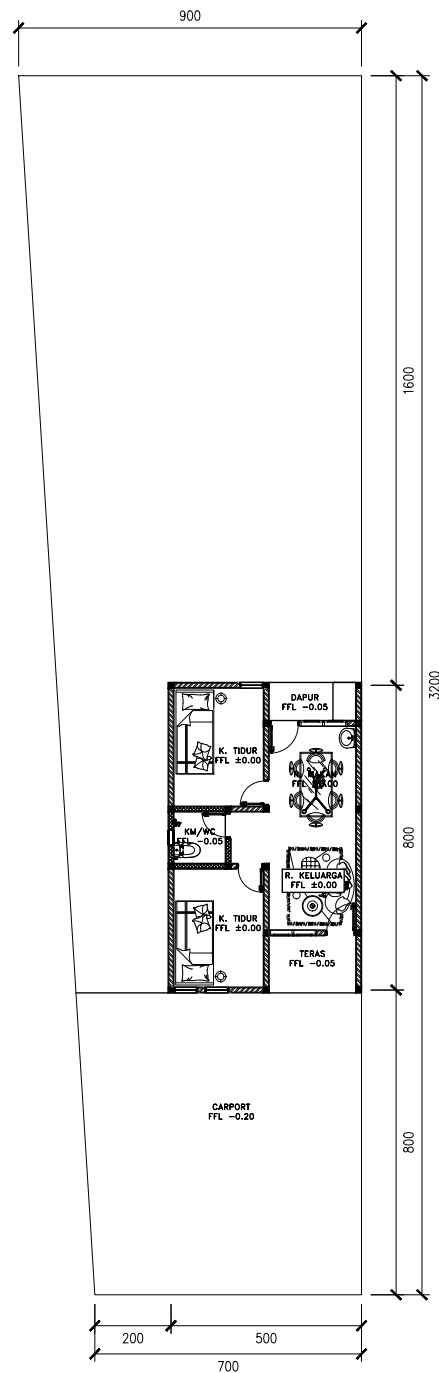


SITEPLAN RENCANA
 SKALA 1:150



CATATAN

NAMA PROYEK

RUMAH TINGGAL
TYPE 40 BAPAK MULYONO

LOKASI

Balong, Cangkringan,
sleman, Yogyakarta

DIGAMBAR

BAGAS PRATAMA A.
DRAFTER

DIPERIKSA OLEH

HARYO BUWONO, SH.
KONTRAKTOR

DISETUJUI OLEH

BAPAK MULYONO
OWNER

JUDUL GAMBAR

SITEPLAN RENCANA

SKALA

1:200

NO. LEMBAR

ARS-1

REVISI NOMER

TANGGAL

10/07/2026

CATATAN

NAMA PROYEK

RUMAH TINGGAL
TYPE 40 BAPAK MULYONO

LOKASI

Balong, Cangkringan,
sleman, Yogyakarta

DIGAMBAR

BAGAS PRATAMA A.
DRAFTER

DIPERIKSA OLEH

HARYO BUWONO, SH.
KONTRAKTOR

DISETUJUI OLEH

BAPAK MULYONO
OWNER

JUDUL GAMBAR

DENAH RENCANA

SKALA

NO. LEMBAR


1:100

ARS-2

REVISI NOMER


TANGGAL

10/07/2026

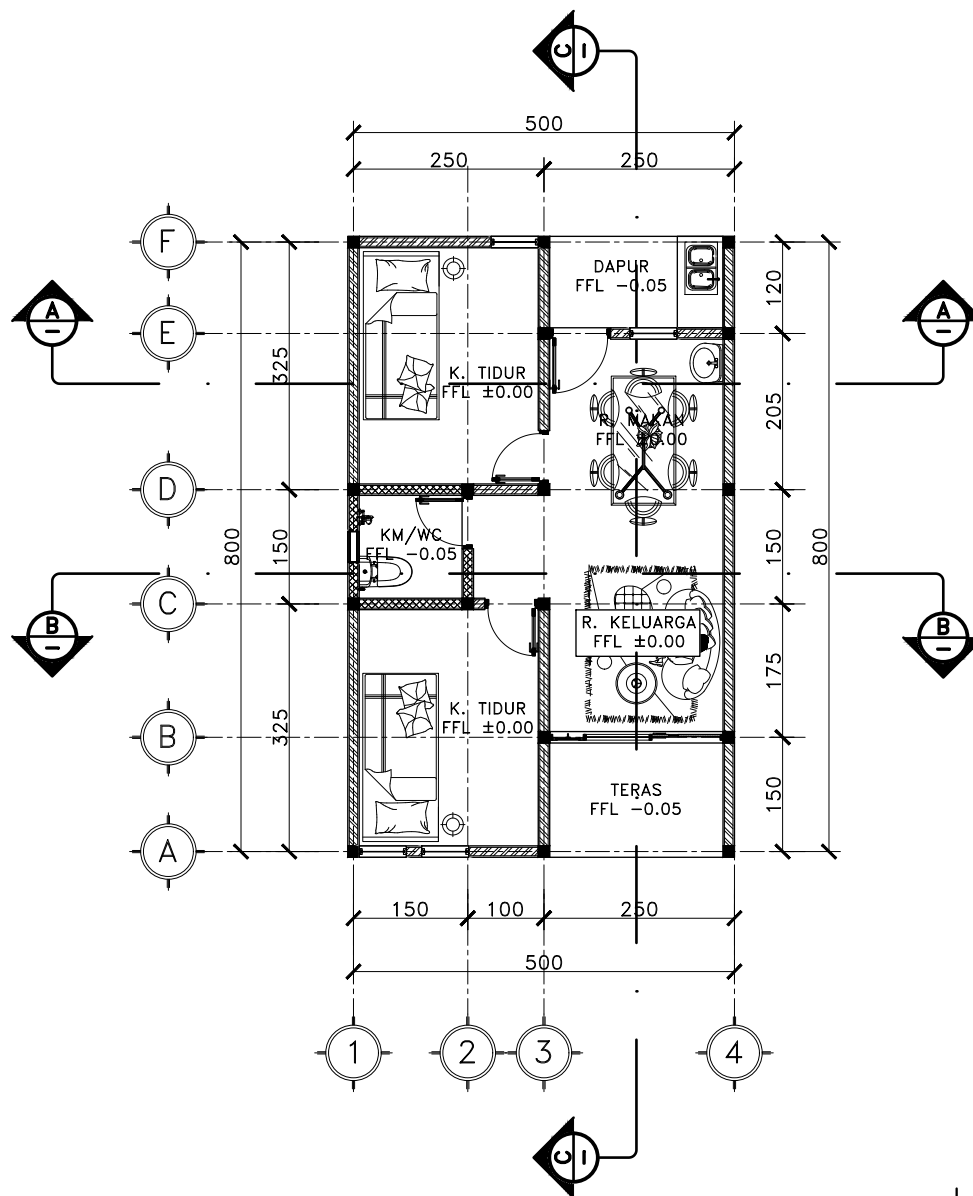

DENAH RENCANA

SKALA 1:100

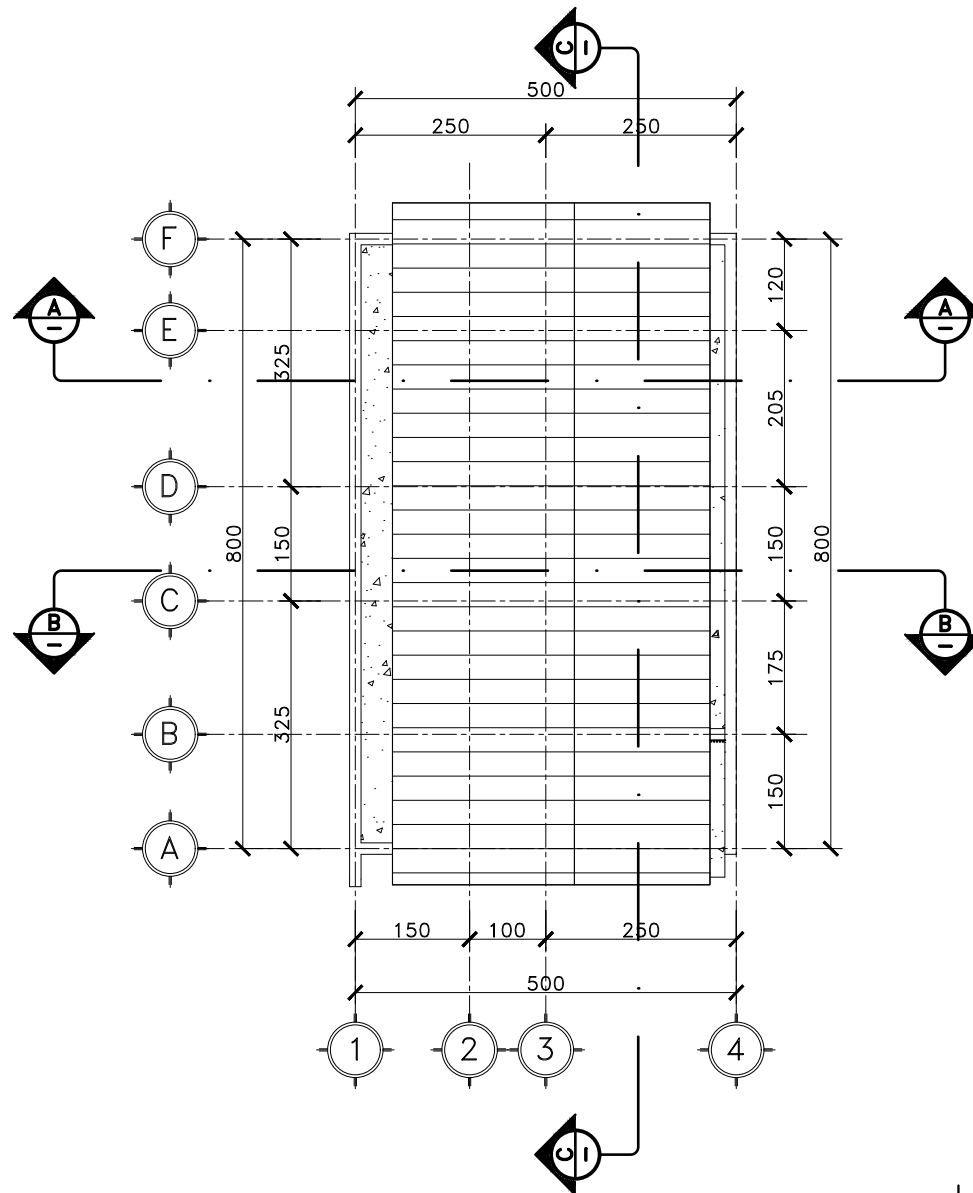

DENAH ATAP

SKALA 1:100

CATATAN

NAMA PROYEK

RUMAH TINGGAL
TYPE 40 BAPAK MULYONO

LOKASI

Balong, Cangkringan,
sleman, Yogyakarta

DIGAMBAR

BAGAS PRATAMA A.
DRAFTER

DIPERIKSA OLEH

HARYO BUWONO, SH.
KONTRAKTOR

DISETUJUI OLEH

BAPAK MULYONO
OWNER

JUDUL GAMBAR

DENAH ATAP

SKALA

1:100

NO. LEMBAR

ARS-3

REVISI NOMER

TANGGAL

10/07/2026

CATATAN

NAMA PROYEK

RUMAH TINGGAL
TYPE 40 BAPAK MULYONO

LOKASI

Balong, Cangkringan,
sleman, Yogyakarta

DIGAMBAR

BAGAS PRATAMA A.
DRAFTER

DIPERIKSA OLEH

HARYO BUWONO, SH.
KONTRAKTOR

DISETUJUI OLEH

BAPAK MULYONO
OWNER


JUDUL GAMBAR

POTONGAN A-A

SKALA NO. LEMBAR

1:100 ARS-4

REVISI NOMER TANGGAL
10/07/2026

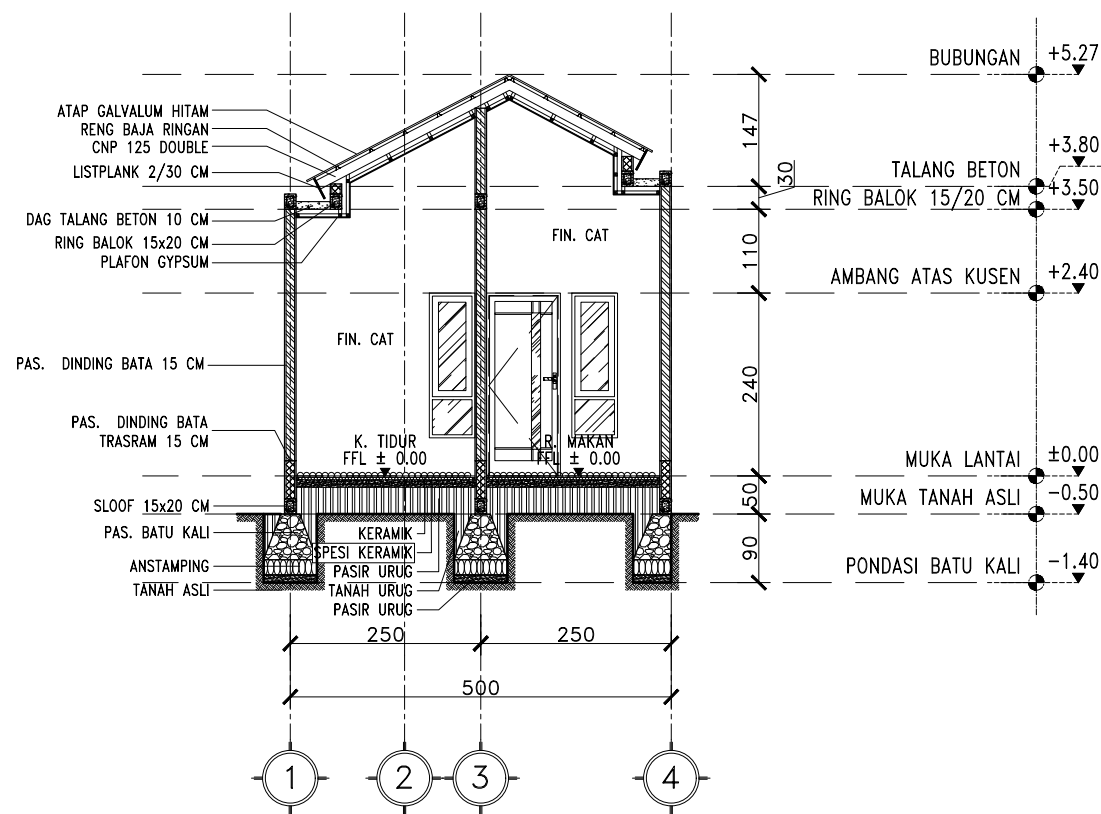

POTONGAN A-A

SKALA 1:100

CATATAN

NAMA PROYEK

RUMAH TINGGAL
TYPE 40 BAPAK MULYONO

LOKASI

Balong, Cangkringan,
sleman, Yogyakarta

DIGAMBAR

BAGAS PRATAMA A.
DRAFTER

DIPERIKSA OLEH

HARYO BUWONO, SH.
KONTRAKTOR

DISETUJUI OLEH

BAPAK MULYONO
OWNER

JUDUL GAMBAR

POTONGAN B-B

SKALA

NO. LEMBAR


1:100

ARS-5

REVISI NOMER

TANGGAL

10/07/2026

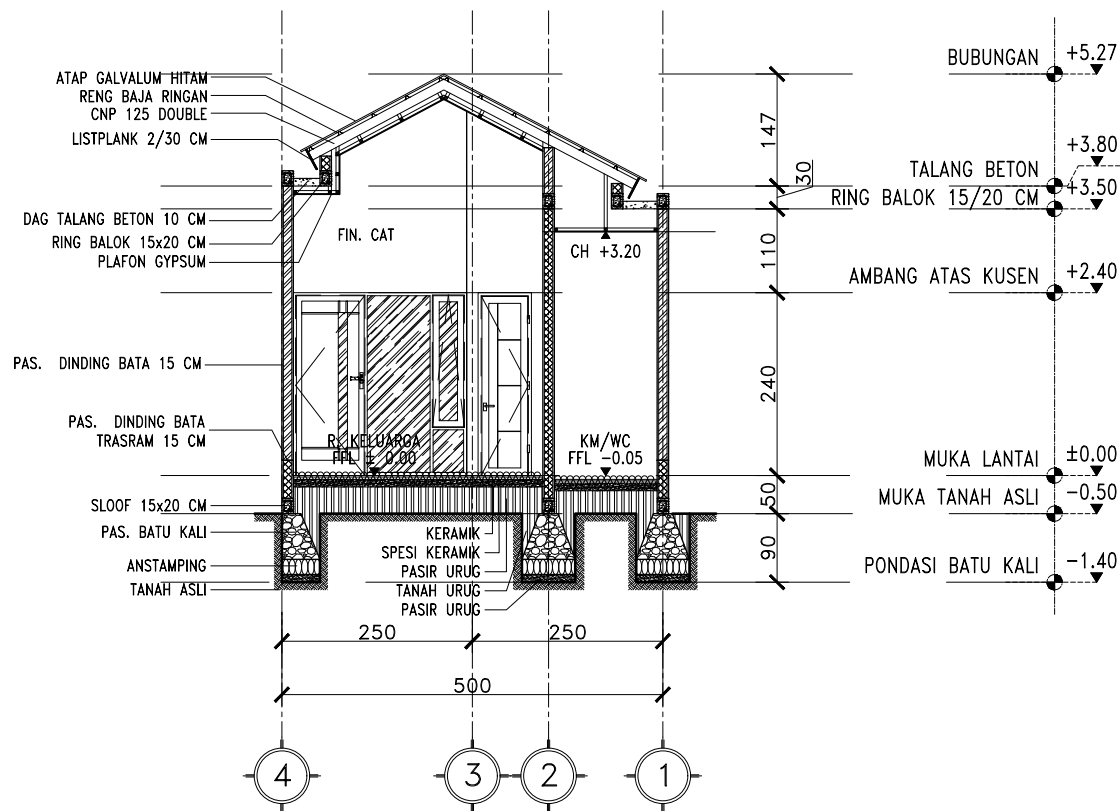

POTONGAN B-B

SKALA 1:100

CATATAN

NAMA PROYEK

RUMAH TINGGAL
TYPE 40 BAPAK MULYONO

LOKASI

Balong, Cangkringan,
sleman, Yogyakarta

DIGAMBAR

BAGAS PRATAMA A.
DRAFTER

DIPERIKSA OLEH

HARYO BUWONO, SH.
KONTRAKTOR

DISETUJUI OLEH

BAPAK MULYONO
OWNER

JUDUL GAMBAR

POTONGAN C-C

SKALA

NO. LEMBAR



1:100

ARS-6

REVISI NOMER


TANGGAL

10/07/2026

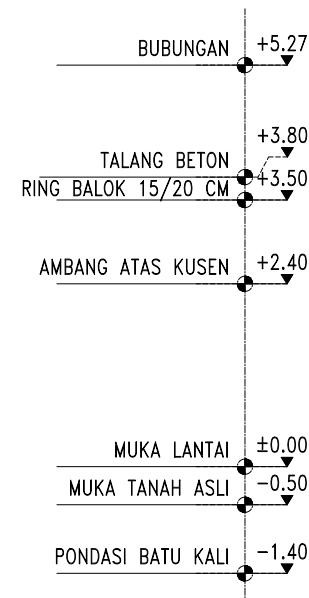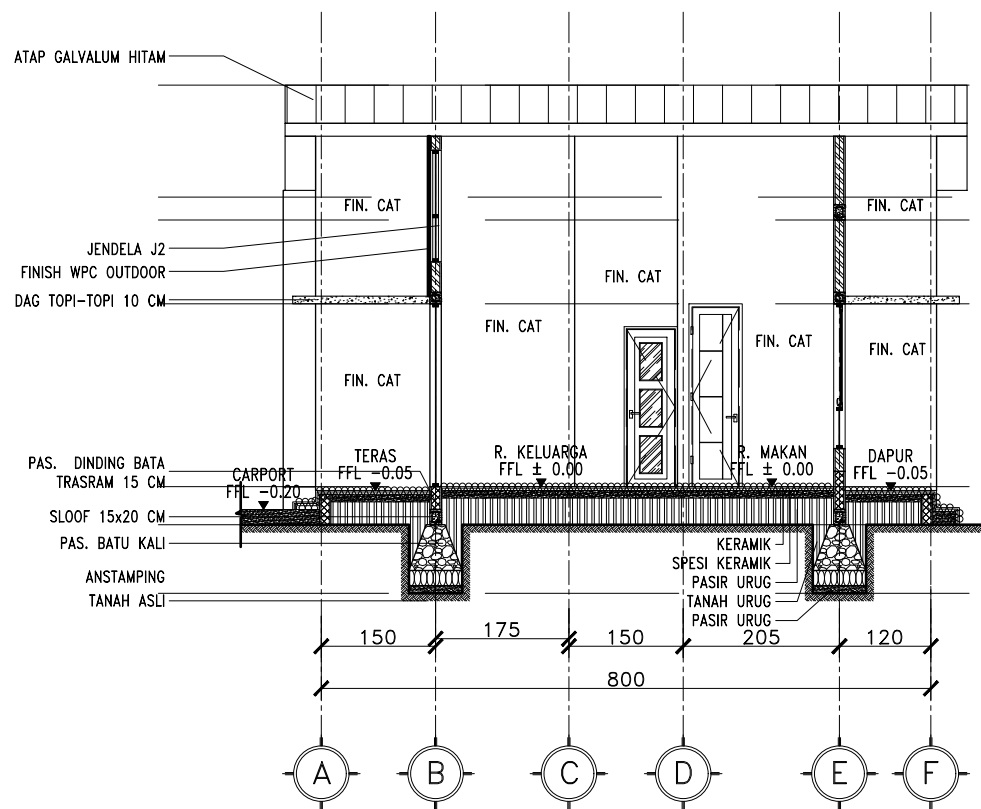

POTONGAN C-C

SKALA 1:100

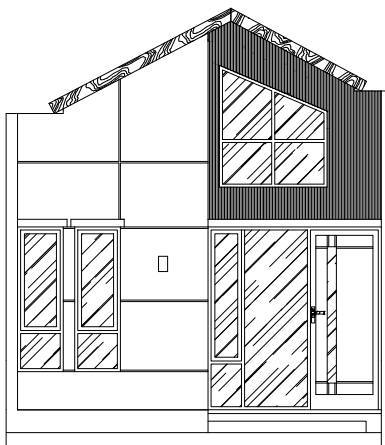

CATATAN

NAMA PROYEK

RUMAH TINGGAL
TYPE 40 BAPAK MULYONO

LOKASI

Balong, Cangkringan,
sleman, Yogyakarta

DIGAMBAR

BAGAS PRATAMA A.
DRAFTER

DIPERIKSA OLEH

HARYO BUWONO, SH.
KONTRAKTOR

DISETUJUI OLEH

BAPAK MULYONO
OWNER

JUDUL GAMBAR

TAMPAK DEPAN

SKALA

NO. LEMBAR

1:100

ARS-7

REVISI NOMER

TANGGAL

10/07/2026



TAMPAK DEPAN

SKALA 1:100

CATATAN

NAMA PROYEK

RUMAH TINGGAL
TYPE 40 BAPAK MULYONO

LOKASI

Balong, Cangkringan,
sleman, Yogyakarta

DIGAMBAR

BAGAS PRATAMA A.
DRAFTER

DIPERIKSA OLEH

HARYO BUWONO, SH.
KONTRAKTOR

DISETUJUI OLEH

BAPAK MULYONO
OWNER

JUDUL GAMBAR


TAMPAK SAMPING
KANAN

SKALA	NO. LEMBAR
-------	------------

1:100



ARS-8

REVISI NOMER	TANGGAL
	10/07/2026

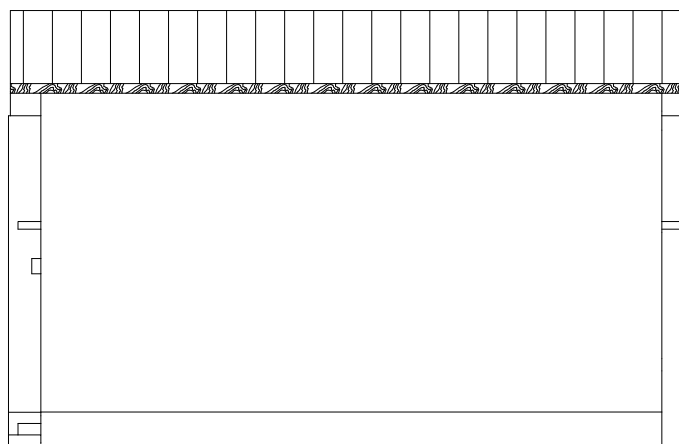

TAMPAK SAMPING KANAN

SKALA 1:100

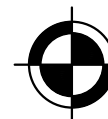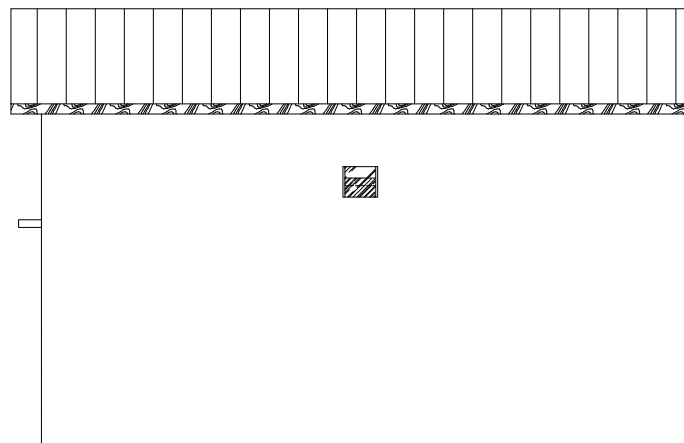

TAMPAK SAMPING KIRI

SKALA 1:100



CATATAN

NAMA PROYEK

RUMAH TINGGAL
TYPE 40 BAPAK MULYONO

LOKASI

Balong, Cangkringan,
sleman, Yogyakarta

DIGAMBAR

BAGAS PRATAMA A.
DRAFTER

DIPERIKSA OLEH

HARYO BUWONO, SH.
KONTRAKTOR

DISETUJUI OLEH

BAPAK MULYONO
OWNER

JUDUL GAMBAR

TAMPAK SAMPING
KIRI

SKALA

1:100


NO. LEMBAR

ARS-9

REVISI NOMER

TANGGAL

10/07/2026

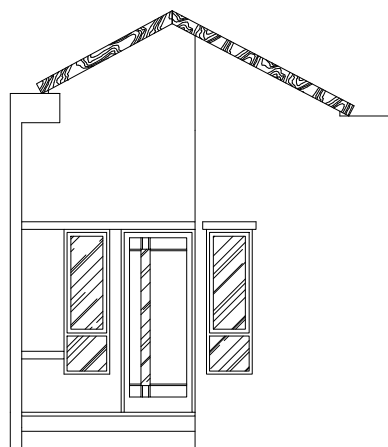

TAMPAK BELAKANG

SKALA 1:100



CATATAN

NAMA PROYEK

RUMAH TINGGAL
TYPE 40 BAPAK MULYONO

LOKASI

Balong, Cangkringan,
sleman, Yogyakarta

DIGAMBAR

BAGAS PRATAMA A.
DRAFTER

DIPERIKSA OLEH

HARYO BUWONO, SH.
KONTRAKTOR

DISETUJUI OLEH

BAPAK MULYONO
OWNER

JUDUL GAMBAR

TAMPAK BELAKANG

SKALA

1:100

NO. LEMBAR

ARS-10

REVISI NOMER TANGGAL

10/07/2026

CATATAN

NAMA PROYEK

RUMAH TINGGAL
TYPE 40 BAPAK MULYONO

LOKASI

Balong, Cangkringan,
sleman, Yogyakarta

DIGAMBAR

BAGAS PRATAMA A.
DRAFTER

DIPERIKSA OLEH

HARYO BUWONO, SH.
KONTRAKTOR

DISETUJUI OLEH

BAPAK MULYONO
OWNER

JUDUL GAMBAR

DENAH PONDASI

SKALA

NO. LEMBAR


1:100

STR-11

REVISI NOMER


TANGGAL

10/07/2026

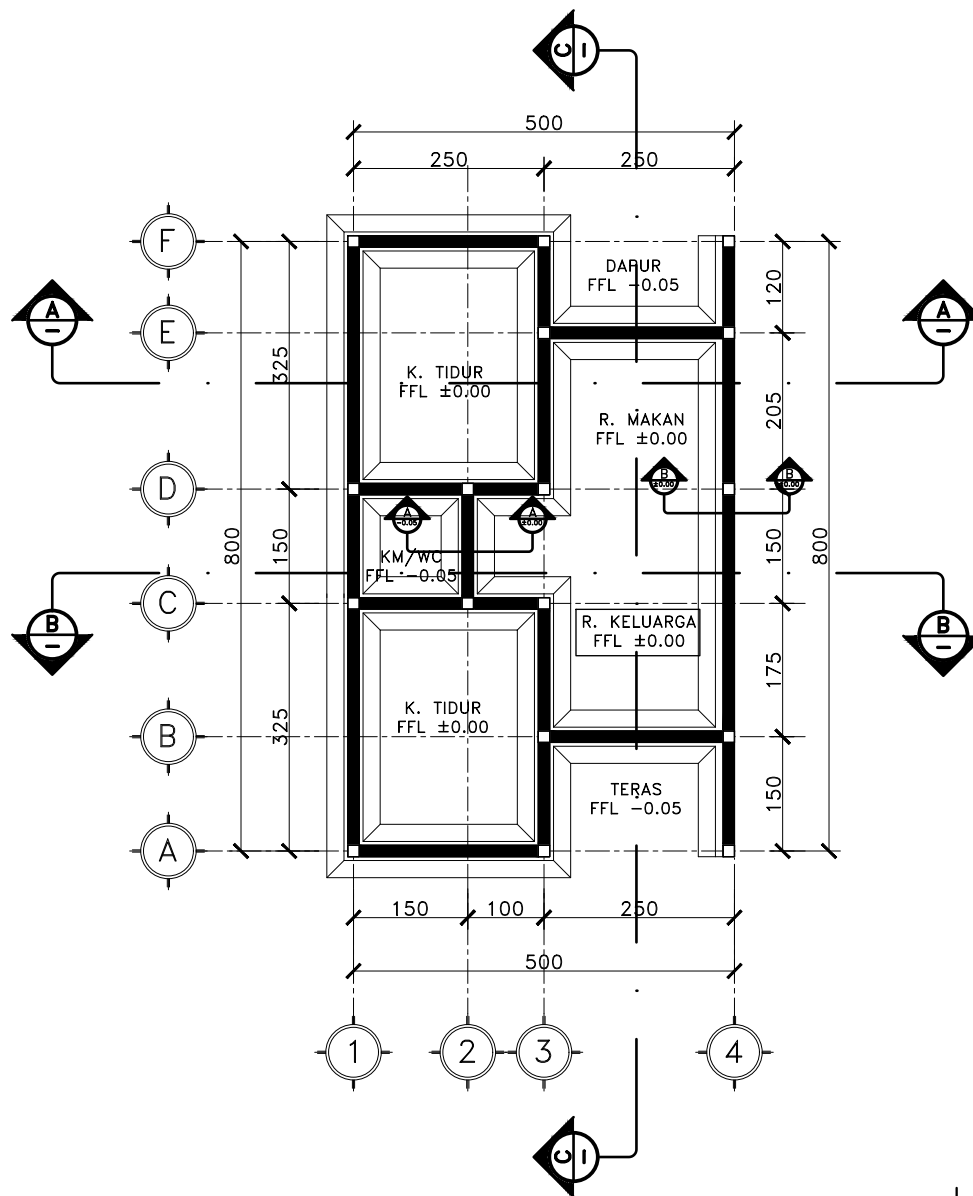

DENAH PONDASI

SKALA 1:100

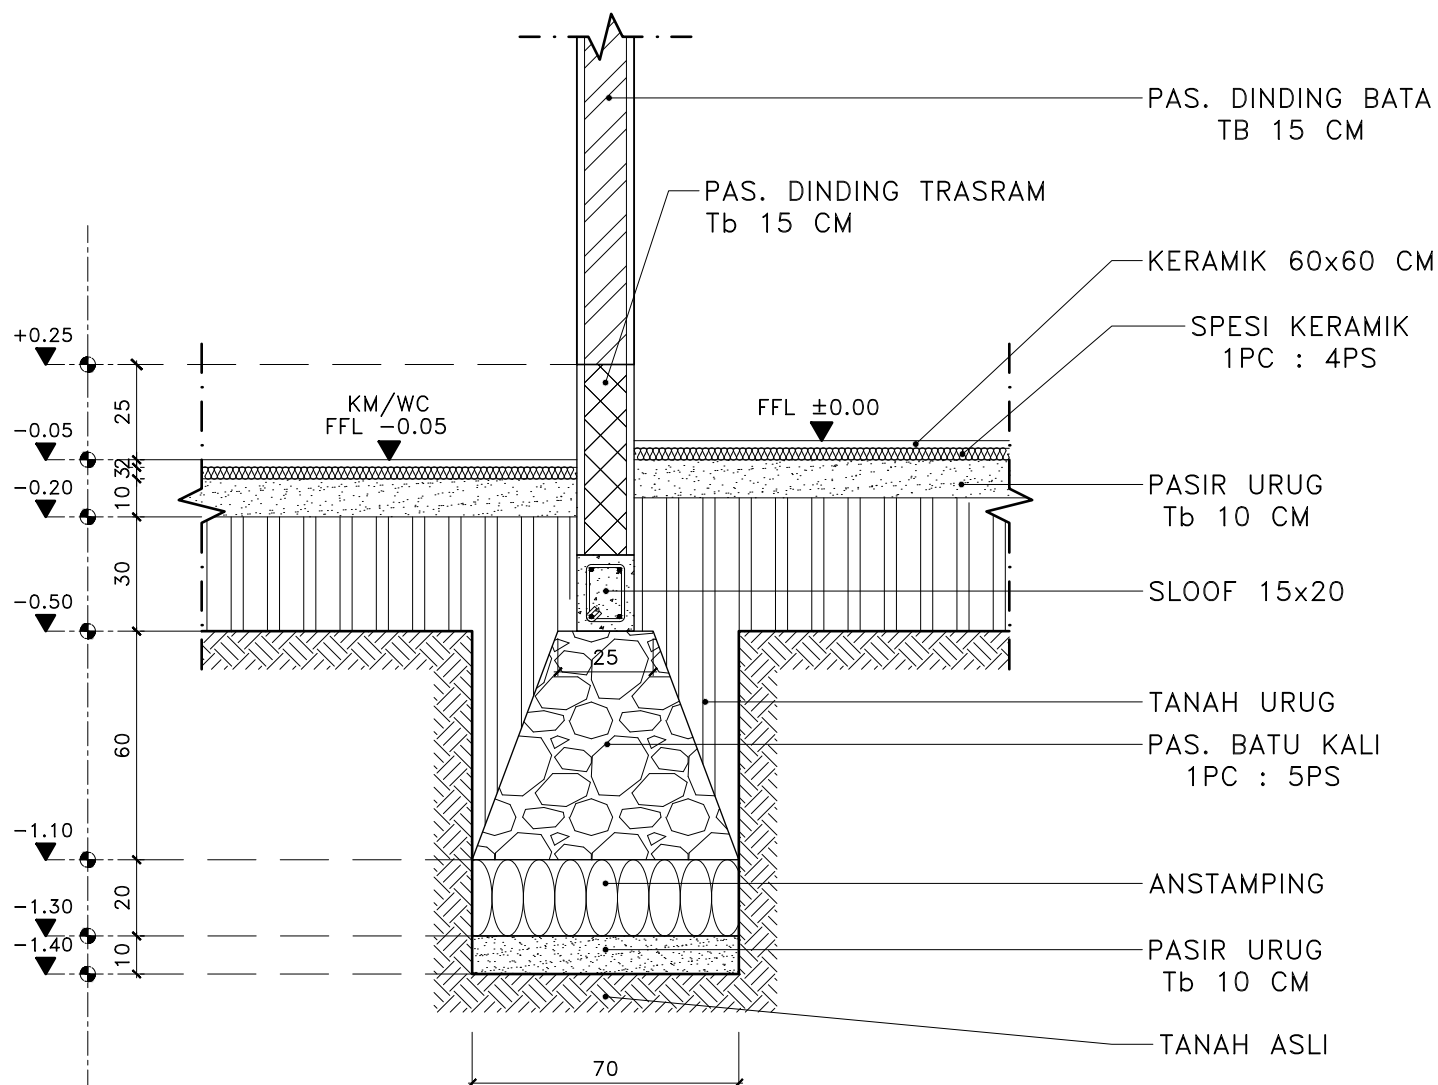

DETAIL PONDASI A-A

SKALA 1:20

CATATAN

NAMA PROYEK

RUMAH TINGGAL
TYPE 40 BAPAK MULYONO

LOKASI

Balong, Cangkringan,
sleman, Yogyakarta

DIGAMBAR

BAGAS PRATAMA A.
DRAFTER

DIPERIKSA OLEH

HARYO BUWONO, SH.
KONTRAKTOR

DISETUJUI OLEH

BAPAK MULYONO
OWNER

JUDUL GAMBAR

DETAIL PONDASI A-A

SKALA

1:20


NO. LEMBAR

STR-12

REVISI NOMER

TANGGAL

10/07/2026

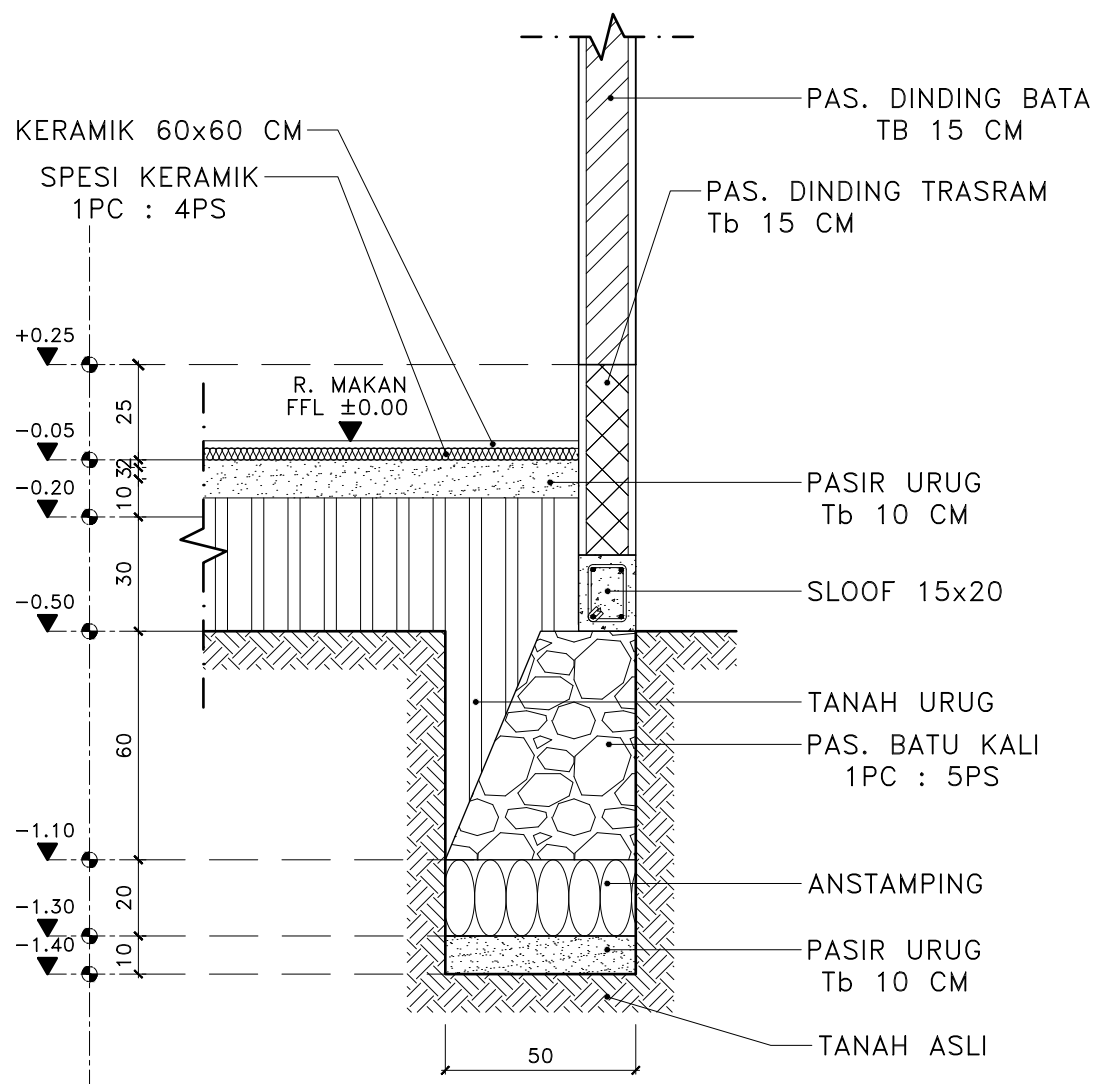

DETAIL PONDASI B-B

SKALA 1:20

CATATAN

NAMA PROYEK

RUMAH TINGGAL
TYPE 40 BAPAK MULYONO

LOKASI

Balong, Cangkringan,
sleman, Yogyakarta

DIGAMBAR

BAGAS PRATAMA A.
DRAFTER

DIPERIKSA OLEH

HARYO BUWONO, SH.
KONTRAKTOR

DISETUJUI OLEH

BAPAK MULYONO
OWNER

JUDUL GAMBAR

DETAIL PONDASI B-B

SKALA

1:20

NO. LEMBAR

STR-13

REVISI NOMER

TANGGAL

10/07/2026

CATATAN

NAMA PROYEK

RUMAH TINGGAL
TYPE 40 BAPAK MULYONO

LOKASI

Balong, Cangkringan,
sleman, Yogyakarta

DIGAMBAR

BAGAS PRATAMA A.
DRAFTER

DIPERIKSA OLEH

HARYO BUWONO, SH.
KONTRAKTOR

DISETUJUI OLEH

BAPAK MULYONO
OWNER

JUDUL GAMBAR

DENAH SLOOF

SKALA

NO. LEMBAR


1:100

STR-14

REVISI NOMER

TANGGAL

10/07/2026

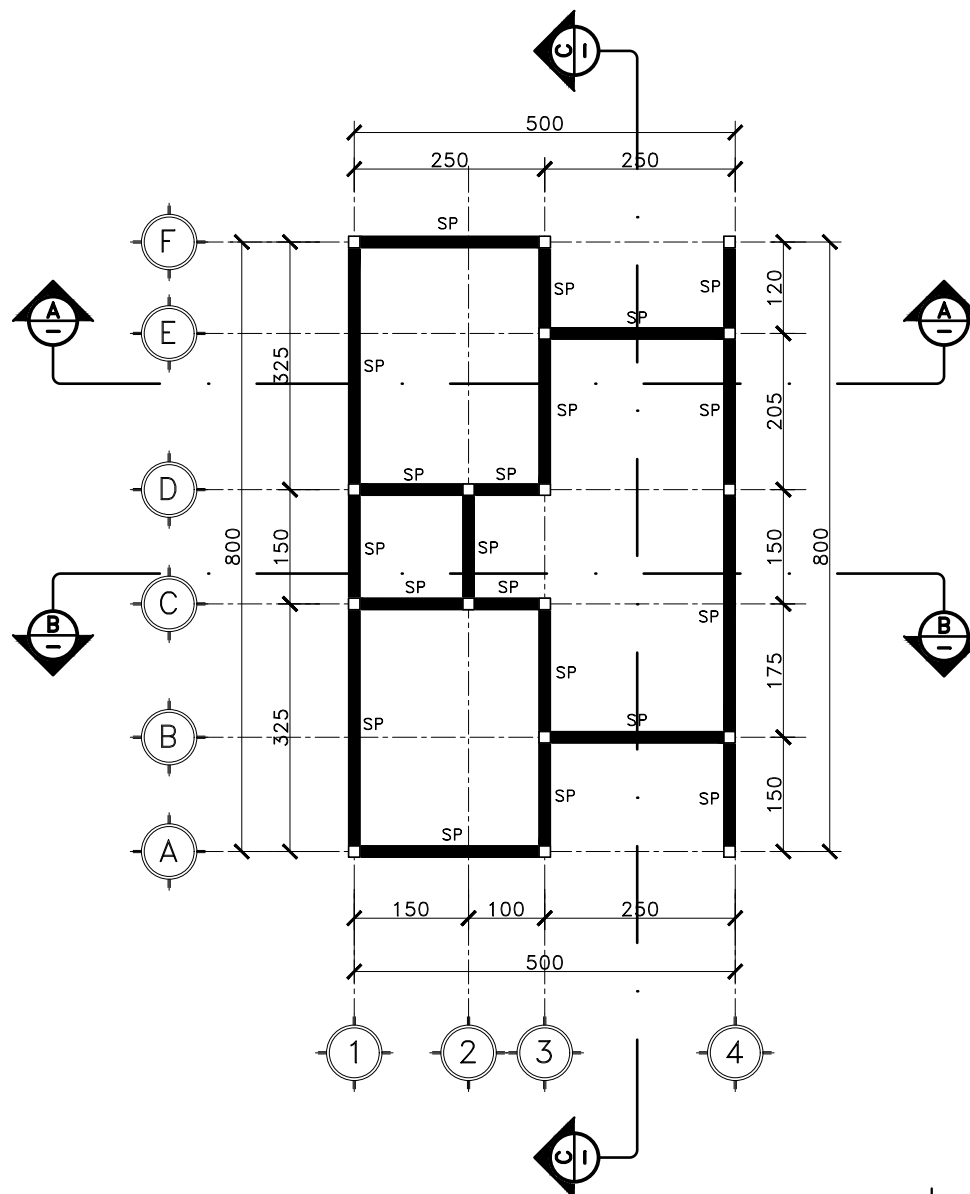

DENAH SLOOF

SKALA 1:100

CATATAN

NAMA PROYEK

RUMAH TINGGAL
TYPE 40 BAPAK MULYONO

LOKASI

Balong, Cangkringan,
sleman, Yogyakarta

DIGAMBAR

BAGAS PRATAMA A.
DRAFTER

DIPERIKSA OLEH

HARYO BUWONO, SH.
KONTRAKTOR

DISETUJUI OLEH

BAPAK MULYONO
OWNER

JUDUL GAMBAR

DETAIL SLOOF

SKALA

1:20




NO. LEMBAR

STR-15

REVISI NOMER

TANGGAL

10/07/2026

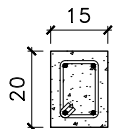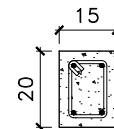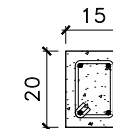TYPE	SP-SLOOF PRAKTIS (15x20 CM)		
POSISI	TUMPUAN KIRI	LAPANGAN	TUMPUAN KANAN
POTONGAN			
TULANGAN ATAS	2- ϕ 10	2- ϕ 10	2- ϕ 10
TULANGAN TENGAH	-	-	-
TULANGAN BAWAH	2- ϕ 10	2- ϕ 10	2- ϕ 10
SENGKANG	ϕ 6-150	ϕ 6-150	ϕ 6-150
SELIMUT BETON	2,5 CM	2,5 CM	2,5 CM



DETAIL SLOOF

SKALA 1:20

CATATAN

NAMA PROYEK

RUMAH TINGGAL
TYPE 40 BAPAK MULYONO

LOKASI

Balong, Cangkringan,
sleman, Yogyakarta

DIGAMBAR

BAGAS PRATAMA A.
DRAFTER

DIPERIKSA OLEH

HARYO BUWONO, SH.
KONTRAKTOR

DISETUJUI OLEH

BAPAK MULYONO
OWNER


JUDUL GAMBAR

DENAH KOLOM

SKALA NO. LEMBAR




1:100 STR-16




REVISI NOMER TANGGAL
10/07/2026

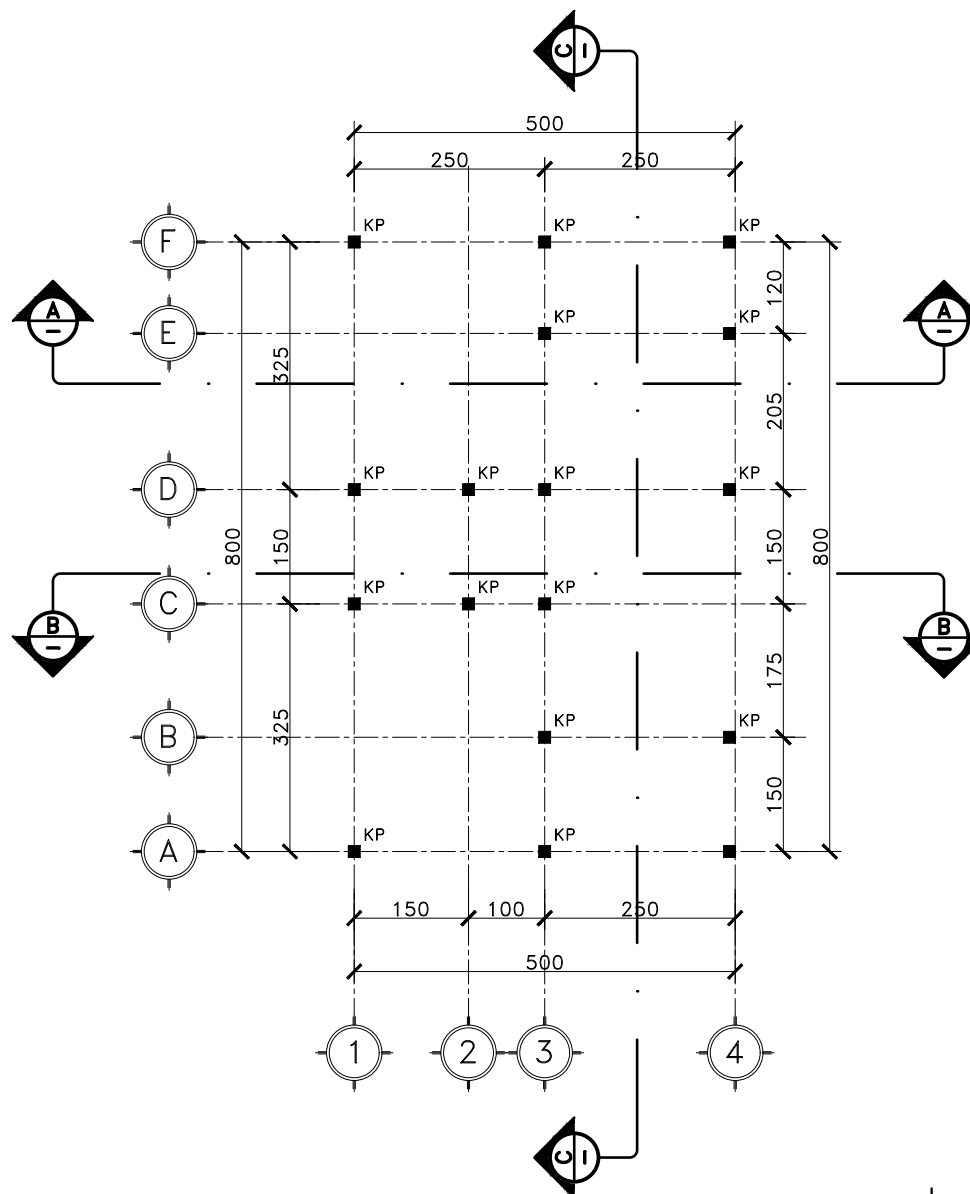


DENAH KOLOM

SKALA 1:100

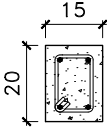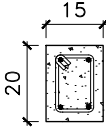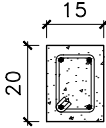TYPE	RB-RING BALOK (15x20 CM)		
POSISI	TUMPUAN KIRI	LAPANGAN	TUMPUAN KANAN
POTONGAN			
TULANGAN ATAS	2-ø8	2-ø8	2-ø8
TULANGAN TENGAH	-	-	-
TULANGAN BAWAH	2-ø8	2-ø8	2-ø8
SENGKANG	ø6-150	ø6-150	ø6-150
SELIMUT BETON	2,5 CM	2,5 CM	2,5 CM

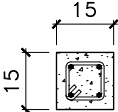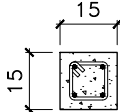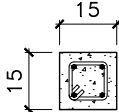TYPE	BL-BALOK LATEI (15x15 CM)		
POSISI	TUMPUAN KIRI	LAPANGAN	TUMPUAN KANAN
POTONGAN			
TULANGAN ATAS	2-ø8	2-ø8	2-ø8
TULANGAN TENGAH	-	-	-
TULANGAN BAWAH	2-ø8	2-ø8	2-ø8
SENGKANG	ø6-150	ø6-150	ø6-150
SELIMUT BETON	2.5 CM	2.5 CM	2.5 CM

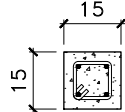TYPE	KP-KOLOM PRAKTIS (15x15 CM)
POTONGAN	
TUL. POKOK	4-ø8
SENGKANG	ø6-150
SELIMUT BETON	2,5 CM



DETAIL KOLOM & BALOK

SKALA 1:20

CATATAN

NAMA PROYEK

RUMAH TINGGAL
TYPE 40 BAPAK MULYONO

LOKASI

Balong, Cangkringan,
sleman, Yogyakarta

DIGAMBAR

BAGAS PRATAMA A.
DRAFTER

DIPERIKSA OLEH

HARYO BUWONO, SH.
KONTRAKTOR

DISETUJUI OLEH

BAPAK MULYONO
OWNER

JUDUL GAMBAR

DETAIL KOLOM & BALOK

SKALA

1:20

NO. LEMBAR

STR-19

REVISI NOMER	TANGGAL
	10/07/2026

CATATAN

NAMA PROYEK

RUMAH TINGGAL
TYPE 40 BAPAK MULYONO

LOKASI

Balong, Cangkringan,
sleman, Yogyakarta

DIGAMBAR

BAGAS PRATAMA A.
DRAFTER

DIPERIKSA OLEH

HARYO BUWONO, SH.
KONTRAKTOR

DISETUJUI OLEH

BAPAK MULYONO
OWNER

JUDUL GAMBAR

DENAH PINTU & JENDELA

SKALA

NO. LEMBAR


1:100

ARS-20

REVISI NOMER

TANGGAL

10/07/2026

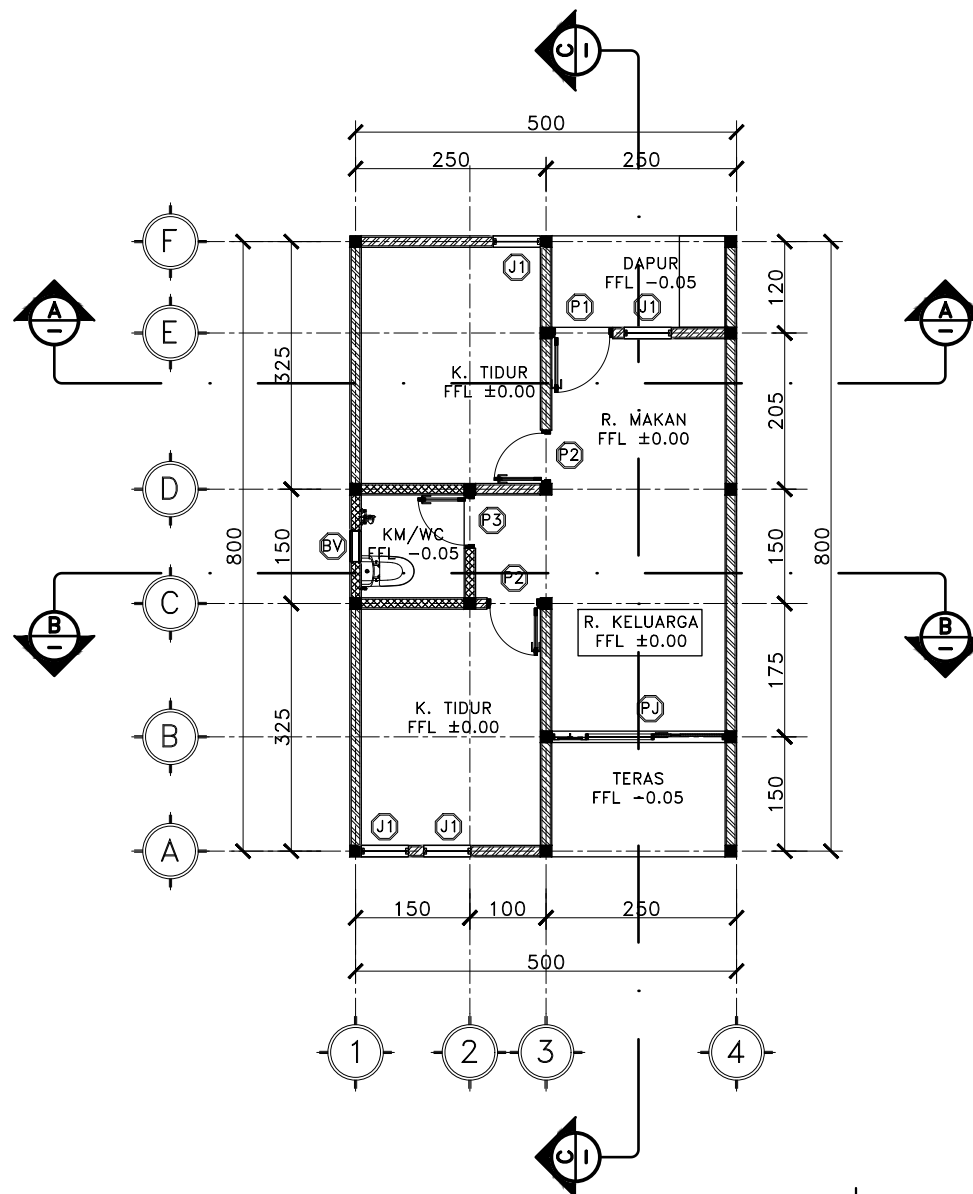

DENAH PINTU JENDELA

SKALA 1:100

CATATAN

NAMA PROYEK

RUMAH TINGGAL
TYPE 40 BAPAK MULYONO

LOKASI

Balong, Cangkringan,
sleman, Yogyakarta

DIGAMBAR

BAGAS PRATAMA A.
DRAFTER

DIPERIKSA OLEH

HARYO BUWONO, SH.
KONTRAKTOR

DISETUJUI OLEH

BAPAK MULYONO
OWNER




JUDUL GAMBAR

DETAIL PJ

SKALA NO. LEMBAR

1:25 ARS-21

REVISI NOMER 1
TANGGAL 10/07/2026

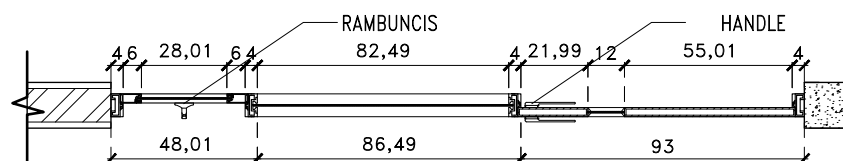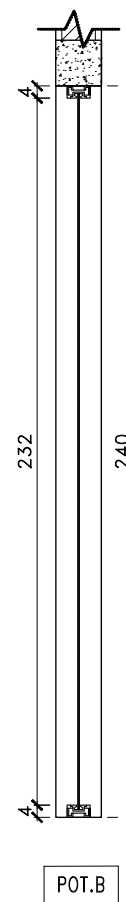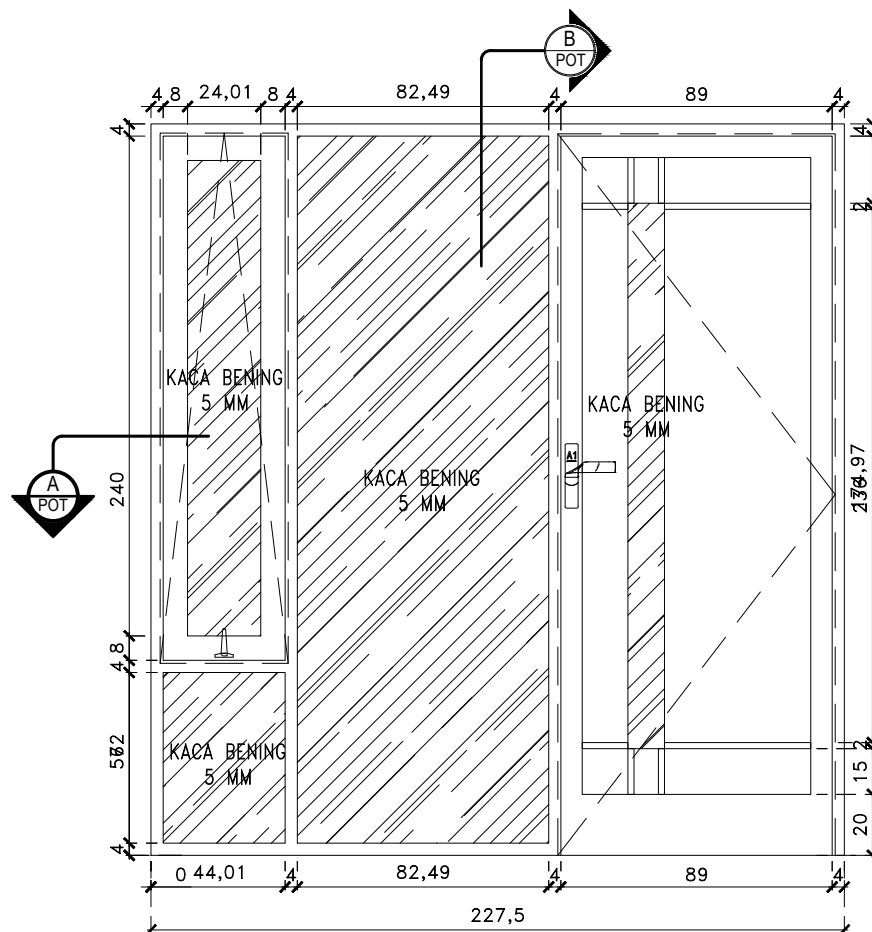

POT.A

LUAR

DALAM



TYPE		JUMLAH	PJ = 1 UNIT
UKURAN			240x227,5 CM
BAHAN	KUSEN/FRAME		ALUMUNIUM 4 CM
	RANGKA DAUN PINTU		ALUMUNIUM 4 CM
	KACA		KACA BENING 5 MM
BUKAAN			SWING 1 DAUN
FINISHING			HPL DOFF
LOKASI	TERAS DEPAN		1

CATATAN

NAMA PROYEK

RUMAH TINGGAL
TYPE 40 BAPAK MULYONO

LOKASI

Balong, Cangkringan,
sleman, Yogyakarta

DIGAMBAR

BAGAS PRATAMA A.
DRAFTER

DIPERIKSA OLEH

HARYO BUWONO, SH.
KONTRAKTOR

DISETUJUI OLEH

BAPAK MULYONO
OWNER



JUDUL GAMBAR

DETAIL P1

SKALA NO.LEMBAR

1:25 ARS-22

REVISI NOMER TANGGAL
10/07/2026

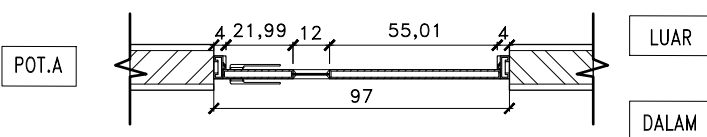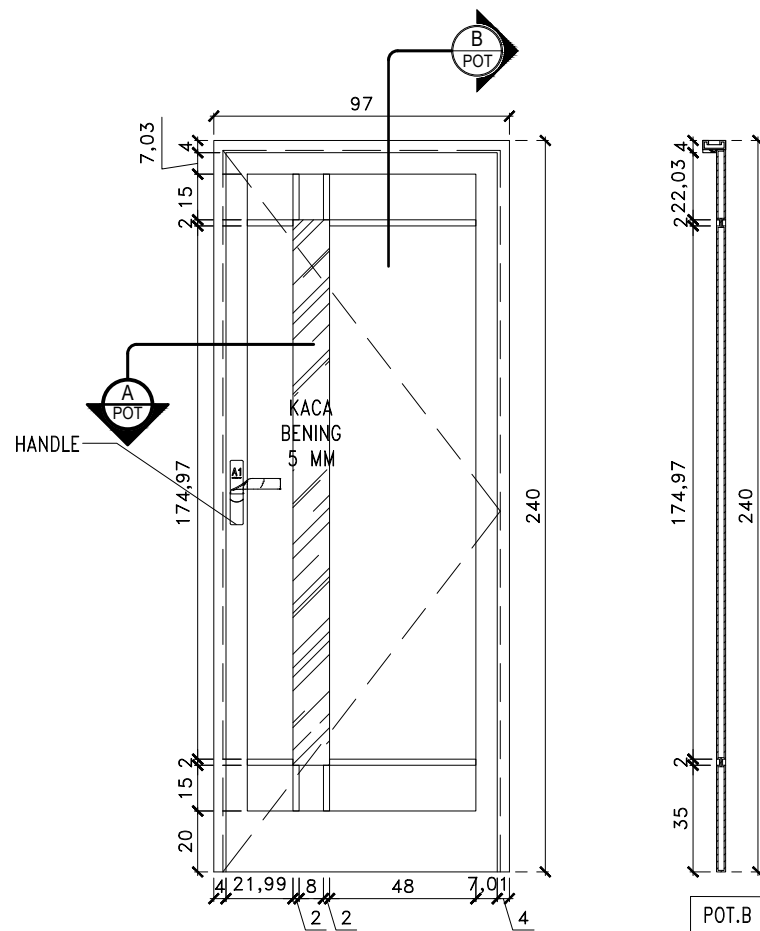

TYPE		JUMLAH	P1 = 1 UNIT
UKURAN			240x97 CM
BAHAN	KUSEN/FRAME		ALUMUNIUM 4 CM
	RANGKA DAUN PINTU		ALUMUNIUM 3x8 CM
	KACA		KACA BENING 5 MM
BUKAAN			SWING 1 DAUN
FINISHING			POWDER COATING WARNA DARK GREY
LOKASI	R.MAKAN		1

CATATAN

NAMA PROYEK

RUMAH TINGGAL
TYPE 40 BAPAK MULYONO

LOKASI

Balong, Cangkringan,
sleman, Yogyakarta

DIGAMBAR

BAGAS PRATAMA A.
DRAFTER

DIPERIKSA OLEH

HARYO BUWONO, SH.
KONTRAKTOR

DISETUJUI OLEH

BAPAK MULYONO
OWNER



JUDUL GAMBAR

DETAIL P2

SKALA NO. LEMBAR

1:25 ARS-23

REVISI NOMER TANGGAL
10/07/2026

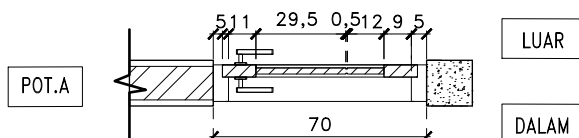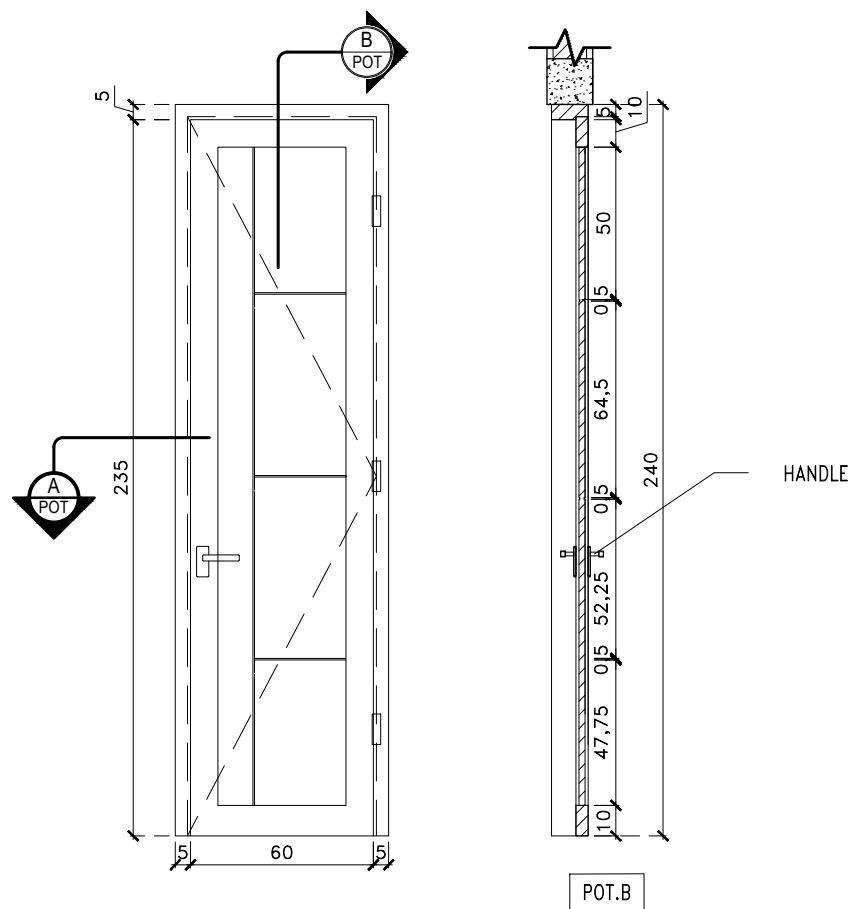

DETAIL P2

SKALA 1:25

TYPE		JUMLAH	P2 = 2 UNIT
UKURAN			210x70 CM
BAHAN	KUSEN/FRAME		KAYU SOLID 12/5 CM
	RANGKA DAUN PINTU		KAYU SOLID TEBAL 3 CM
	KACA		-
BUKAAN			SWING 1 DAUN
FINISHING			-
LOKASI	KAMAR TIDUR		2

CATATAN

NAMA PROYEK

RUMAH TINGGAL
TYPE 40 BAPAK MULYONO

LOKASI

Balong, Cangkringan,
sleman, Yogyakarta

DIGAMBAR

BAGAS PRATAMA A.
DRAFTER

DIPERIKSA OLEH

HARYO BUWONO, SH.
KONTRAKTOR

DISETUJUI OLEH

BAPAK MULYONO
OWNER

JUDUL GAMBAR


DETAIL P3

SKALA NO. LEMBAR

1:25 ARS-24

REVISI NOMER TANGGAL
10/07/2026

TYPE		JUMLAH	P4 = 3 UNIT
UKURAN			210x70 CM
BAHAN	KUSEN/FRAME		ALUMUNIU 3"
	RANGKA DAUN PINTU		ALUMUNIU 3x8 CM
	KACA		KACA ACID 5 MM
BUKAAN			SWING 1 DAUN
FINISHING			POWDER COATING WARNA DARK GREY
LOKASI	KM/WC		1

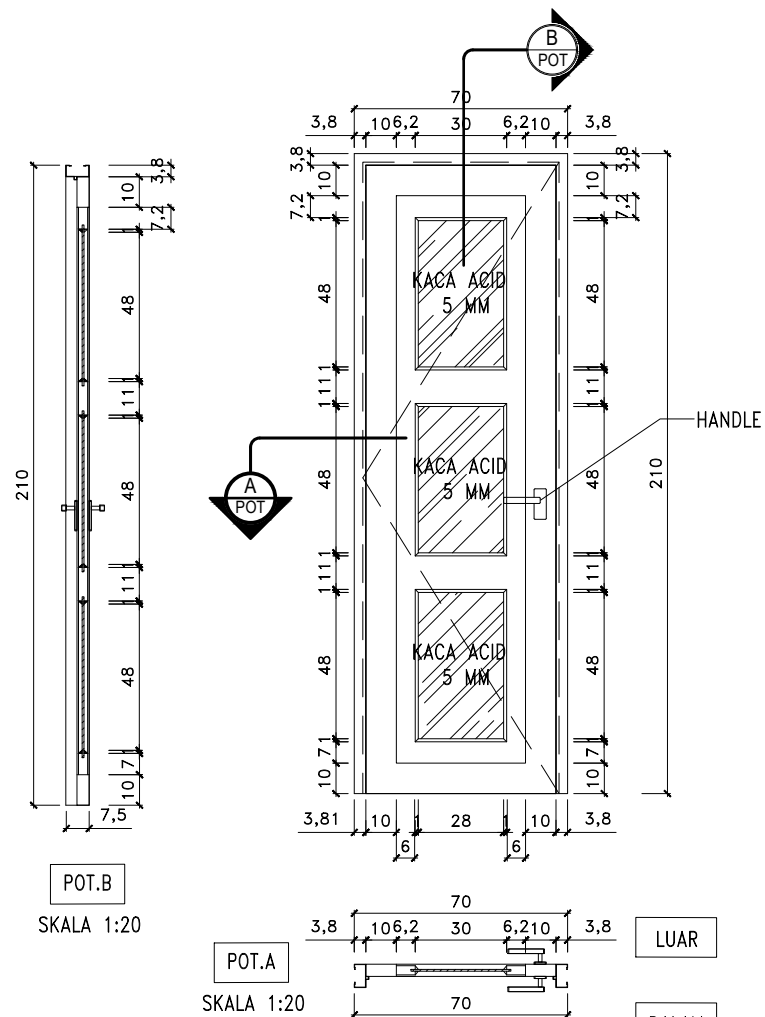

10/07/2026

CATATAN

NAMA PROYEK

RUMAH TINGGAL
TYPE 40 BAPAK MULYONO

LOKASI

Balong, Cangkringan,
sleman, Yogyakarta

DIGAMBAR

BAGAS PRATAMA A.
DRAFTER

DIPERIKSA OLEH

HARYO BUWONO, SH.
KONTRAKTOR

DISETUJUI OLEH

BAPAK MULYONO
OWNER



JUDUL GAMBAR

DETAIL J2


SKALA NO. LEMBAR

1:25 ARS-26

REVISI NOMER TANGGAL
10/07/2026

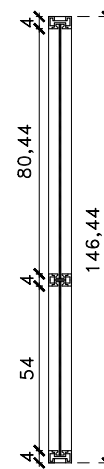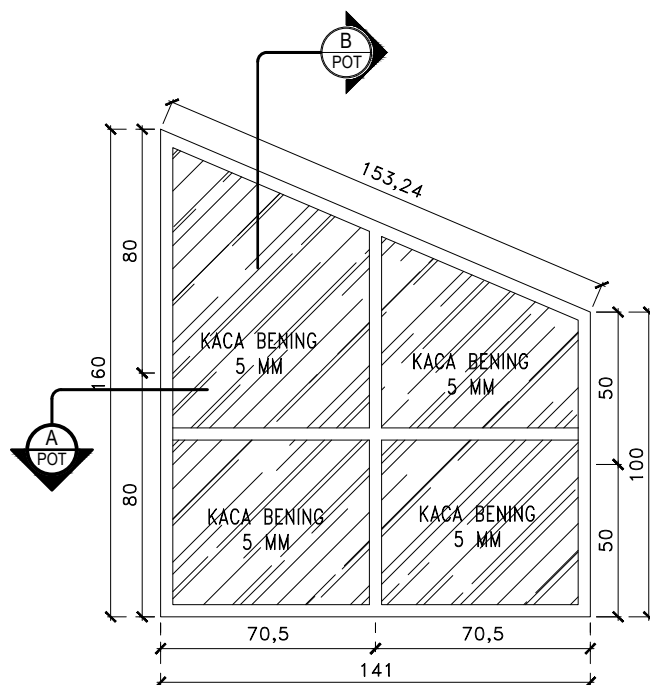


POT.B

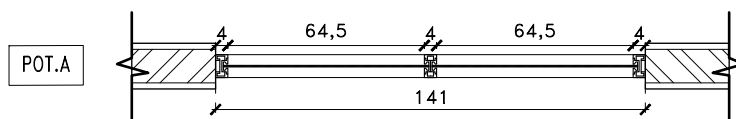

POT.A

LUAR

DALAM

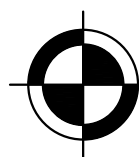

DETAIL J2

SKALA 1:25

TYPE		JUMLAH	J2 = 1 UNIT
UKURAN			160x141 CM
BAHAN	KUSEN/FRAME		ALUMUNUM 4 CM
	RANGKA DAUN PINTU		-
	KACA		KACA BENING 5 MM
BUKAAN			KACA MATI 4
FINISHING			POWDER COATING WARNA DARK GREY
LOKASI	R.KELUARGA		1

CATATAN

NAMA PROYEK

RUMAH TINGGAL
TYPE 40 BAPAK MULYONO

LOKASI

Balong, Cangkringan,
sleman, Yogyakarta

DIGAMBAR

BAGAS PRATAMA A.
DRAFTER

DIPERIKSA OLEH

HARYO BUWONO, SH.
KONTRAKTOR

DISETUJUI OLEH

BAPAK MULYONO
OWNER


JUDUL GAMBAR

DETAIL BV

SKALA NO. LEMBAR

1:25 ARS-27

REVISI NOMER TANGGAL
10/07/2026

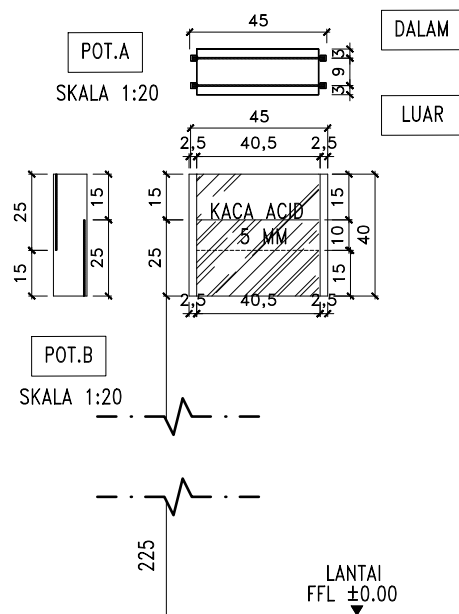

TYPE		JUMLAH	BV = 1 UNIT
UKURAN			45x40 CM
BAHAN	KUSEN/FRAME		ALUMUNIUM 3"
	RANGKA DAUN JENDELA		ALUMUNIUM 3x8 CM
	KACA		KACA ACID 5 MM
BUKAAN			KACA MATI 1
FINISHING			POWDER COATING WARNA DARK GREY
LOKASI	KM/WC		1

CATATAN

NAMA PROYEK

RUMAH TINGGAL
TYPE 40 BAPAK MULYONO

LOKASI

Balong, Cangkringan,
sleman, Yogyakarta

DIGAMBAR

BAGAS PRATAMA A.
DRAFTER

DIPERIKSA OLEH

HARYO BUWONO, SH.
KONTRAKTOR

DISETUJUI OLEH

BAPAK MULYONO
OWNER


JUDUL GAMBAR

DENAH FINISHING
LANTAI

SKALA NO. LEMBAR

1:100 ARS-28

REVISI NOMER TANGGAL
10/07/2026

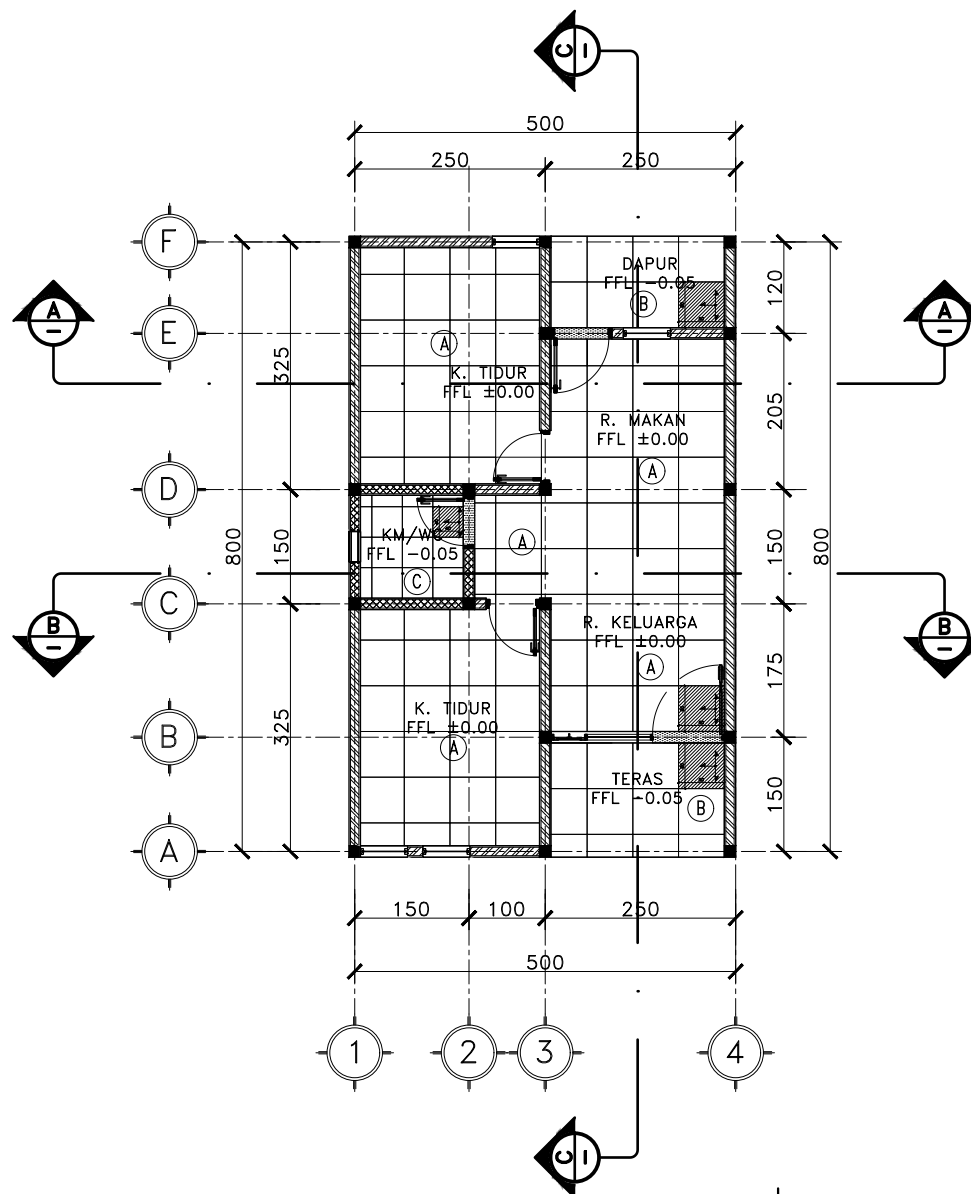

DENAH FINISHING LANTAI

SKALA 1:100

CATATAN

NAMA PROYEK

RUMAH TINGGAL
TYPE 40 BAPAK MULYONO

LOKASI

Balong, Cangkringan,
sleman, Yogyakarta

DIGAMBAR

BAGAS PRATAMA A.
DRAFTER

DIPERIKSA OLEH

HARYO BUWONO, SH.
KONTRAKTOR

DISETUJUI OLEH

BAPAK MULYONO
OWNER

JUDUL GAMBAR

DENAH PLAFOND

SKALA

NO. LEMBAR


1:100

ARS-29

REVISI NOMER

TANGGAL

10/07/2026

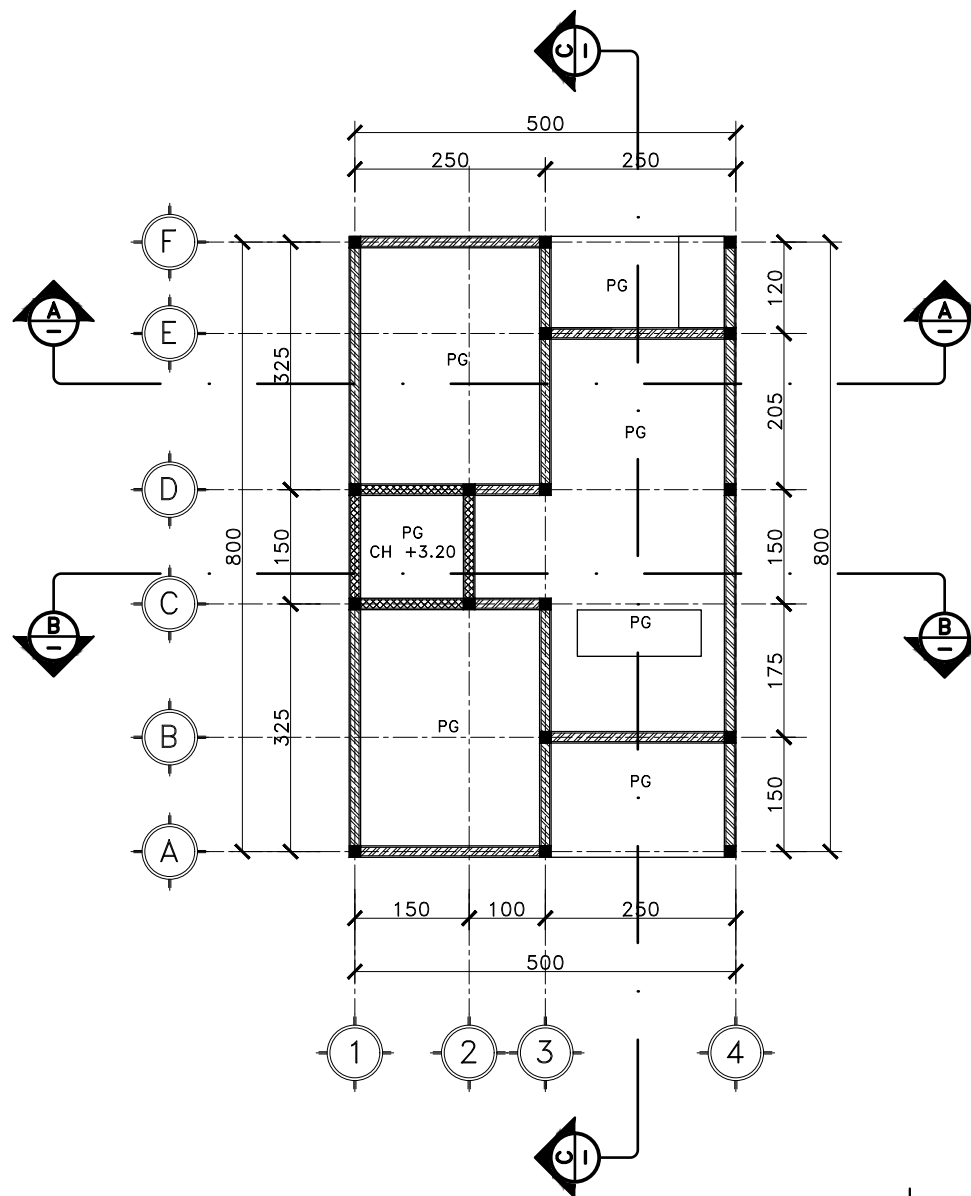

CATATAN: PEMASANGAN PLAFON GYPSUM
MENGIKUTI KEMIRINGAN ATAP
KECUALI KAMAR MANDI



DENAH PLAFOND

SKALA 1:100

CATATAN

NAMA PROYEK

RUMAH TINGGAL
TYPE 40 BAPAK MULYONO

LOKASI

Balong, Cangkringan,
sleman, Yogyakarta

DIGAMBAR

BAGAS PRATAMA A.
DRAFTER

DIPERIKSA OLEH

HARYO BUWONO, SH.
KONTRAKTOR

DISETUJUI OLEH

BAPAK MULYONO
OWNER

JUDUL GAMBAR



DENAH INSTALASI
LISTRIK

SKALA NO. LEMBAR

1:100

MEP-30

REVISI NOMER TANGGAL
10/07/2026

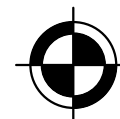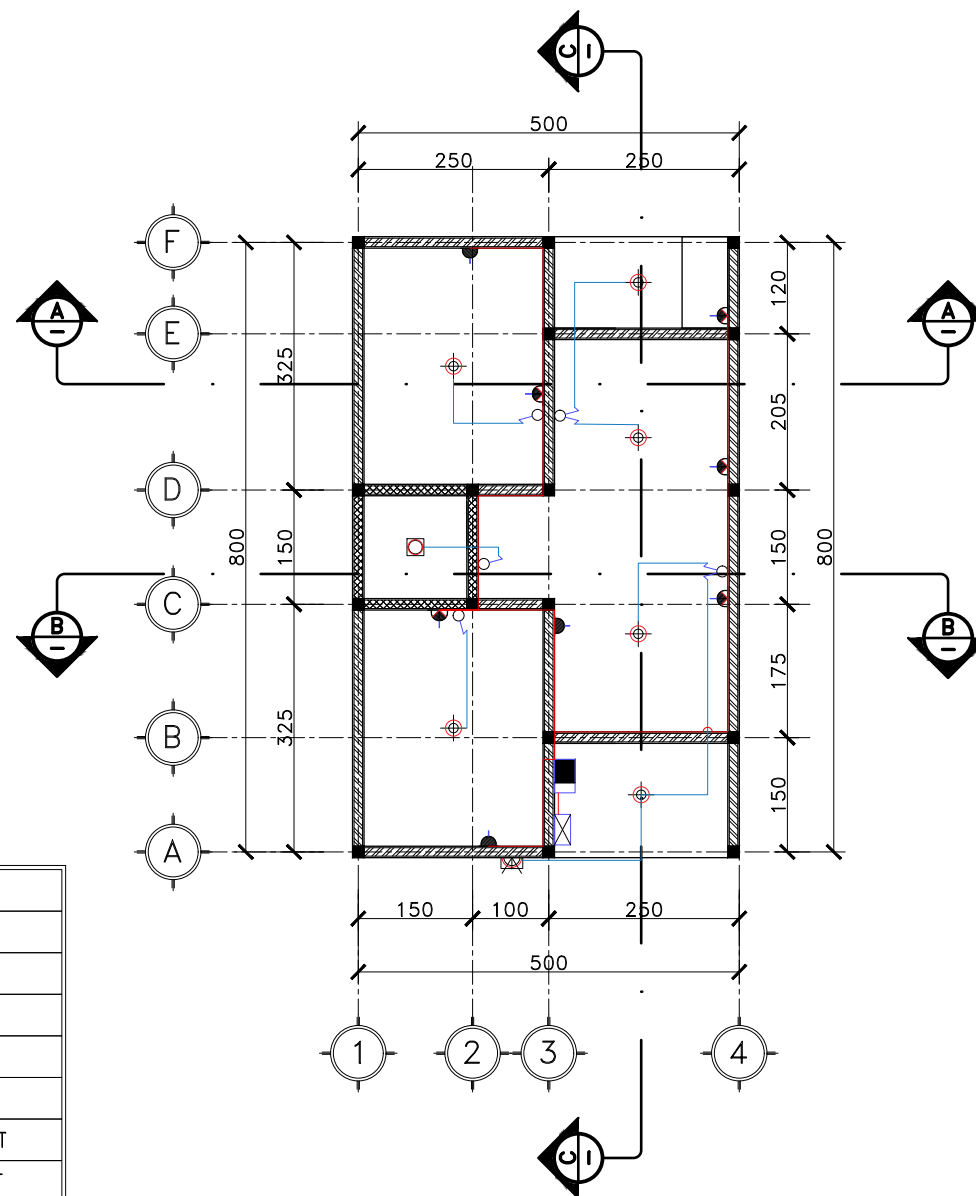

DENAH INSTALASI LISTRIK

SKALA 1:100

KETERANGAN

	TITIK LAMPU DOWN LIGHT 20 WATT
	TITIK LAMPU DINDING 15 WATT
	TITIK LAMPU DOWN LIGHT OUTBOW 20 WATT
	(1.4m) SAKLAR TUNGGAL
	(1.4m) SAKLAR SERI
	(60cm) KETINGGIAN STOP KONTAK 200 WATT
	(1.4m) KETINGGIAN STOP KONTAK 200 WATT
	BOX PANEL PEMBAGI (MCB) 10 A OTOMATIS
	BOX METER
	KABEL PRIMER
	KABEL SEKUNDER

CATATAN

NAMA PROYEK

RUMAH TINGGAL
TYPE 40 BAPAK MULYONO

LOKASI

Balong, Cangkringan,
sleman, Yogyakarta

DIGAMBAR

BAGAS PRATAMA A.
DRAFTER

DIPERIKSA OLEH

HARYO BUWONO, SH.
KONTRAKTOR

DISETUJUI OLEH

BAPAK MULYONO
OWNER

JUDUL GAMBAR


DENAH INSTALASI
AIR BERSIH

SKALA NO. LEMBAR

1:100

MEP-31

REVISI NOMER
TANGGAL
10/07/2026

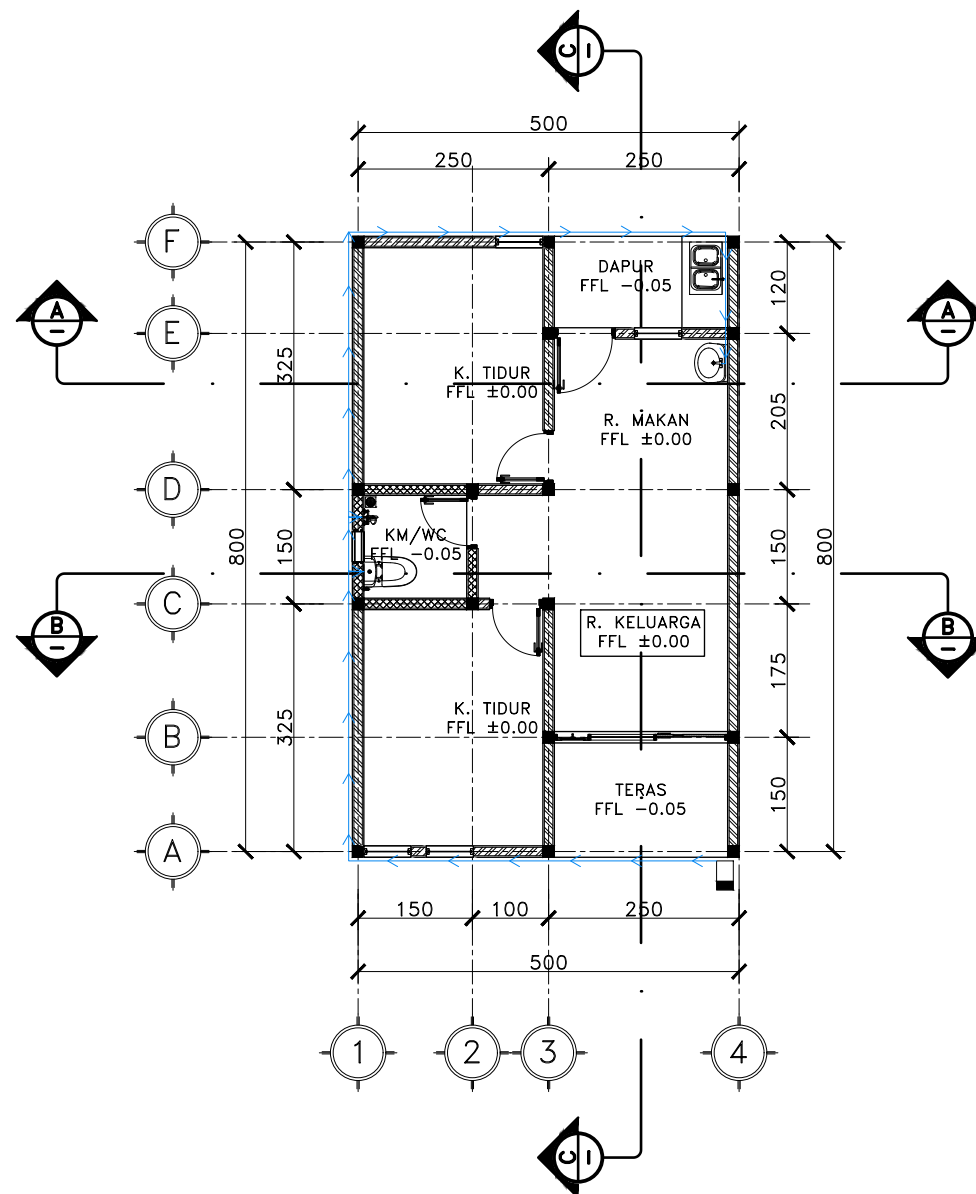

DENAH INSTALASI AIR BERSIH

SKALA 1:100

SIMBOL	KETERANGAN
PA	: PDAM
KR	: KERAN AIR
FD	: FLOOR DRAIN
SK	: KITCHEN SINK
CD	: CLOSET DUDUK
SP	: SEPTICTANK
BK	: BAK KONTROL
SR	: SUMUR RESAPAN
SW	: SHOWER
RD	: ROOF DRAIN
WT	: WASTAFEL
	: ARAH ALIRAN AIR
	: SALURAN AIR BERSIH (PVC AW Ø 1")
	: SALURAN AIR HUJAN (PVC AW Ø 3")
	: SALURAN AIR KOTOR (PVC AW Ø 4")
	: SALURAN PIPA AIR HUJAN NAIK/TURUN

CATATAN

NAMA PROYEK

RUMAH TINGGAL
TYPE 40 BAPAK MULYONO

LOKASI

Balong, Cangkringan,
sleman, Yogyakarta

DIGAMBAR

BAGAS PRATAMA A.
DRAFTER

DIPERIKSA OLEH

HARYO BUWONO, SH.
KONTRAKTOR

DISETUJUI OLEH

BAPAK MULYONO
OWNER

JUDUL GAMBAR


DENAH INSTALASI
AIR KOTOR

SKALA NO. LEMBAR

1:100

MEP-32

REVISI NOMER
TANGGAL
10/07/2026

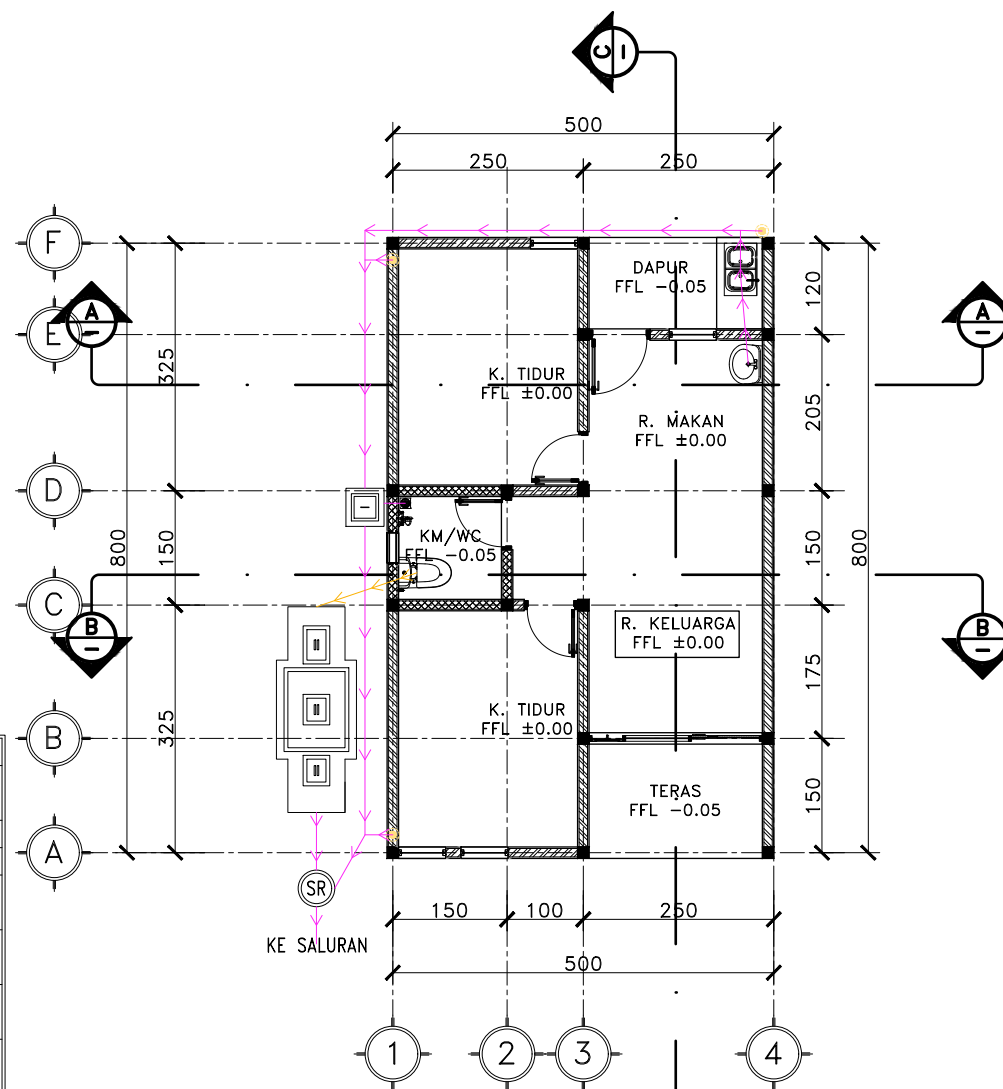

SIMBOL	KETERANGAN
PA	: PDAM
KR	: KERAN AIR
FD	: FLOOR DRAIN
SK	: KITCHEN SINK
CD	: CLOSET DUDUK
SP	: SEPTICTANK
BK	: BAK KONTROL
SR	: SUMUR RESAPAN
SW	: SHOWER
RD	: ROOF DRAIN
WT	: WASTAFEL
~>	: ARAH ALIRAN AIR
---	: SALURAN AIR BERSIH (PVC AW Ø 1")
---	: SALURAN AIR HUJAN (PVC AW Ø 3")
---	: SALURAN AIR KOTOR (PVC AW Ø 4")
---	: SALURAN PIPA AIR HUJAN NAIK/TURUN



DENAH INSTALASI AIR KOTOR

SKALA 1:100

CATATAN

NAMA PROYEK

RUMAH TINGGAL
TYPE 40 BAPAK MULYONO

LOKASI

Balong, Cangkringan,
sleman, Yogyakarta

DIGAMBAR

BAGAS PRATAMA A.
DRAFTER

DIPERIKSA OLEH

HARYO BUWONO, SH.
KONTRAKTOR

DISETUJUI OLEH

BAPAK MULYONO
OWNER

JUDUL GAMBAR


DENAH INSTALASI
AIR HUJAN

SKALA NO. LEMBAR

1:100

MEP-33

REVISI NOMER
TANGGAL
10/07/2026

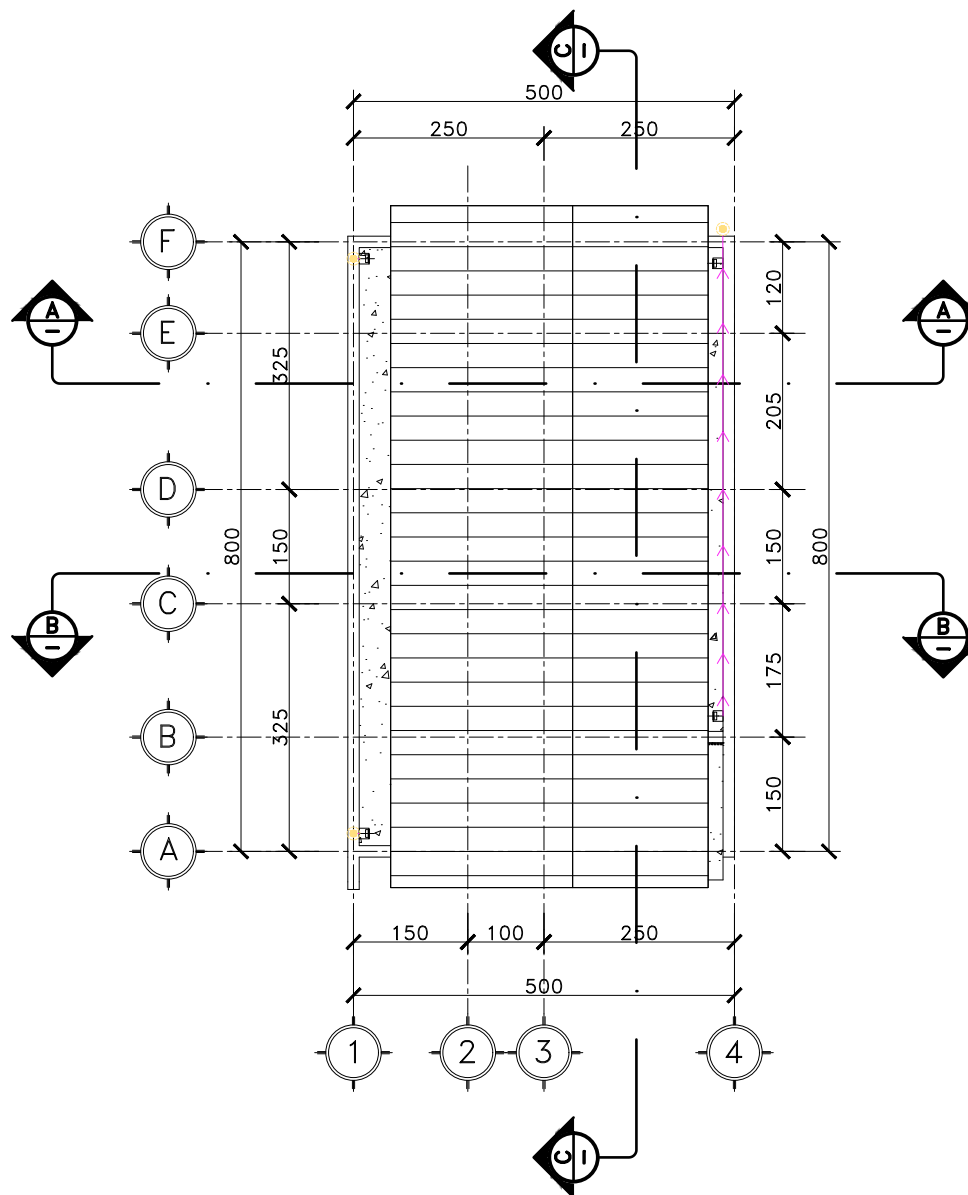

DENAH INSTALASI AIR HUJAN

SKALA 1:100

SIMBOL	KETERANGAN
PA	: PDAM
KR	: KERAN AIR
FD	: FLOOR DRAIN
SK	: KITCHEN SINK
CD	: CLOSET DUDUK
SP	: SEPTICTANK
BK	: BAK KONTROL
SR	: SUMUR RESAPAN
SW	: SHOWER
RD	: ROOF DRAIN
WT	: WASTAFEL
	: ARAH ALIRAN AIR
	: SALURAN AIR BERSIH (PVC AW Ø 1")
	: SALURAN AIR HUJAN (PVC AW Ø 3")
	: SALURAN AIR KOTOR (PVC AW Ø 4")
	: SALURAN PIPA AIR HUJAN NAIK/TURUN

CATATAN

NAMA PROYEK

RUMAH TINGGAL
TYPE 40 BAPAK MULYONO

LOKASI

Balong, Cangkringan,
sleman, Yogyakarta

DIGAMBAR

BAGAS PRATAMA A.
DRAFTER

DIPERIKSA OLEH

HARYO BUWONO, SH.
KONTRAKTOR

DISETUJUI OLEH

BAPAK MULYONO
OWNER

JUDUL GAMBAR

DETAIL SEPTICTANK

SKALA

1:50


NO. LEMBAR

MEP-34


REVISI NOMER

TANGGAL

10/07/2026

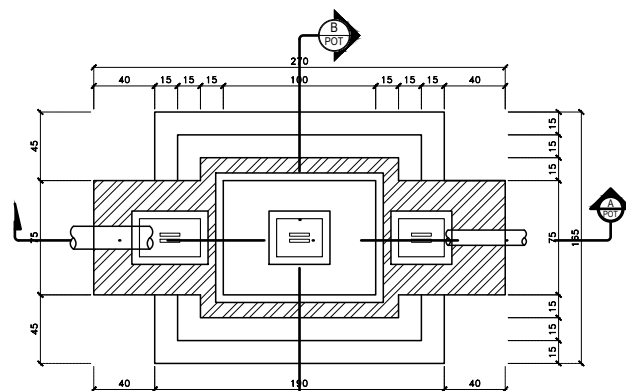

TAMPAK ATAS

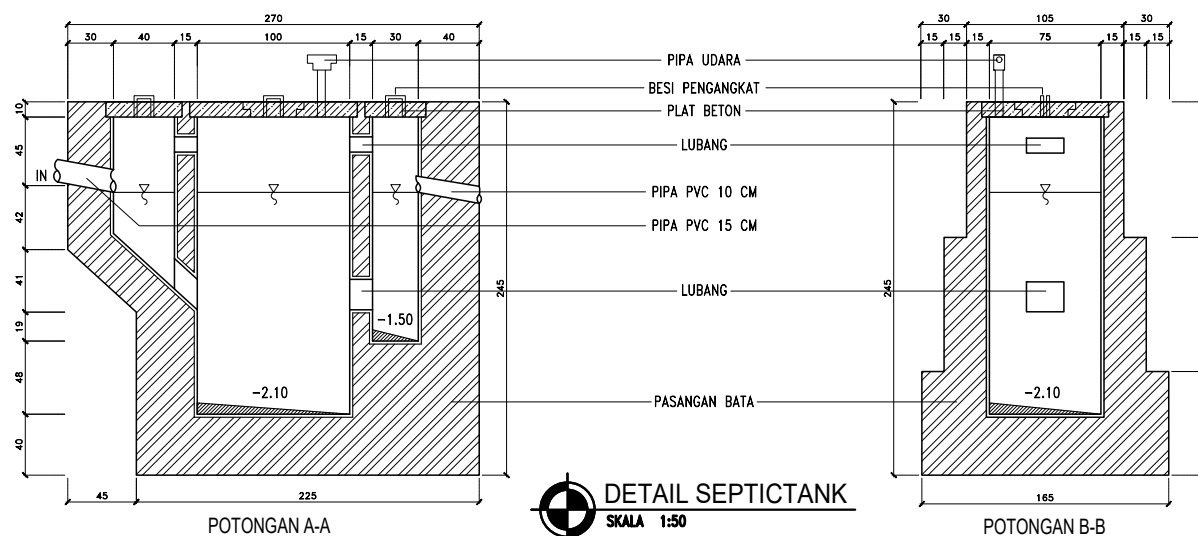

DETAIL SEPTICTANK

SKALA 1:50

POTONGAN B-B

POTONGAN A-A

CATATAN

NAMA PROYEK

RUMAH TINGGAL
TYPE 40 BAPAK MULYONO

LOKASI

Balong, Cangkringan,
sleman, Yogyakarta

DIGAMBAR

BAGAS PRATAMA A.
DRAFTER

DIPERIKSA OLEH

HARYO BUWONO, SH.
KONTRAKTOR

DISETUJUI OLEH

BAPAK MULYONO
OWNER

JUDUL GAMBAR

DETAIL SUMUR RESAPAN

SKALA

NO. LEMBAR


1:20

MEP-35

REVISI NOMER



TANGGAL

10/07/2026

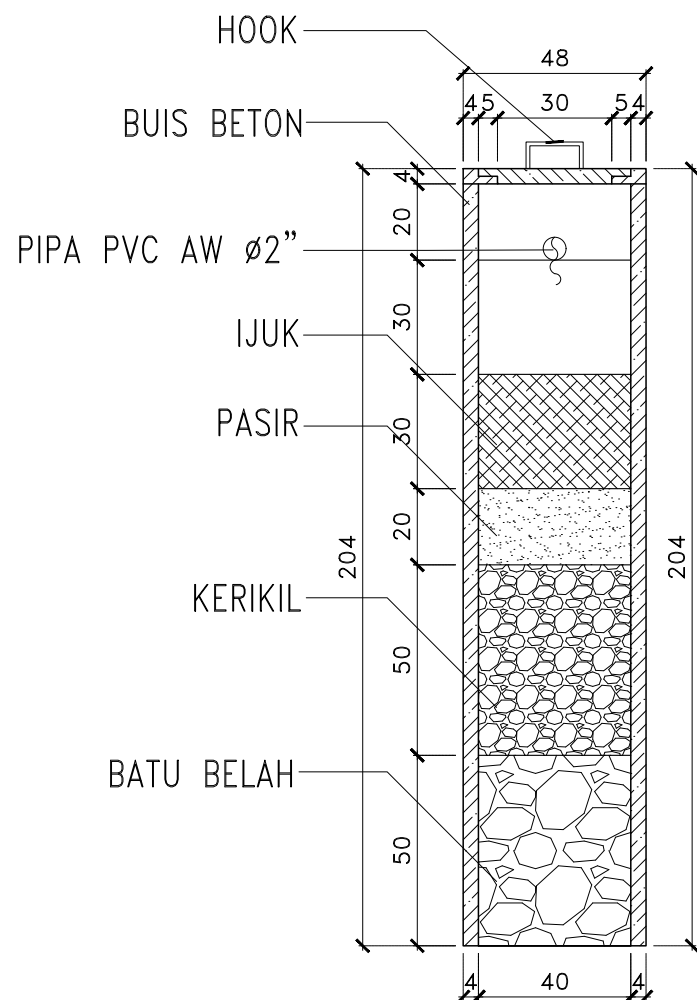

POTONGAN A-A SUMUR RESAPAN

SKALA 1:20

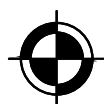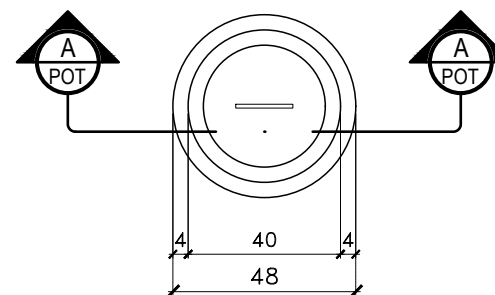

TAMPAK ATAS SUMUR RESAPAN

SKALA 1:20

CATATAN

NAMA PROYEK

RUMAH TINGGAL
TYPE 40 BAPAK MULYONO

LOKASI

Balong, Cangkringan,
sleman, Yogyakarta

DIGAMBAR

BAGAS PRATAMA A.
DRAFTER

DIPERIKSA OLEH

HARYO BUWONO, SH.
KONTRAKTOR

DISETUJUI OLEH

BAPAK MULYONO
OWNER

JUDUL GAMBAR

DETAIL BAK KONTROL

SKALA

NO. LEMBAR

1:20


MEP-36

REVISI NOMER

TANGGAL


10/07/2026

PENUTUP BETON

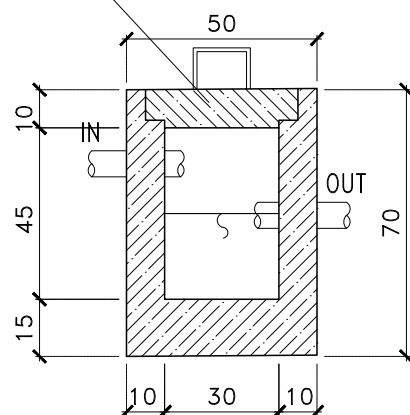

POTONGAN A-A BAK KONTROL

SKALA 1:20

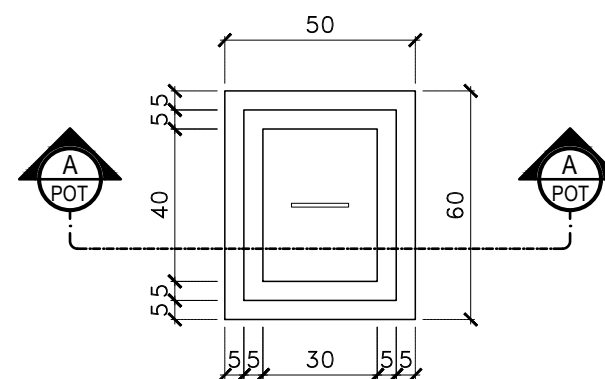

TAMPAK ATAS BAK KONTROL

SKALA 1:20

CATATAN

NAMA PROYEK

RUMAH TINGGAL
TYPE 40 BAPAK MULYONO

LOKASI

Balong, Cangkringan,
sleman, Yogyakarta

DIGAMBAR

BAGAS PRATAMA A.
DRAFTER

DIPERIKSA OLEH

HARYO BUWONO, SH.
KONTRAKTOR

DISETUJUI OLEH

BAPAK MULYONO
OWNER

JUDUL GAMBAR

DETAIL ROOF DRAIN

SKALA

NO. LEMBAR


1:20

MEP-37

REVISI NOMER


TANGGAL

10/07/2026

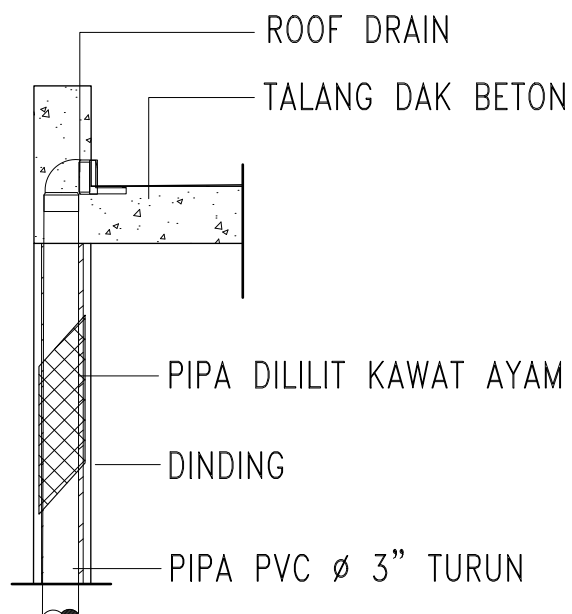

DETAIL ROOF DRAIN

SKALA 1:20

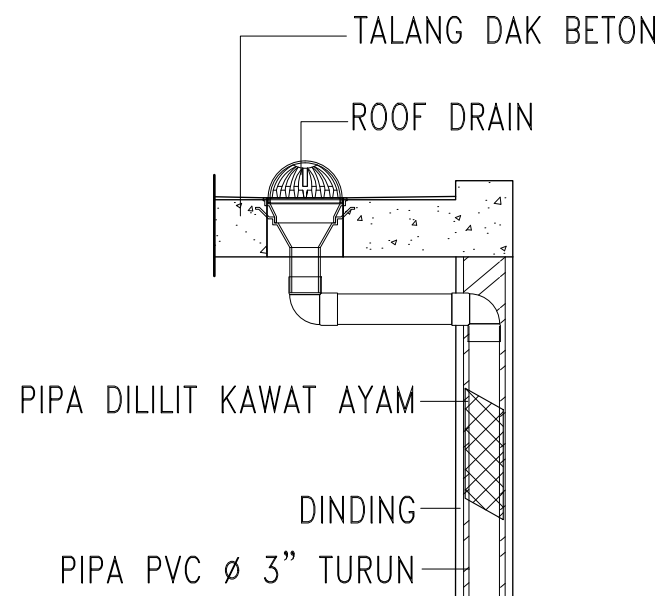

DETAIL ROOF DRAIN

SKALA 1:20